


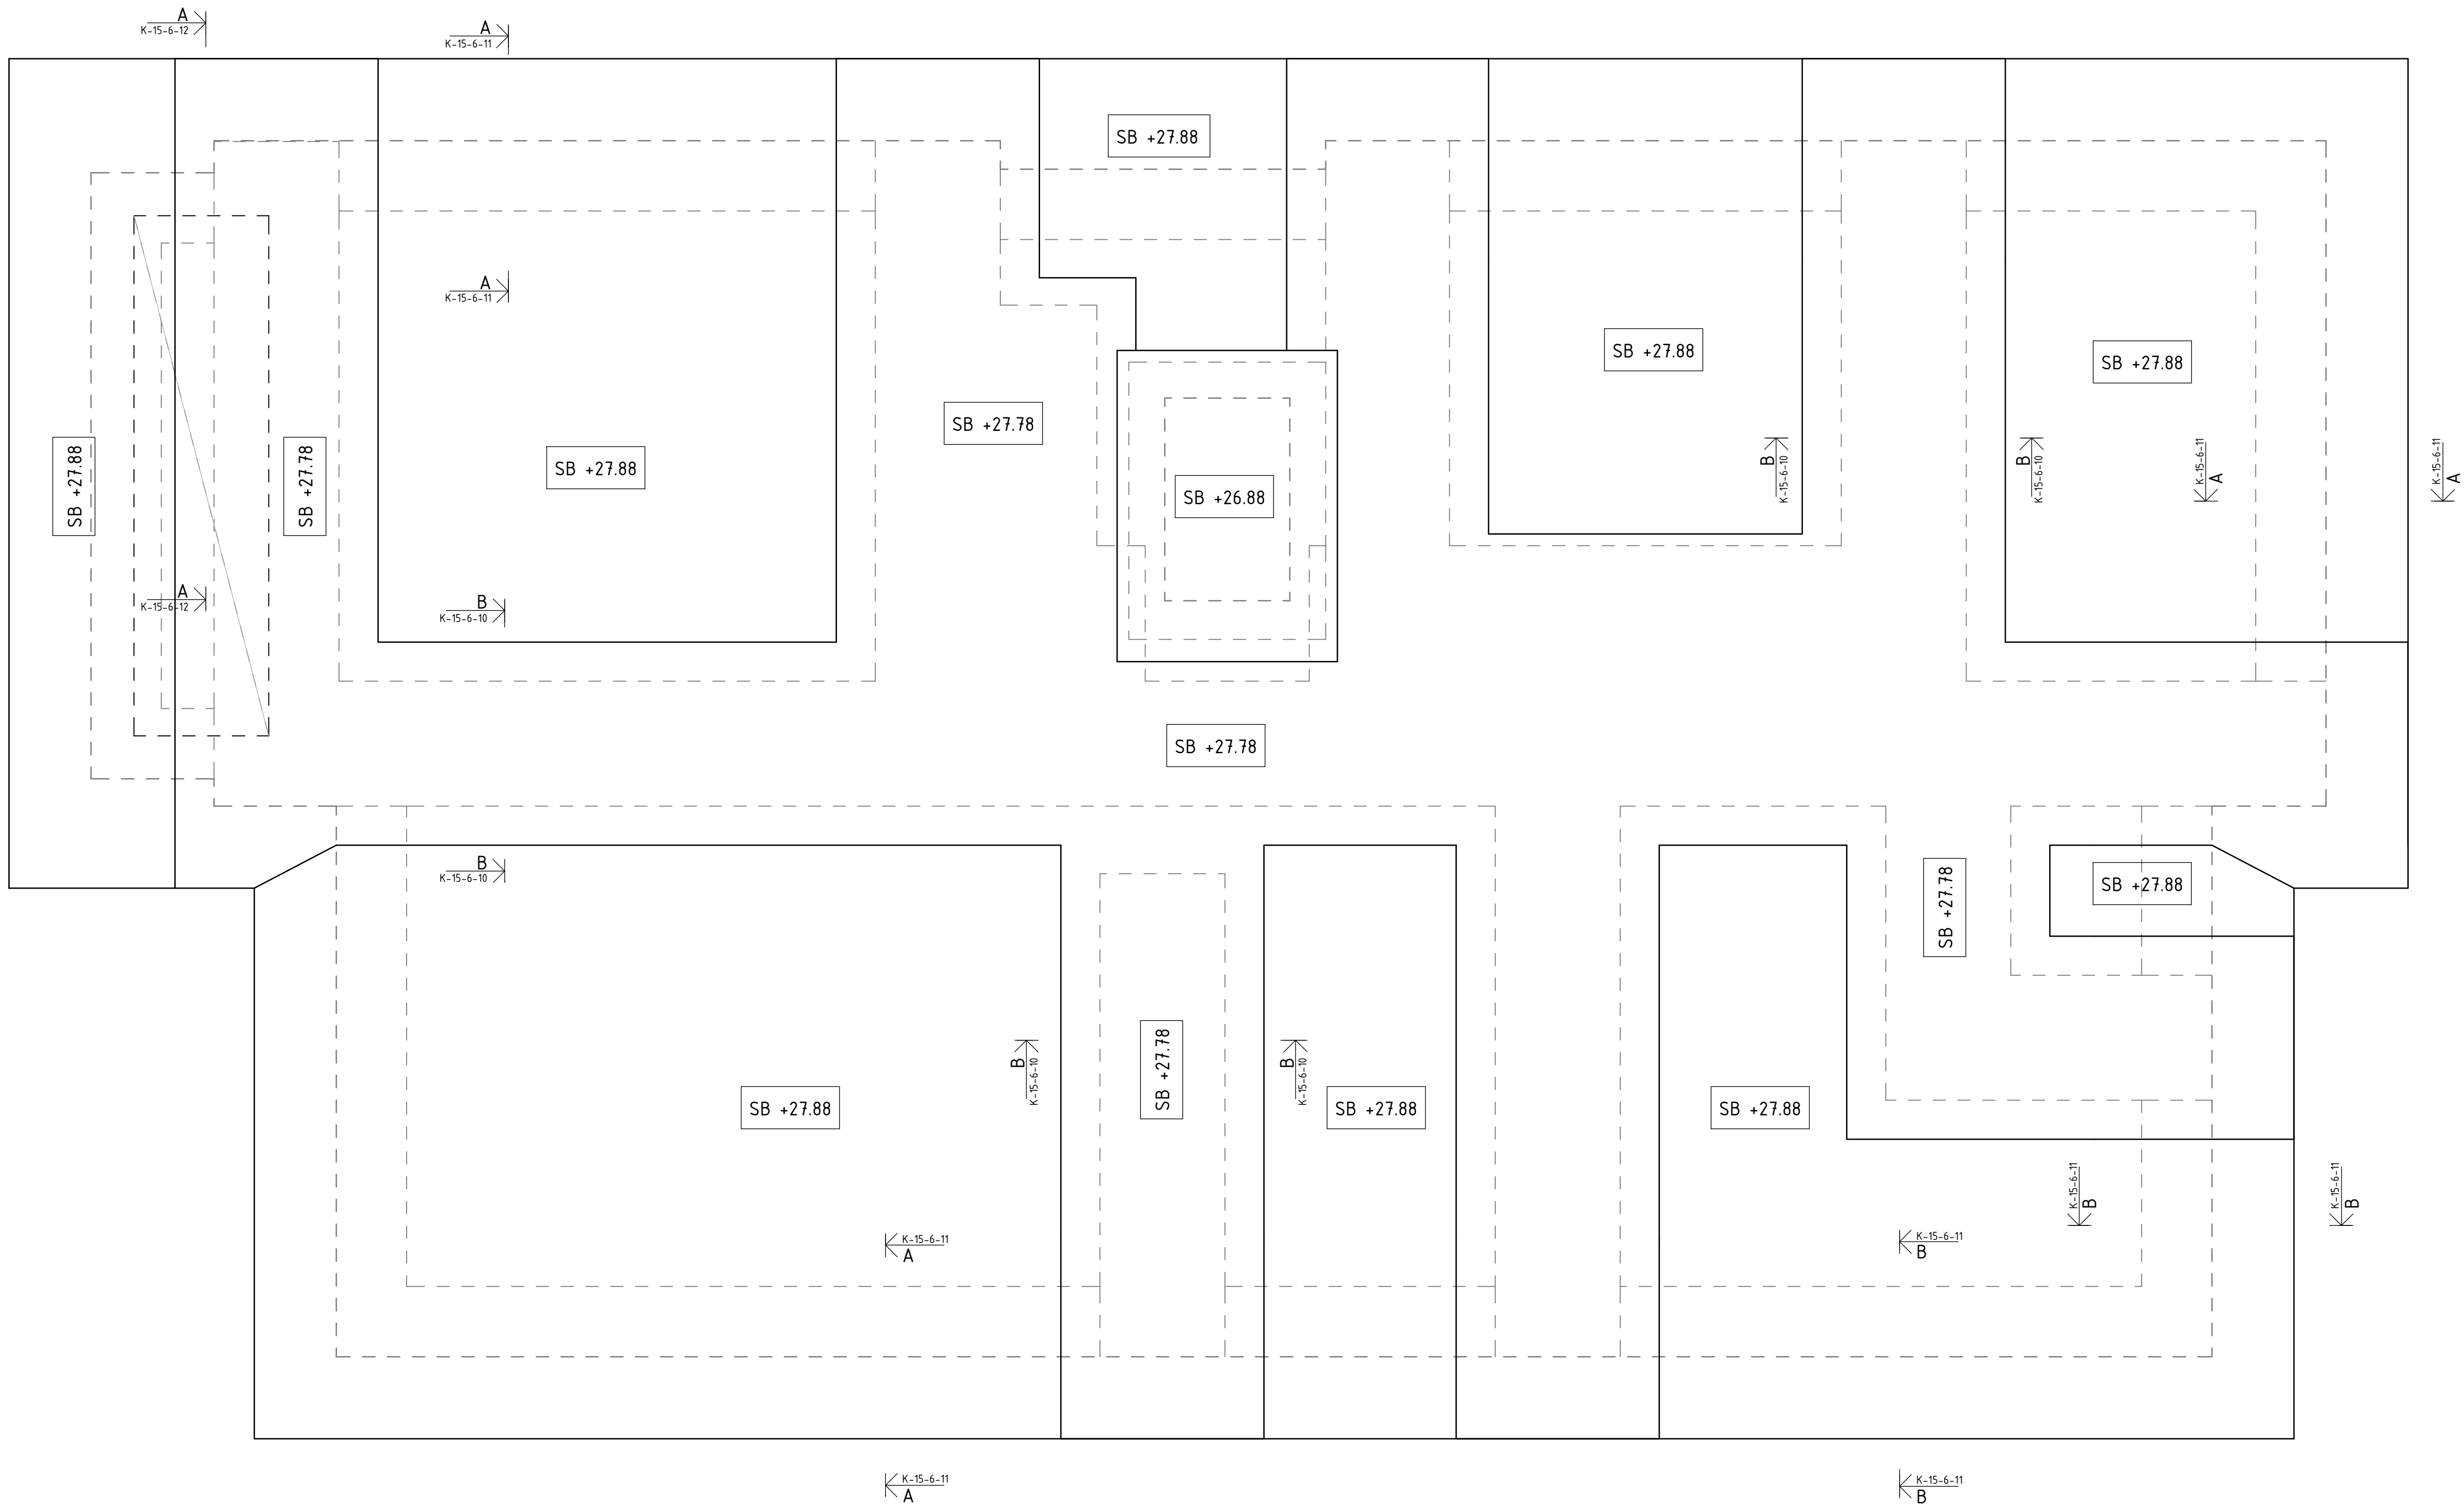

FÖRKLARINGAR

GROVSCHAKTPLAN, SCHAKT FÖR
INSTALLATIONER REDOVISAS EJ.

HISSGROPSDJUP ANTAGEN, SCHAKT UTREDS
OCH ANPASSAS AV TE.

SLÄNTLUTNING 1:1,5 DÄR ANNAT EJ ANGES.

FÖRESKRIFTER

SE RITNING K-00-0-00

HÄNVISNINGAR

FÖRESKRIFTER K-00-0-00
PRINCIPDETALJER INKL. TYPDETALJER
PRINCIPDETALJER K-15-6-10
UTVÄNDIG TRAPPA K-15-6-12

Bef.	Ändringen avser	Datum	Sign
SYSTEMHANDLING			
VärmdöBostäder			
Orienteringsfigur			
E	ELKONSULT E-TEC AB	073-6655510	
G	TREELINE CONSULTING AB	073-0844329	
X	K KÄVER & MELLIN	072-7326731	
L	C.F. MØLLER SVERIGE AB	08-55576000	
M	VIKEN MILJÖKONSULT AB	070-6526445	
V	DLV AB	076-0224797	
VA	NIRAS SWEDEN AB	08-50384400	
Uppdragsnr.	Ritad/konstr. av	Handläggare	
24222	FE	FE	
Datum	Ansvarig		
2024-11-29	ANDERS HEDBERG		
SKEVIK, VÄRMDÖ			
SKEVIK 1:190			
Schaktplan Hus A			
Skala a1	Skala a3	Nummer	Bef.
1:50	1:100	K-11-1-109	