


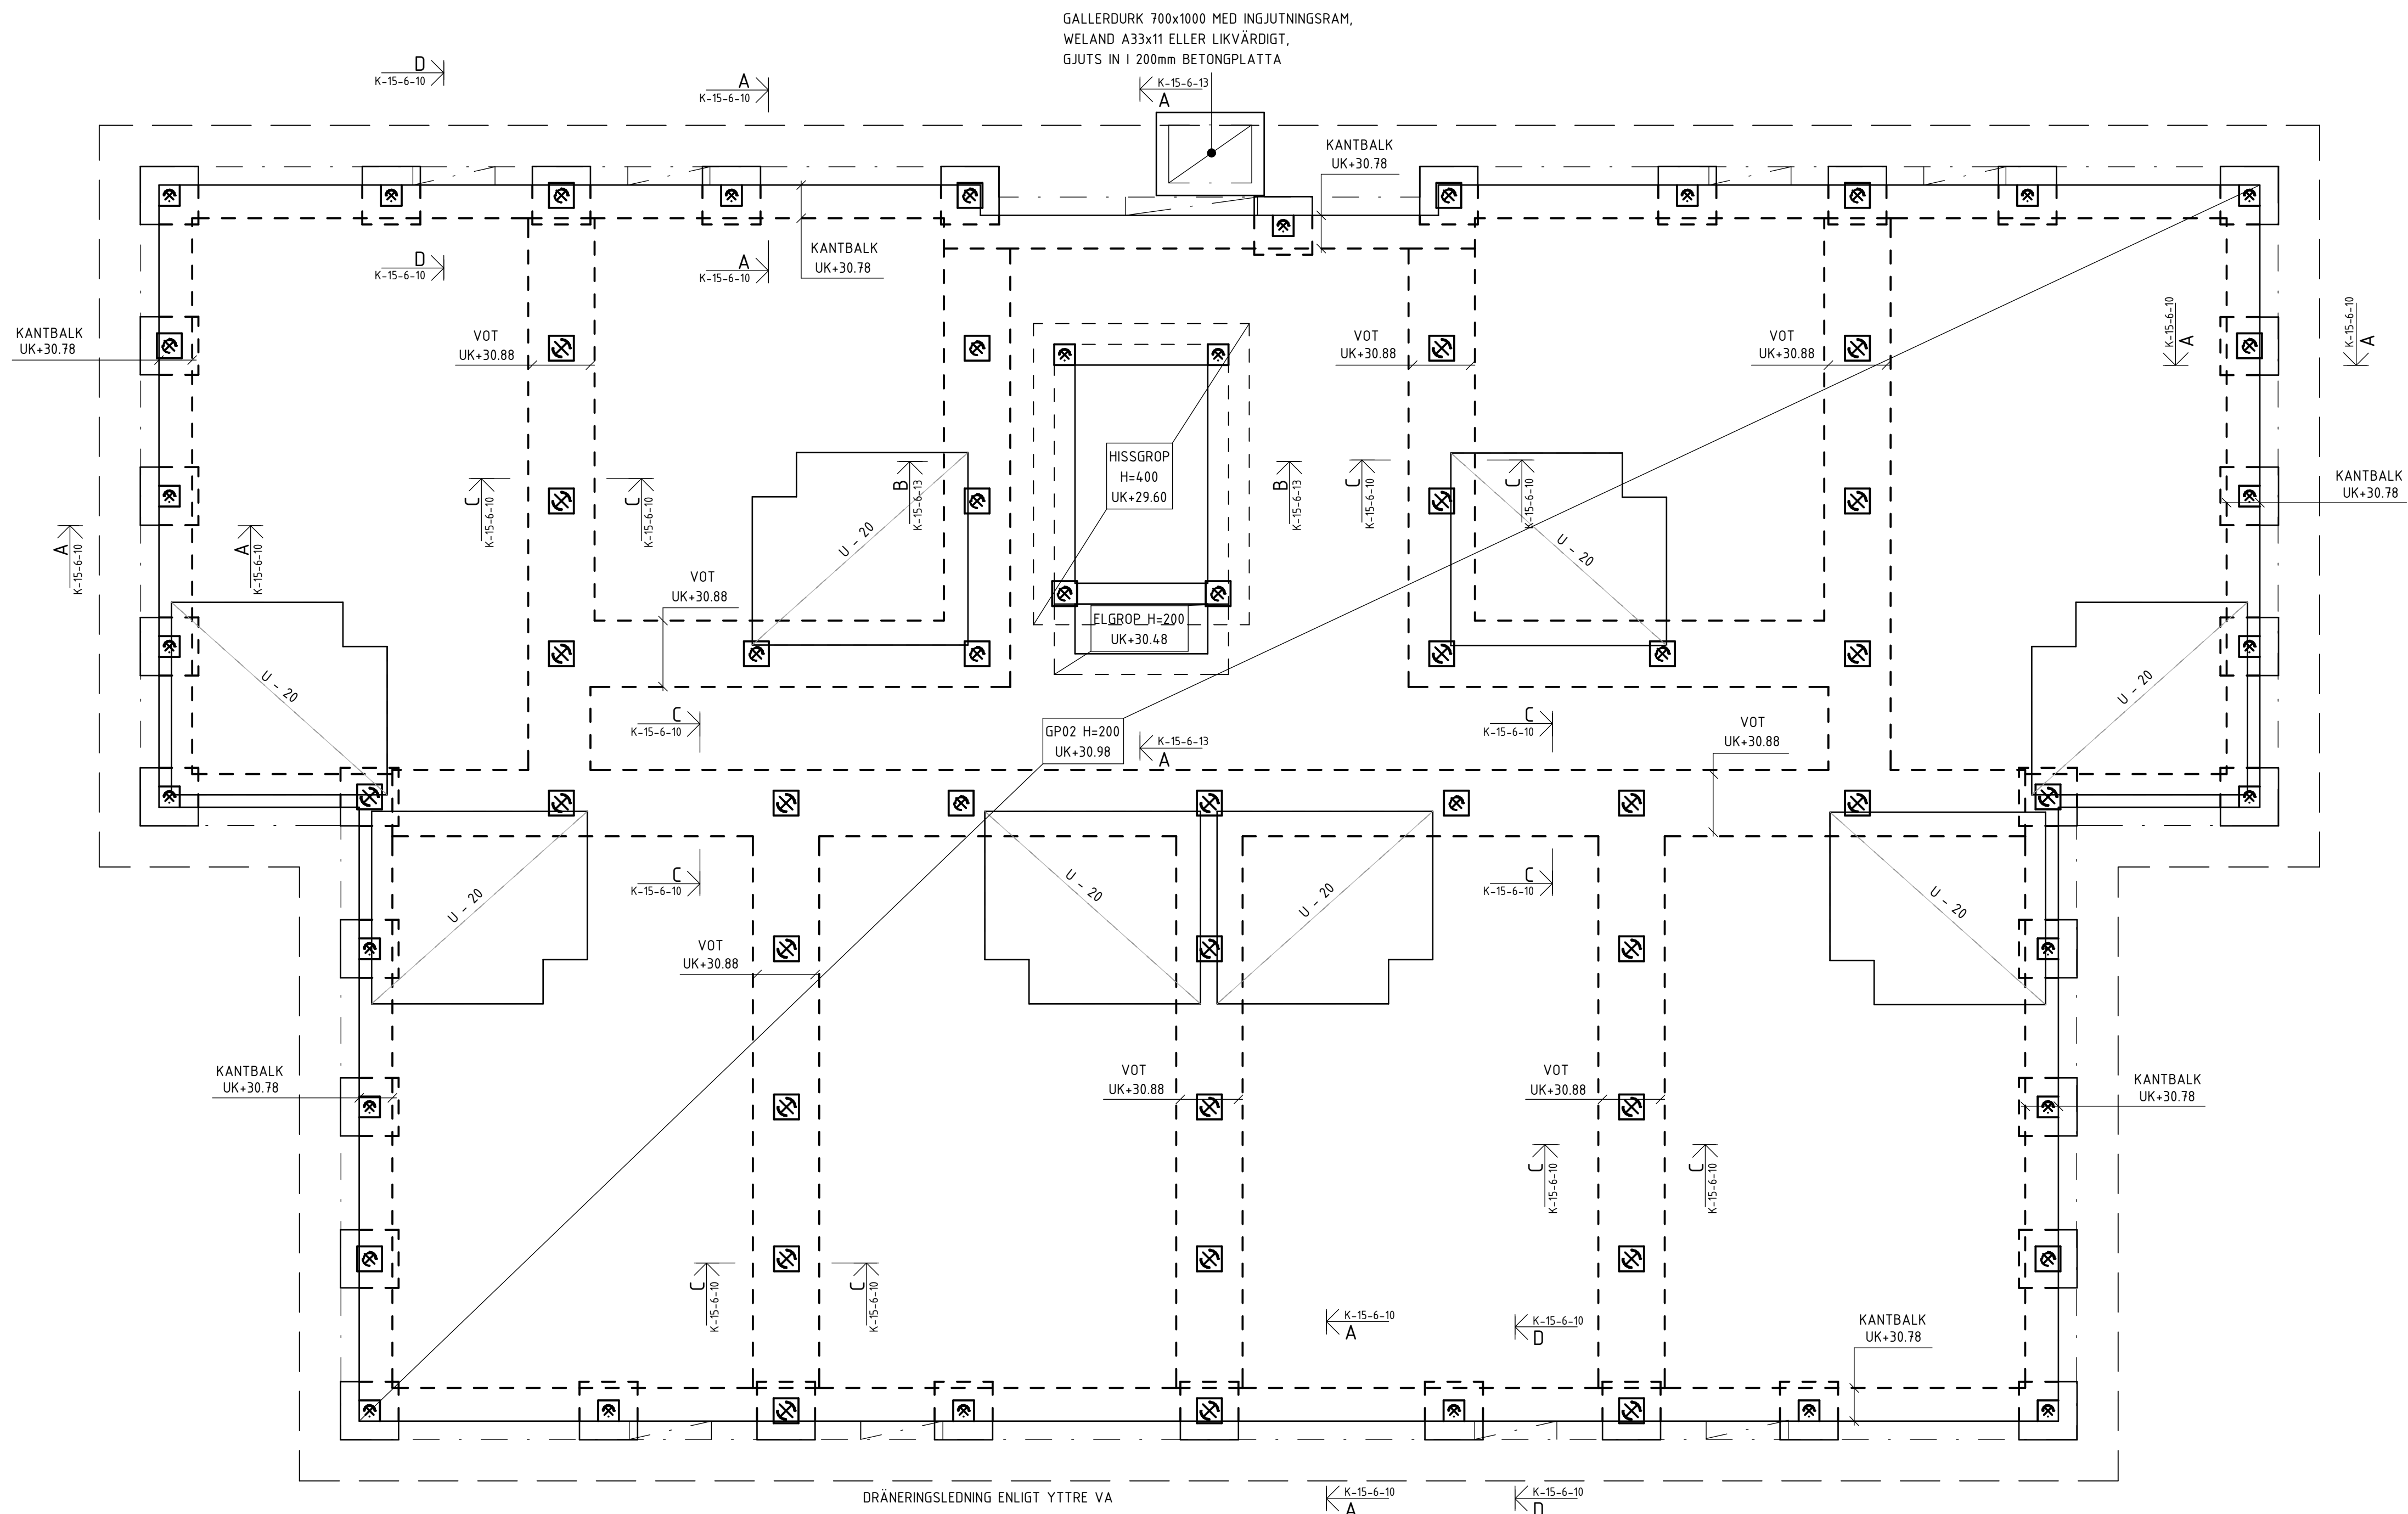

FÖRKLARINGAR

GP = GRUNDPLATTA, SE K-15-6-10

U - 20 = 20mm URSPARING I ÖK BETONG
FÖR BADRUM

HISSGROPSDJUP ANTAGEN TILL 1200mm,
UTREDS AV TE.

ELGROPSDJUP ANTAGEN TILL 500mm,
UTREDS AV TE.

FÖRESKRIFTER

SE RITNING

K-00-0-00

HÄNVISNINGAR

FÖRESKRIFTER

K-00-0-00

PRINCIPDETALJER INKL. TYPDETALJER

K-15-6-10

HISSGROP HUS B

K-15-6-13

VA-PLAN


R-51-1-01

Bet. Ändringen avser Datum Sign

SYSTEMHANDLING

VärmdöBostäder

Orienteringsfigur

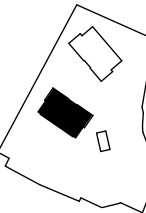

E	ELKONSULT E-TEC AB	073-6655510
G	TREELINE CONSULTING AB	073-0844329
X	K KÅVER & MELLIN	072-7326731
L	C.F. MØLLER SVERIGE AB	08-55576000
M	VIKEN MILJÖKONSULT AB	070-6526445
V	DLV AB	076-0224797
VA	NIRAS SWEDEN AB	08-50384400

Uppdragsnr.	Ritad/konstr. av	Handläggare
24222	FE	FE

Datum	Ansvarig
2024-11-29	ANDERS HEDBERG

SKEVIK, VÄRMDÖ
SKEVIK 1:190

Grundplan Hus B

Skala a1	Skala a3	Nummer	Bet.
1:50	1:100	K-15-1-209	