
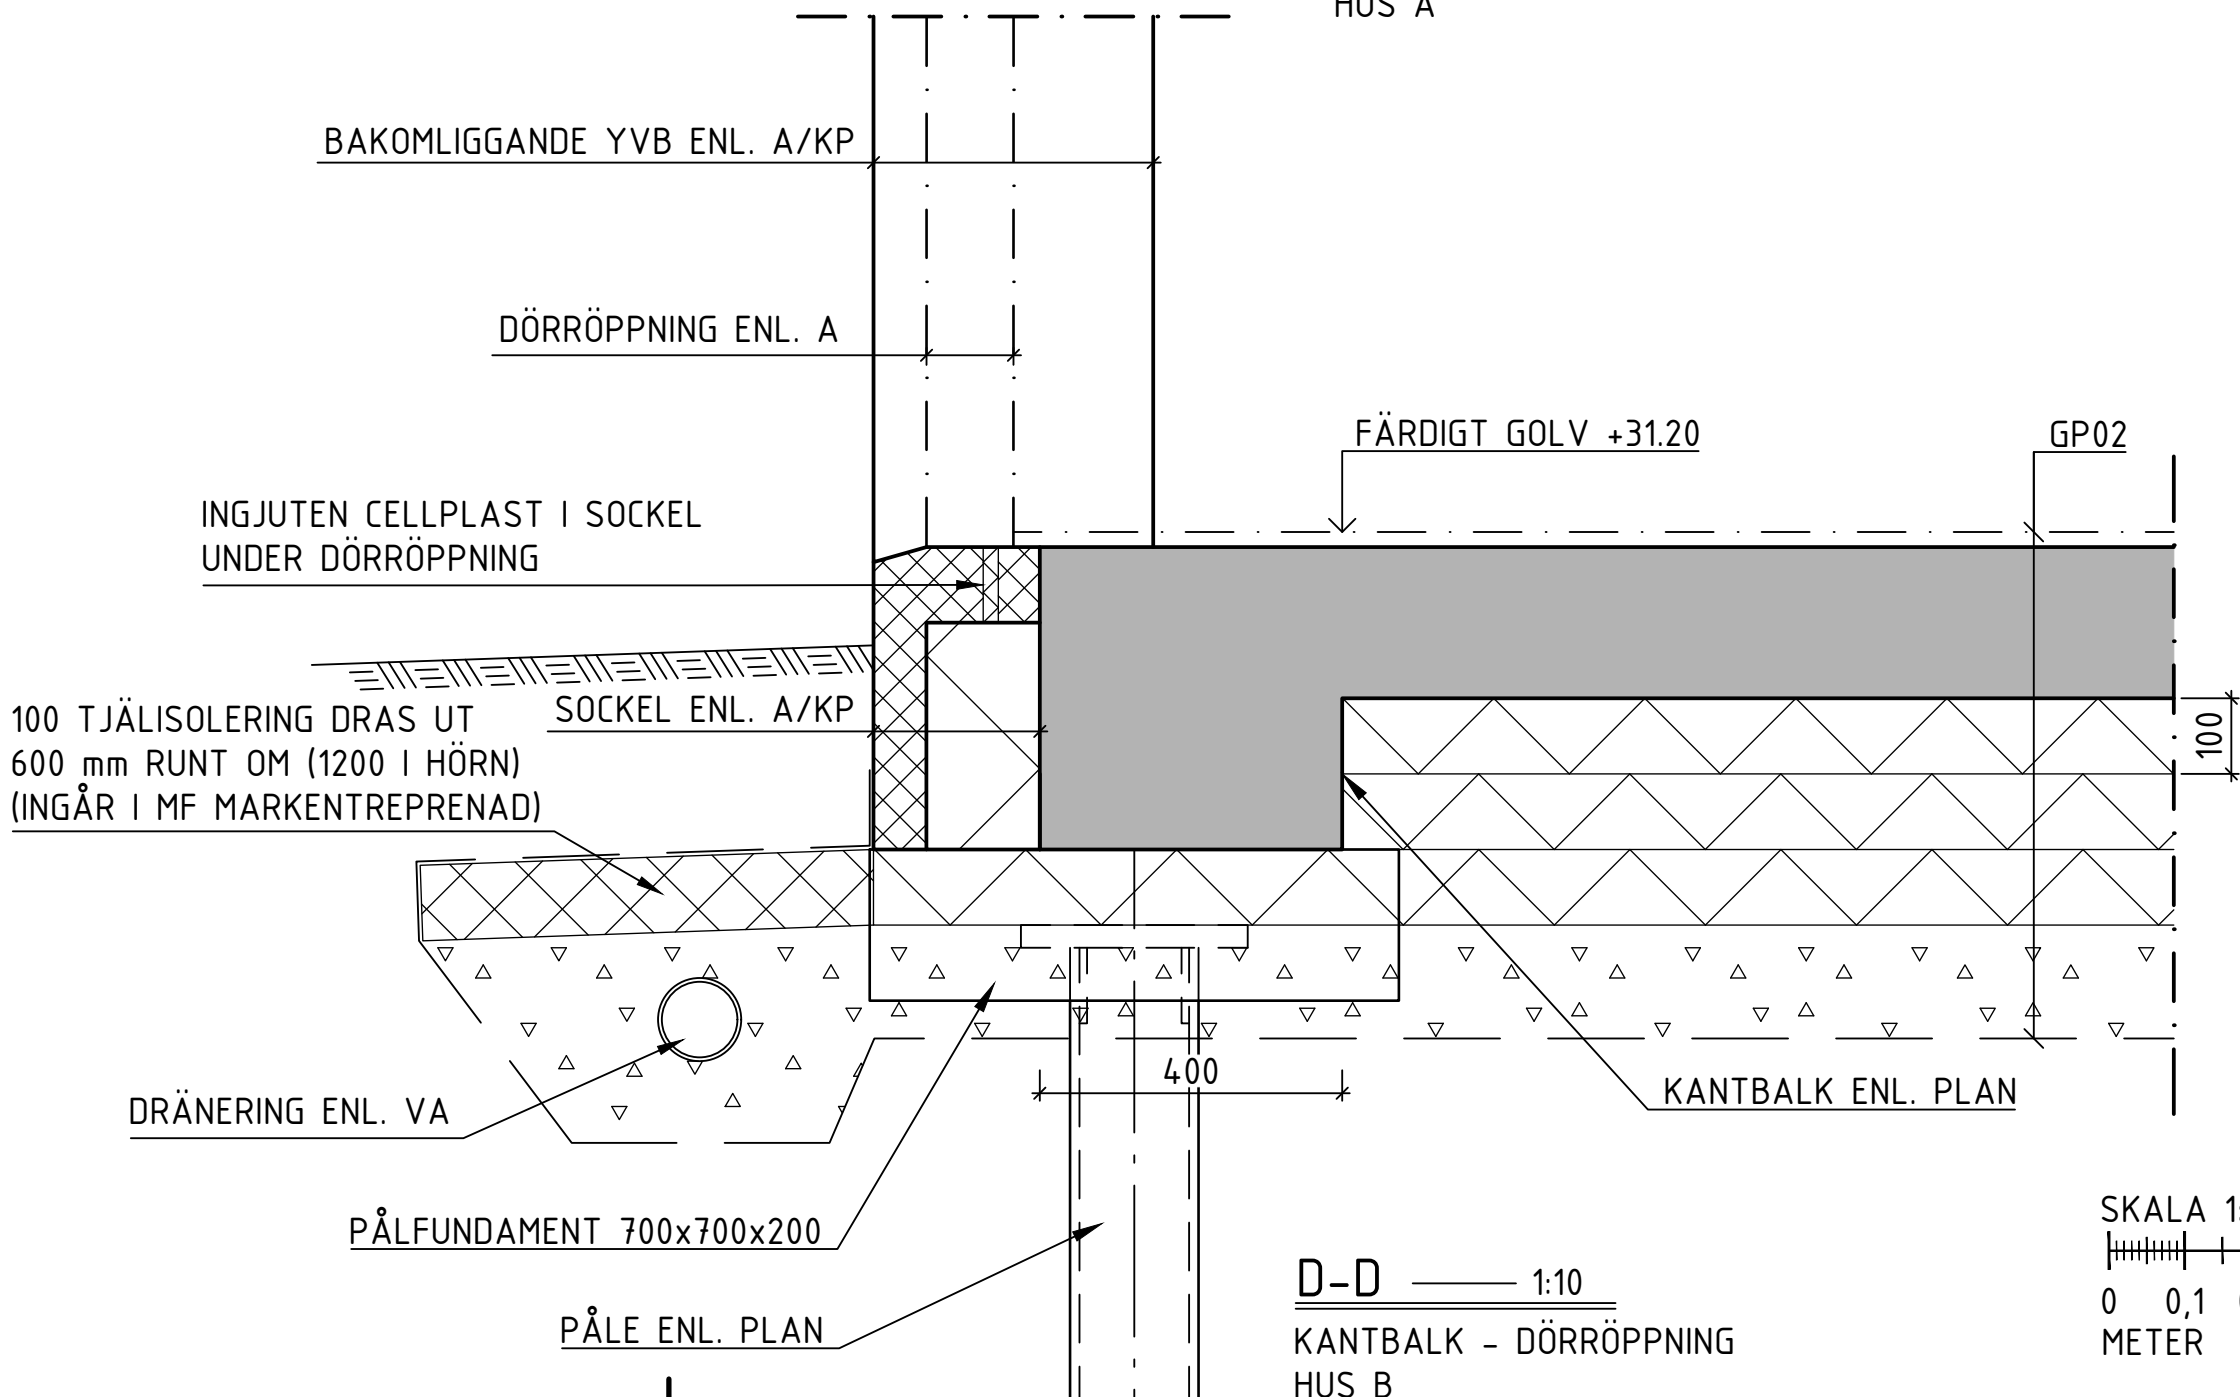
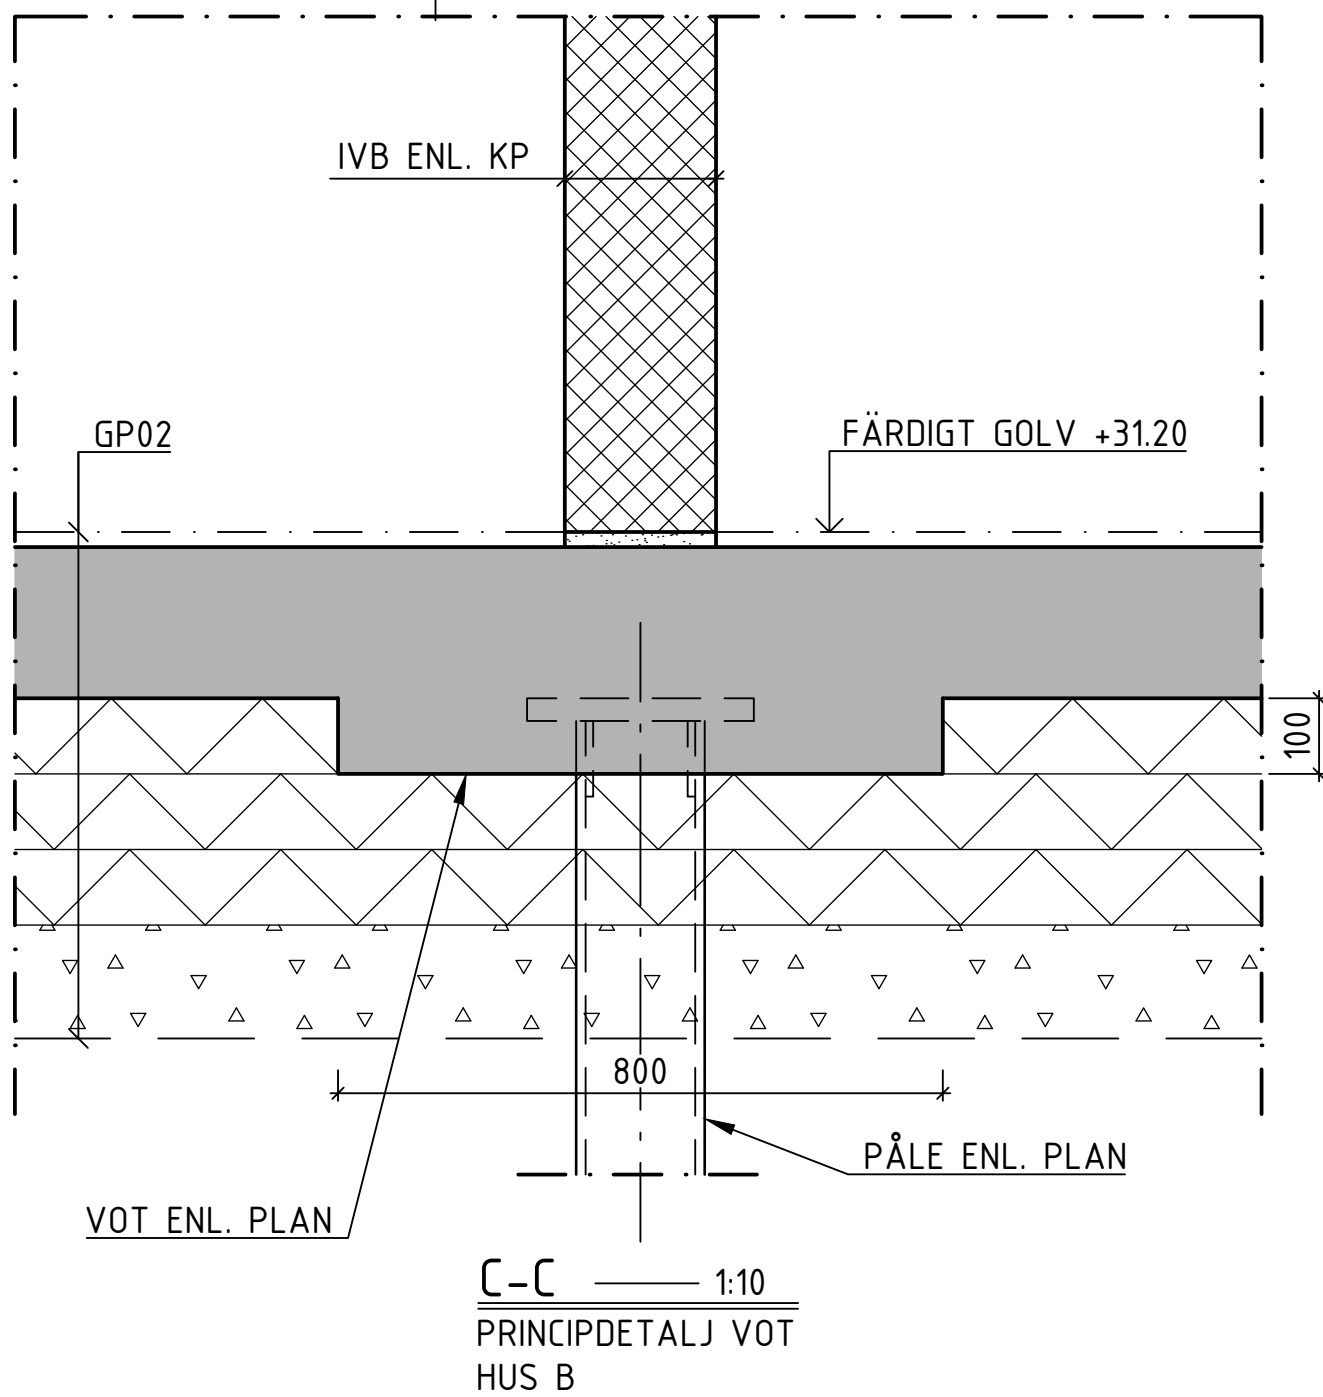
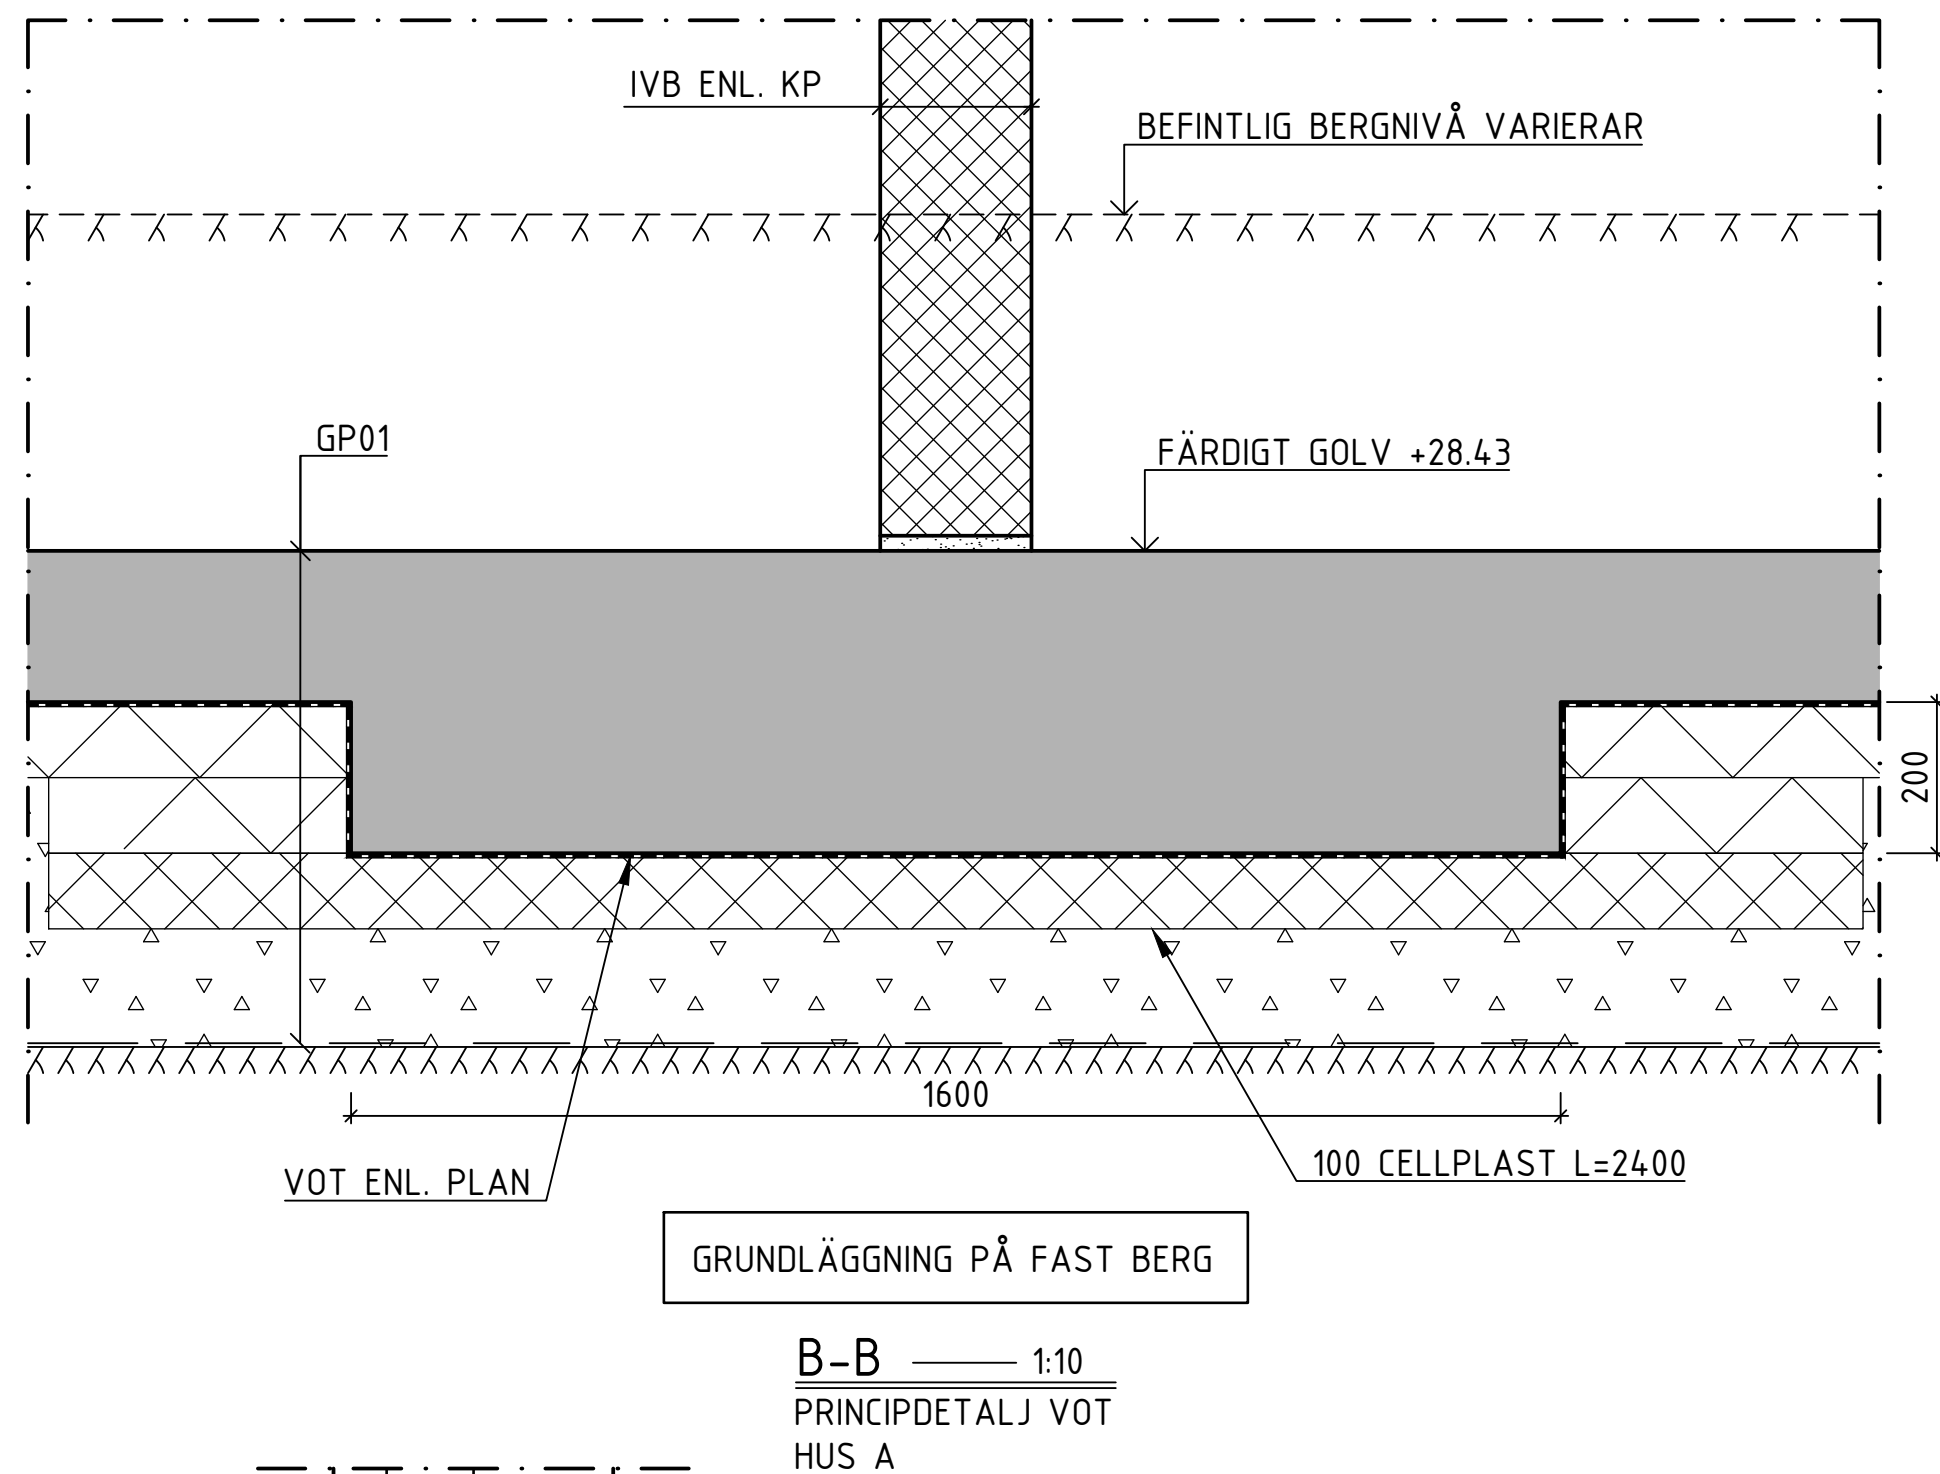
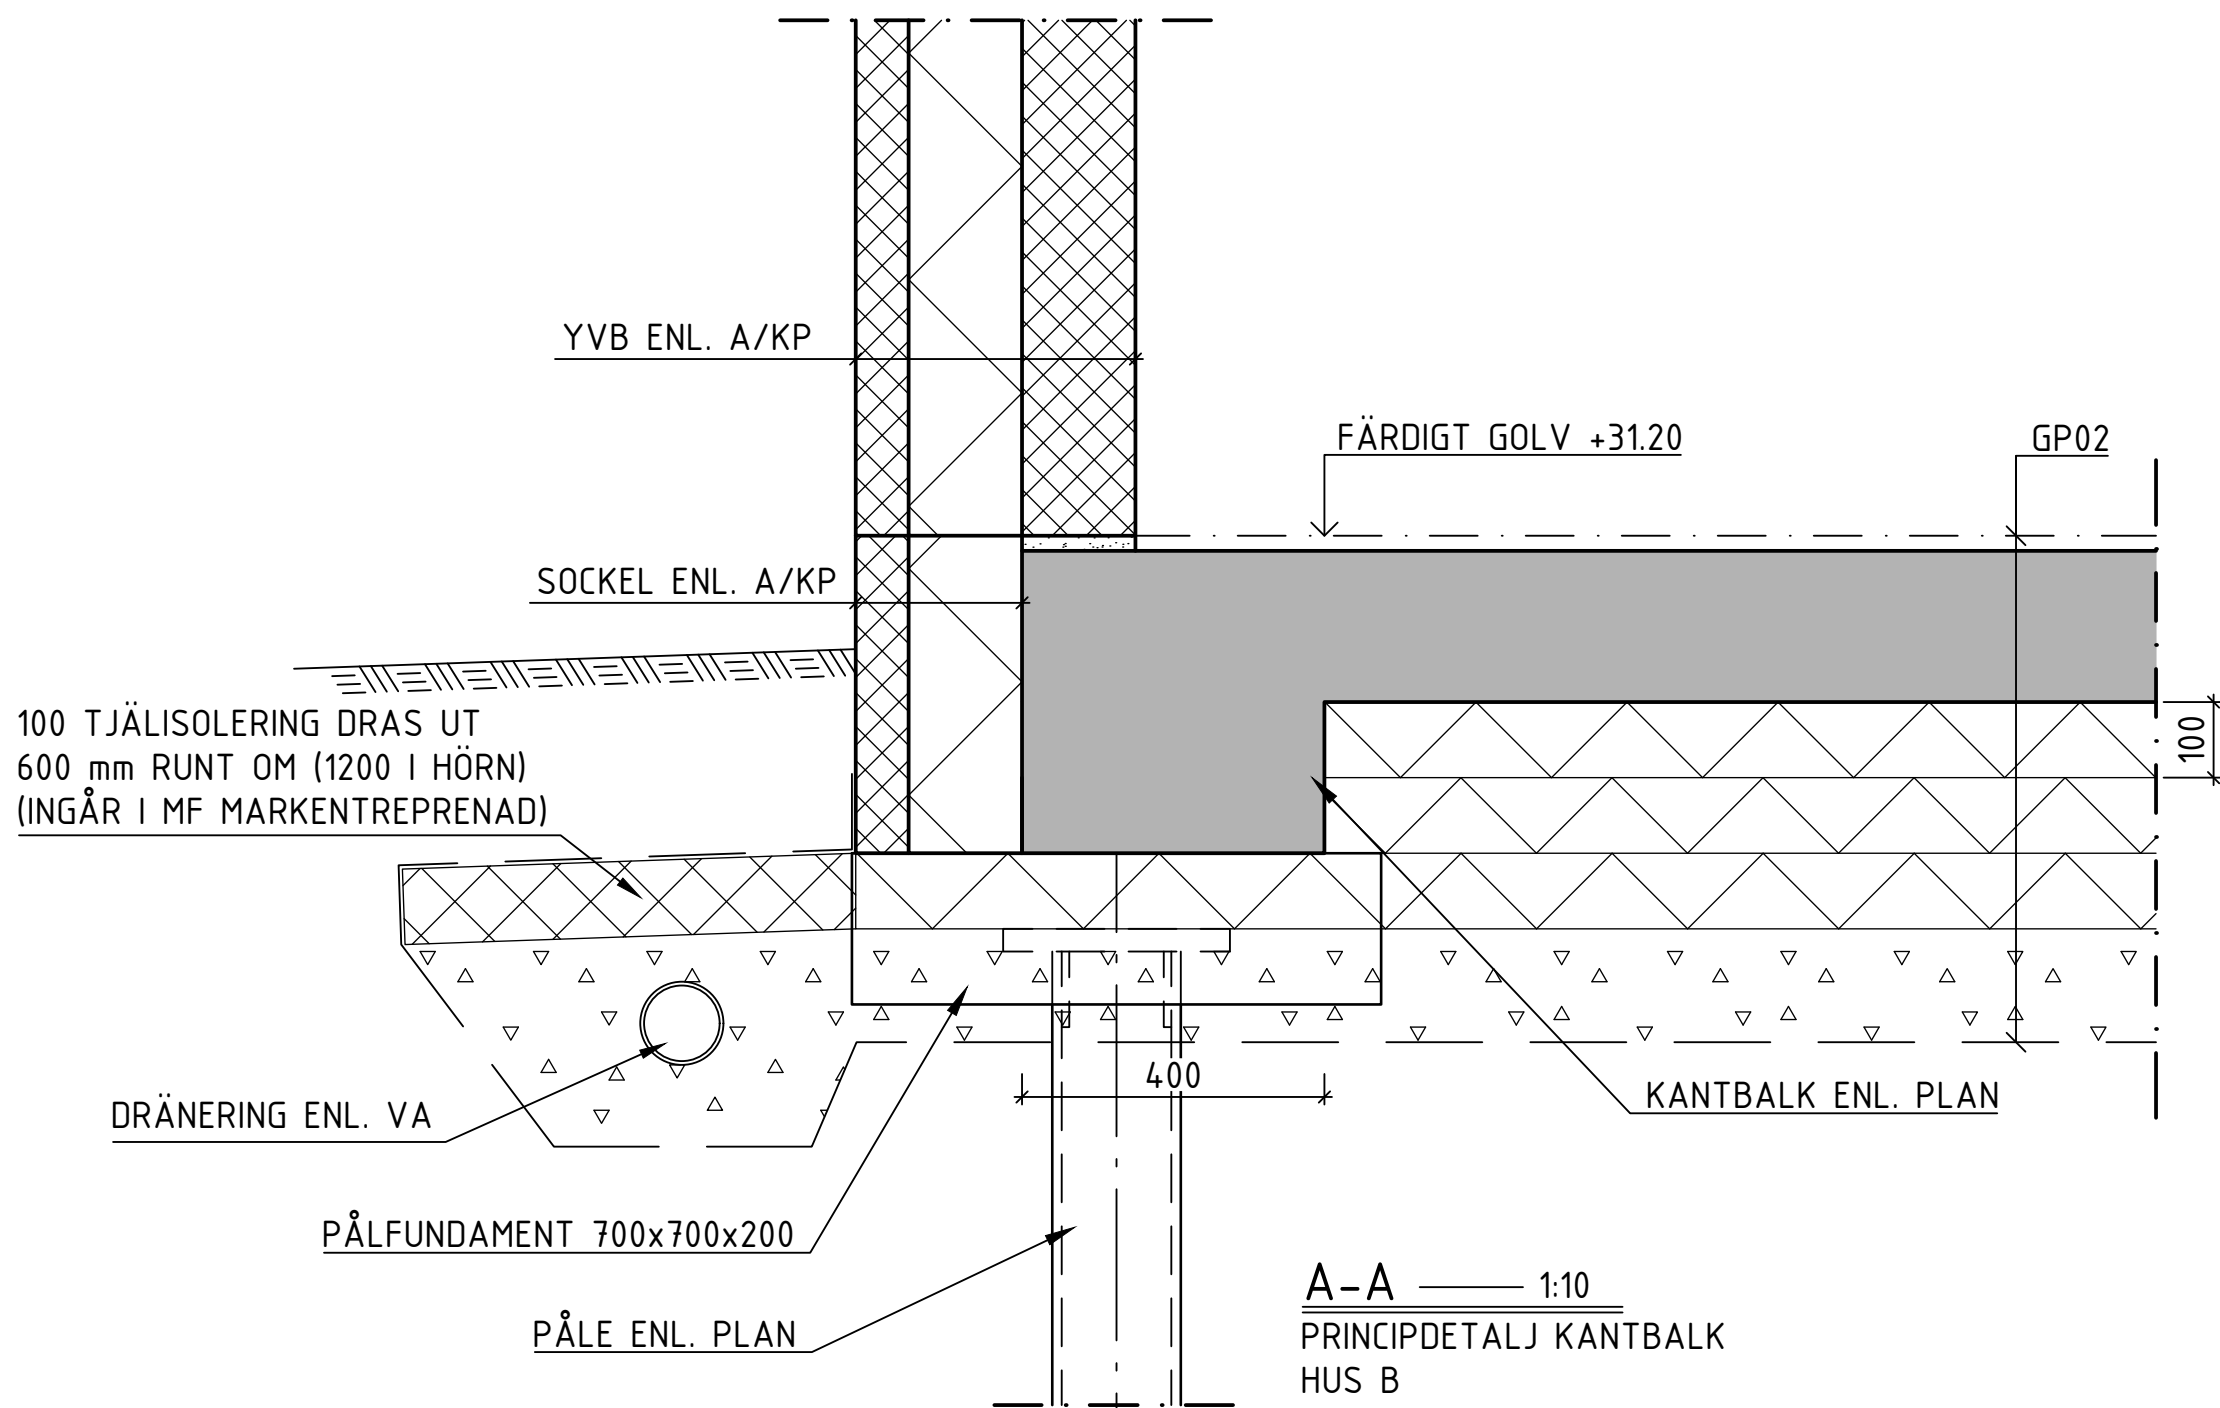


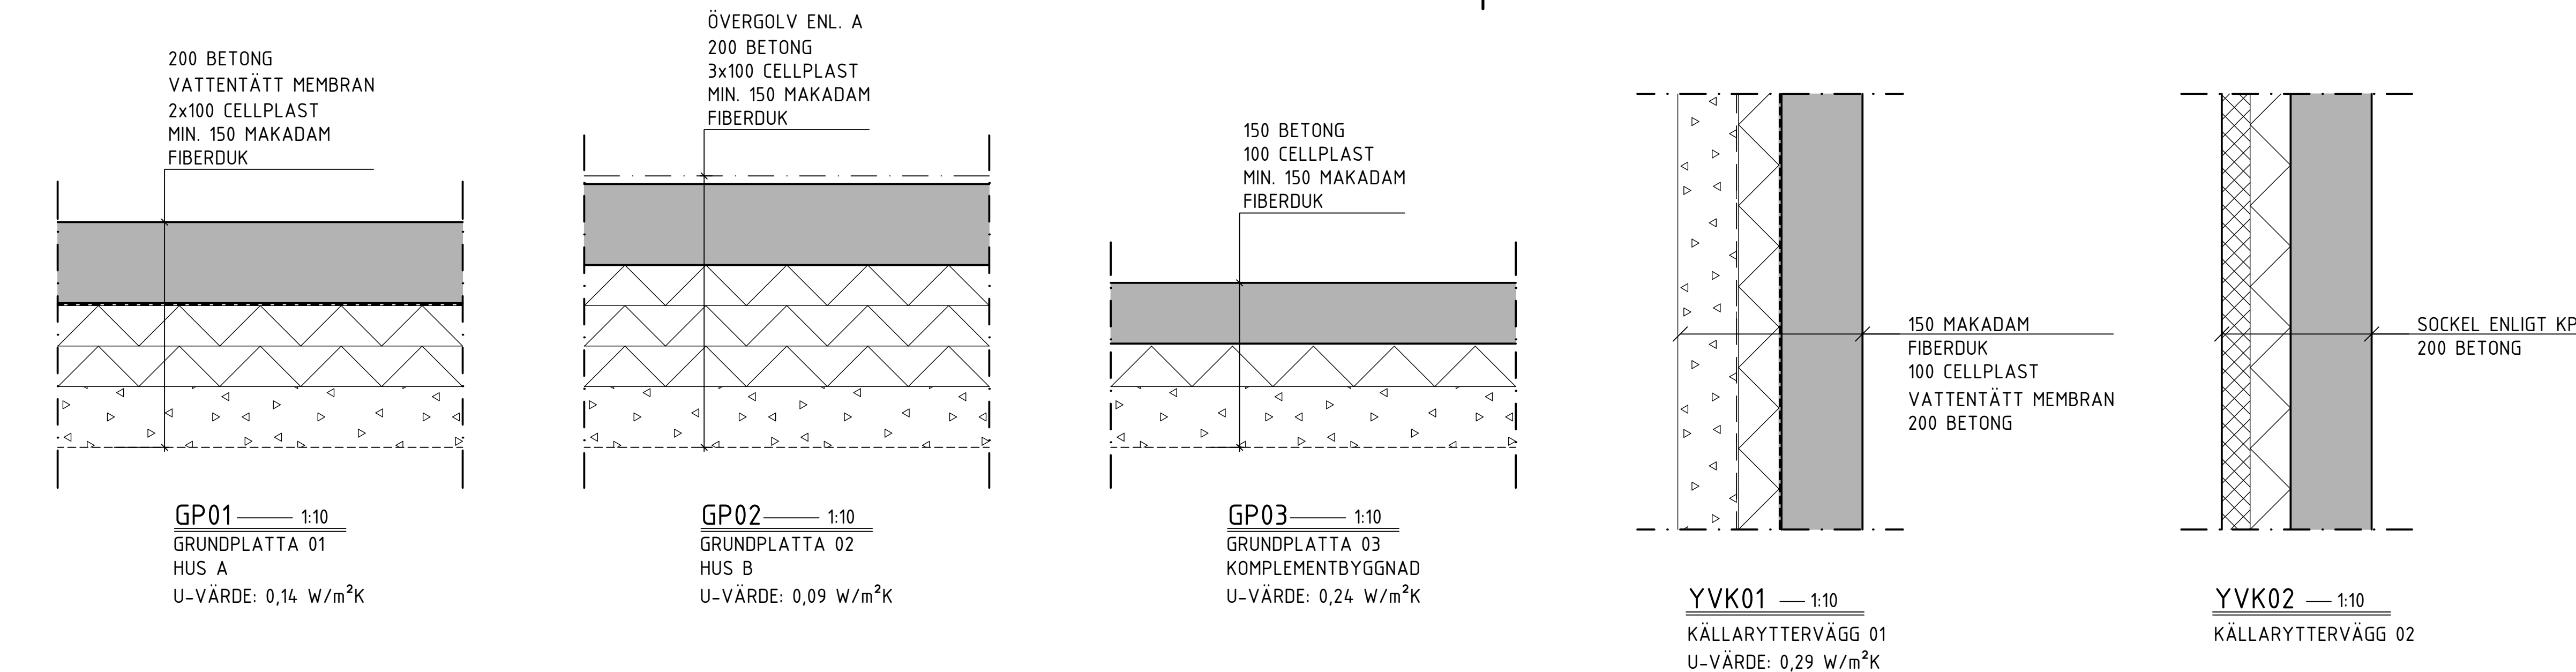

FÖRKLARINGAR

FÖRESKRIFTER

SE RITNING K-00-0-00

HÄNVISNINGAR


FÖRESKRIFTER K-00-0-00

Bef.	Andringen avser	Datum	Sign
------	-----------------	-------	------

SYSTEMHANDLING



Orienteringsfigur

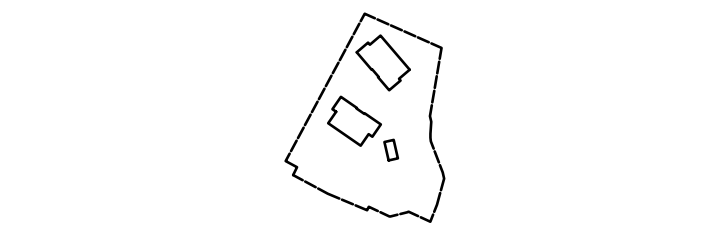

E	ELKONSULT E-TEC AB	073-6655510
G	TREELINE CONSULTING AB	073-0844329
K	KÄVER & MELLIN	072-7326731
L	C.F. MØLLER SVERIGE AB	08-55576000
M	VIKEN MILJÖKONSULT AB	070-6526445
V	DLV AB	076-0224797
VA	NIRAS SWEDEN AB	08-50384400

Uppdragsnr. 24222	Ritad/konstr. av FE	Handläggare FE
Datum 2024-11-29	Ansv. ing ANDERS HEDBERG	

SKEVIK, VÄRMDÖ
SKEVIK 1:190
Principdetaljer inkl. typdetaljer

Skala a1	Skala a3	Nummer	Bef.
1:10	1:20	K-15-6-10	