
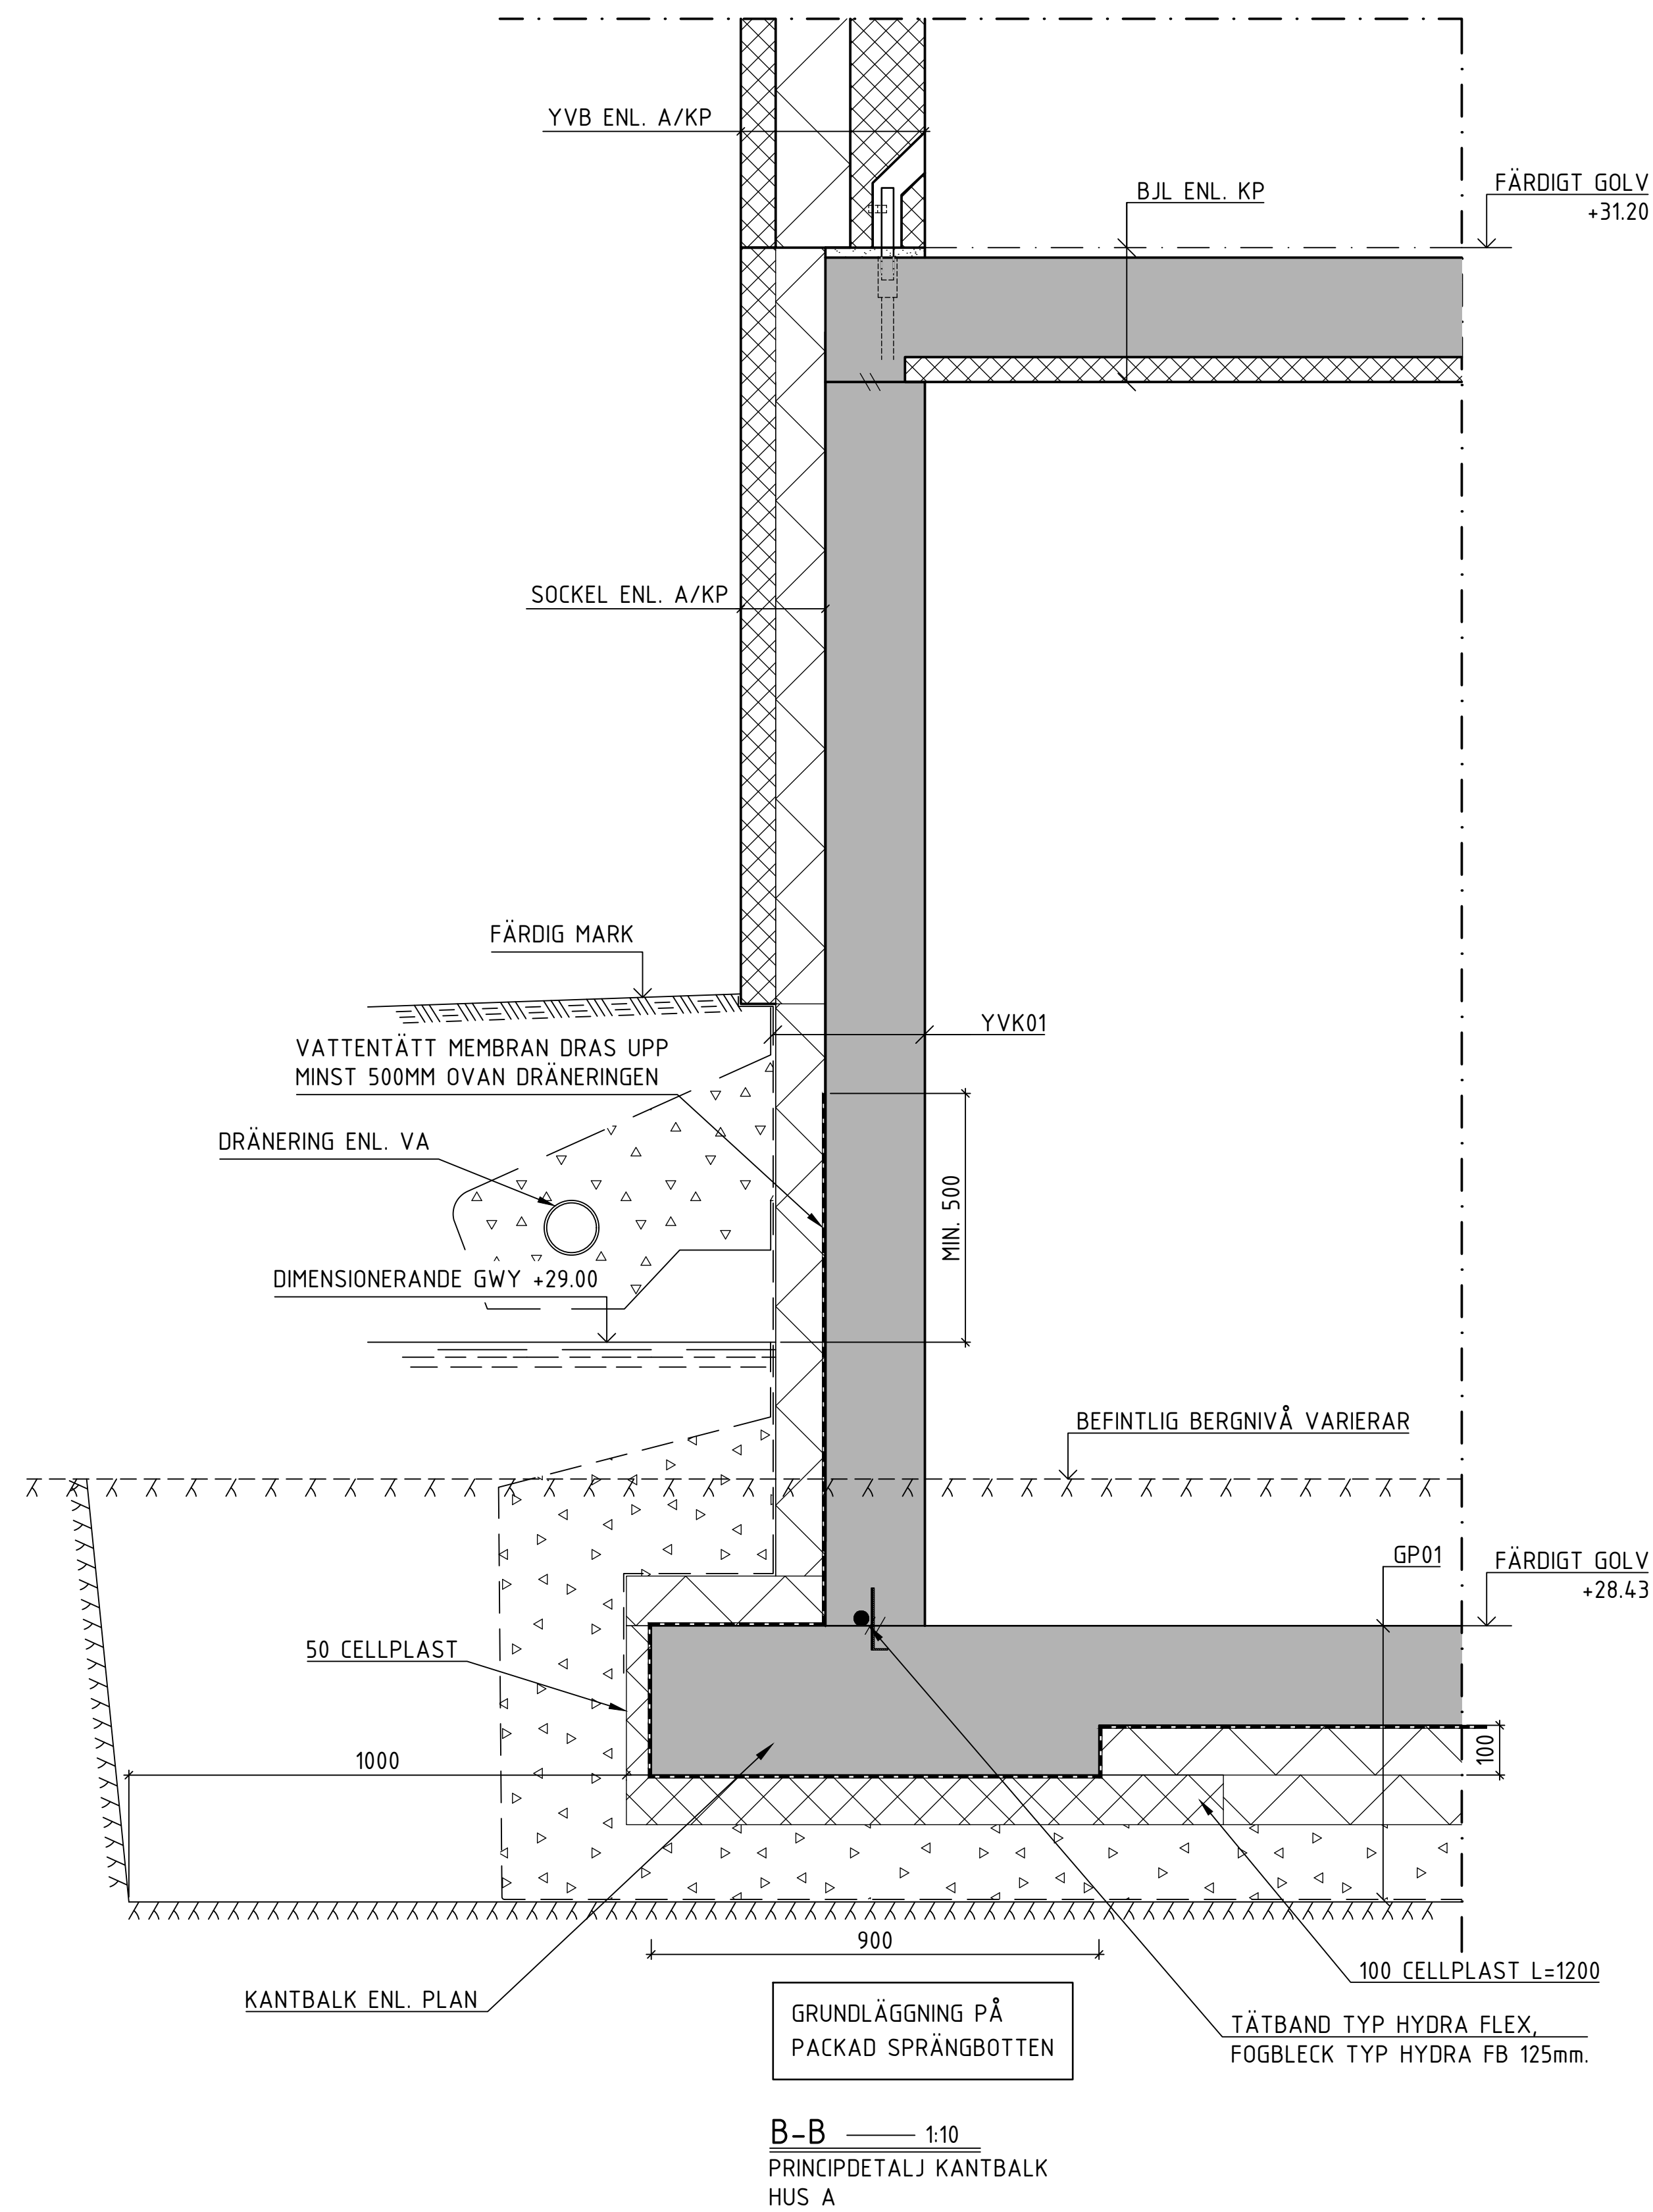


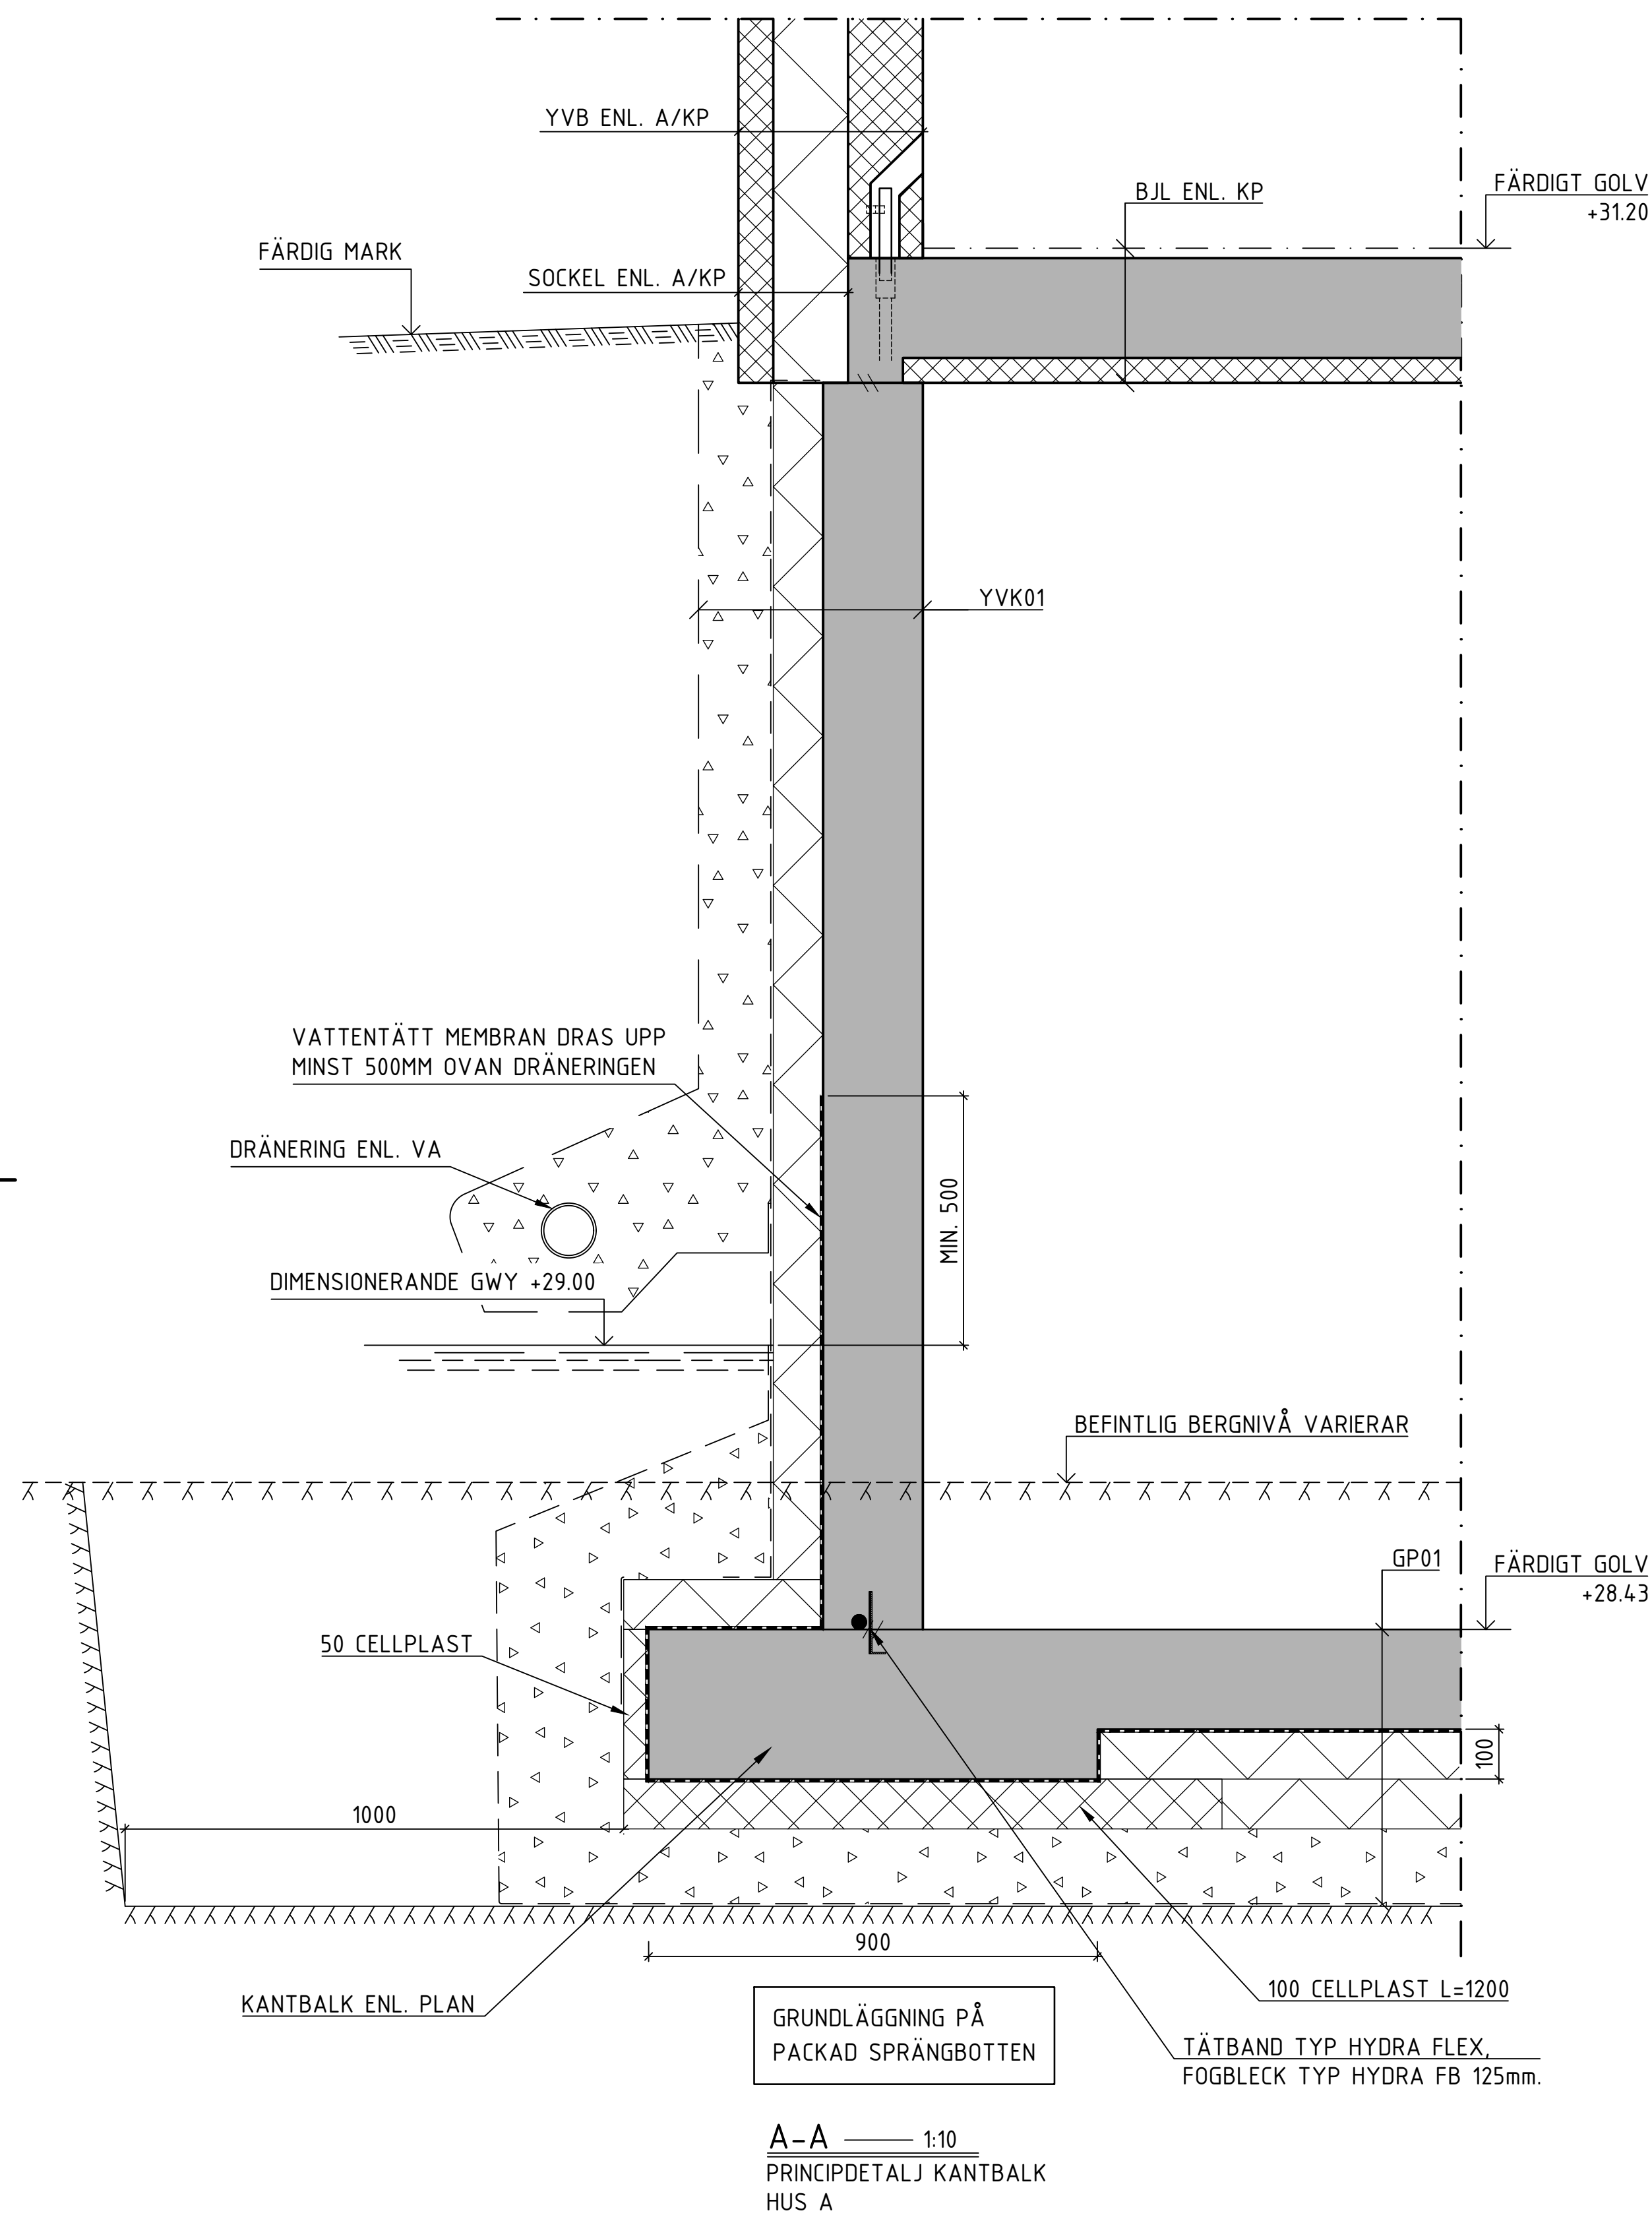

SKALA 1:10

0 0,1 0,2 0,5 1,0

METER

FÖRKLARINGAR

GP = GRUNDPLATTA, SE K-15-6-10

FÖRESKRIFTER

SE RITNING

K-00-0-00

HÄNVISNINGAR

FÖRESKRIFTER	K-00-0-0
--------------	----------


PRINCIPDETALJER INKL. TYPDETALJER
K-15-6-10

Bet.	Ändringen avser	Datum	Sign
------	-----------------	-------	------

SYSTEMHANDLING



 Ministerium für Bildung und Wissenschaft Land Nordrhein-Westfalen	Orientierungsfigur
--	------------------------------------

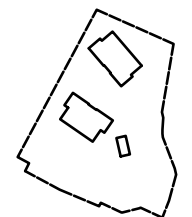

	E	ELKONSULT E-TEC AB	073-6655510
	G	TREELINE CONSULTING AB	073-0844329
X	K	KÄVÉR & MELLIN	072-7326731
	L	C.F. MÖLLER SVERIGE AB	08-55567600
	M	VIKEN MILJÖKONSULT AB	070-6526445
	V	DLV AB	076-0224797
	VA	NIRAS SWEDEN AB	08-50384400

Uppdrag.nr. 24222	Ritad/konstr. av FE	Handläggare FE
----------------------	------------------------	-------------------

Datum	Ansvarig
2024-11-29	ANDERS HEDBERG

SKEVIK, VÄRMDÖ

SKEVIK 1:190

Principdetaljer

Skala a1	Skala a3	Nummer	Bet.
1:10	1:20	K-15-6-11	