


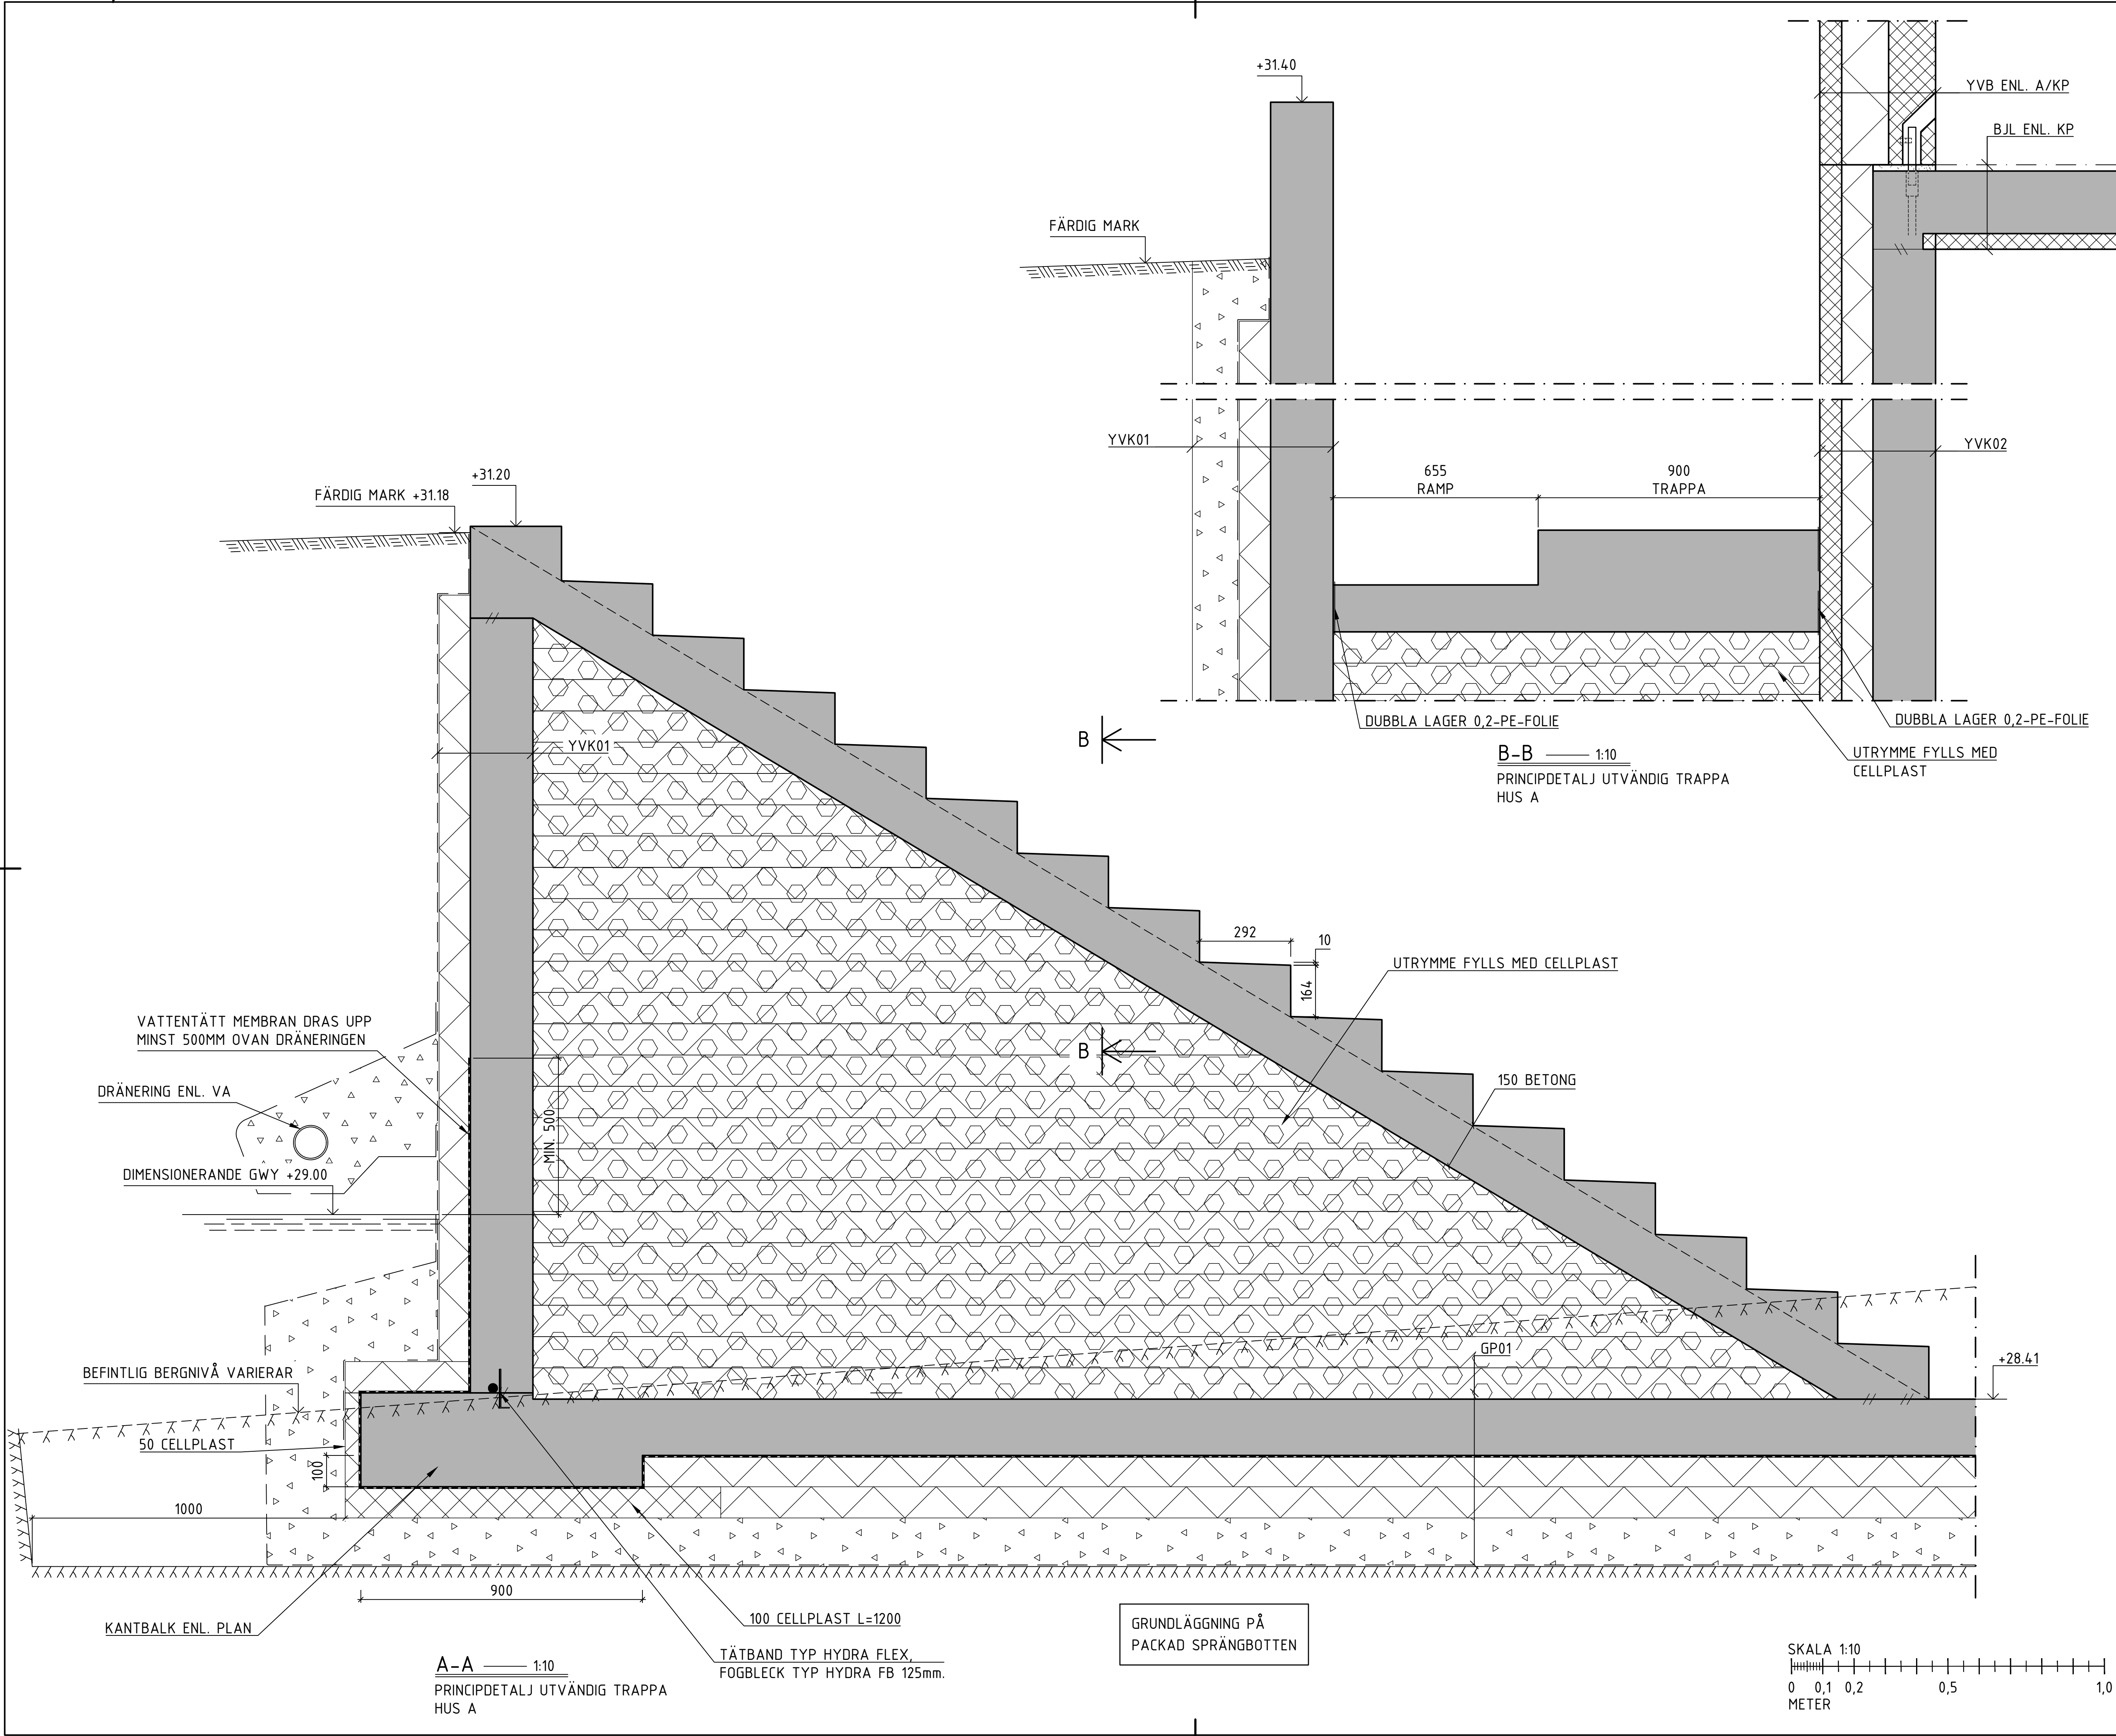

FÖRKLARINGAR

GP = GRUNDPLATTA, SE K-15-6-10

FÖRESKRIFTER

SE RITNING

K-00-0-00

HÄNVISNINGAR

FÖRESKRIFTER

PRINCIPDETALJER INKL. TYPDETALJER

K-00-0-00

K-15-6-10

Bef.	Andringen avser	Datum	Sign
SYSTEMHANDLING			
Orienteringsfigur			
E	ELKONSULT E-TEC AB	073-6655510	
G	TREELINE CONSULTING AB	073-0844329	
K	KÄVER & MELLIN	072-7326731	
L	C.F. MØLLER SVERIGE AB	08-55576000	
M	VIKEN MILJÖKONSULT AB	070-6526445	
V	DLV AB	076-0224797	
VA	NIRAS SWEDEN AB	08-50384400	
Uppdragsnr.	Ritad/konstr. av	Handläggare	
24222	FE	FE	
Datum	Ansv. ing. ANDERS HEDBERG		
2024-11-29			
SKEVIK, VÄRMDÖ			
SKEVIK 1:190			
Utvändig trappa Hus A			
Skala a1	Skala a3	Nummer	Bef.
1:10	1:20	K-15-6-12	