


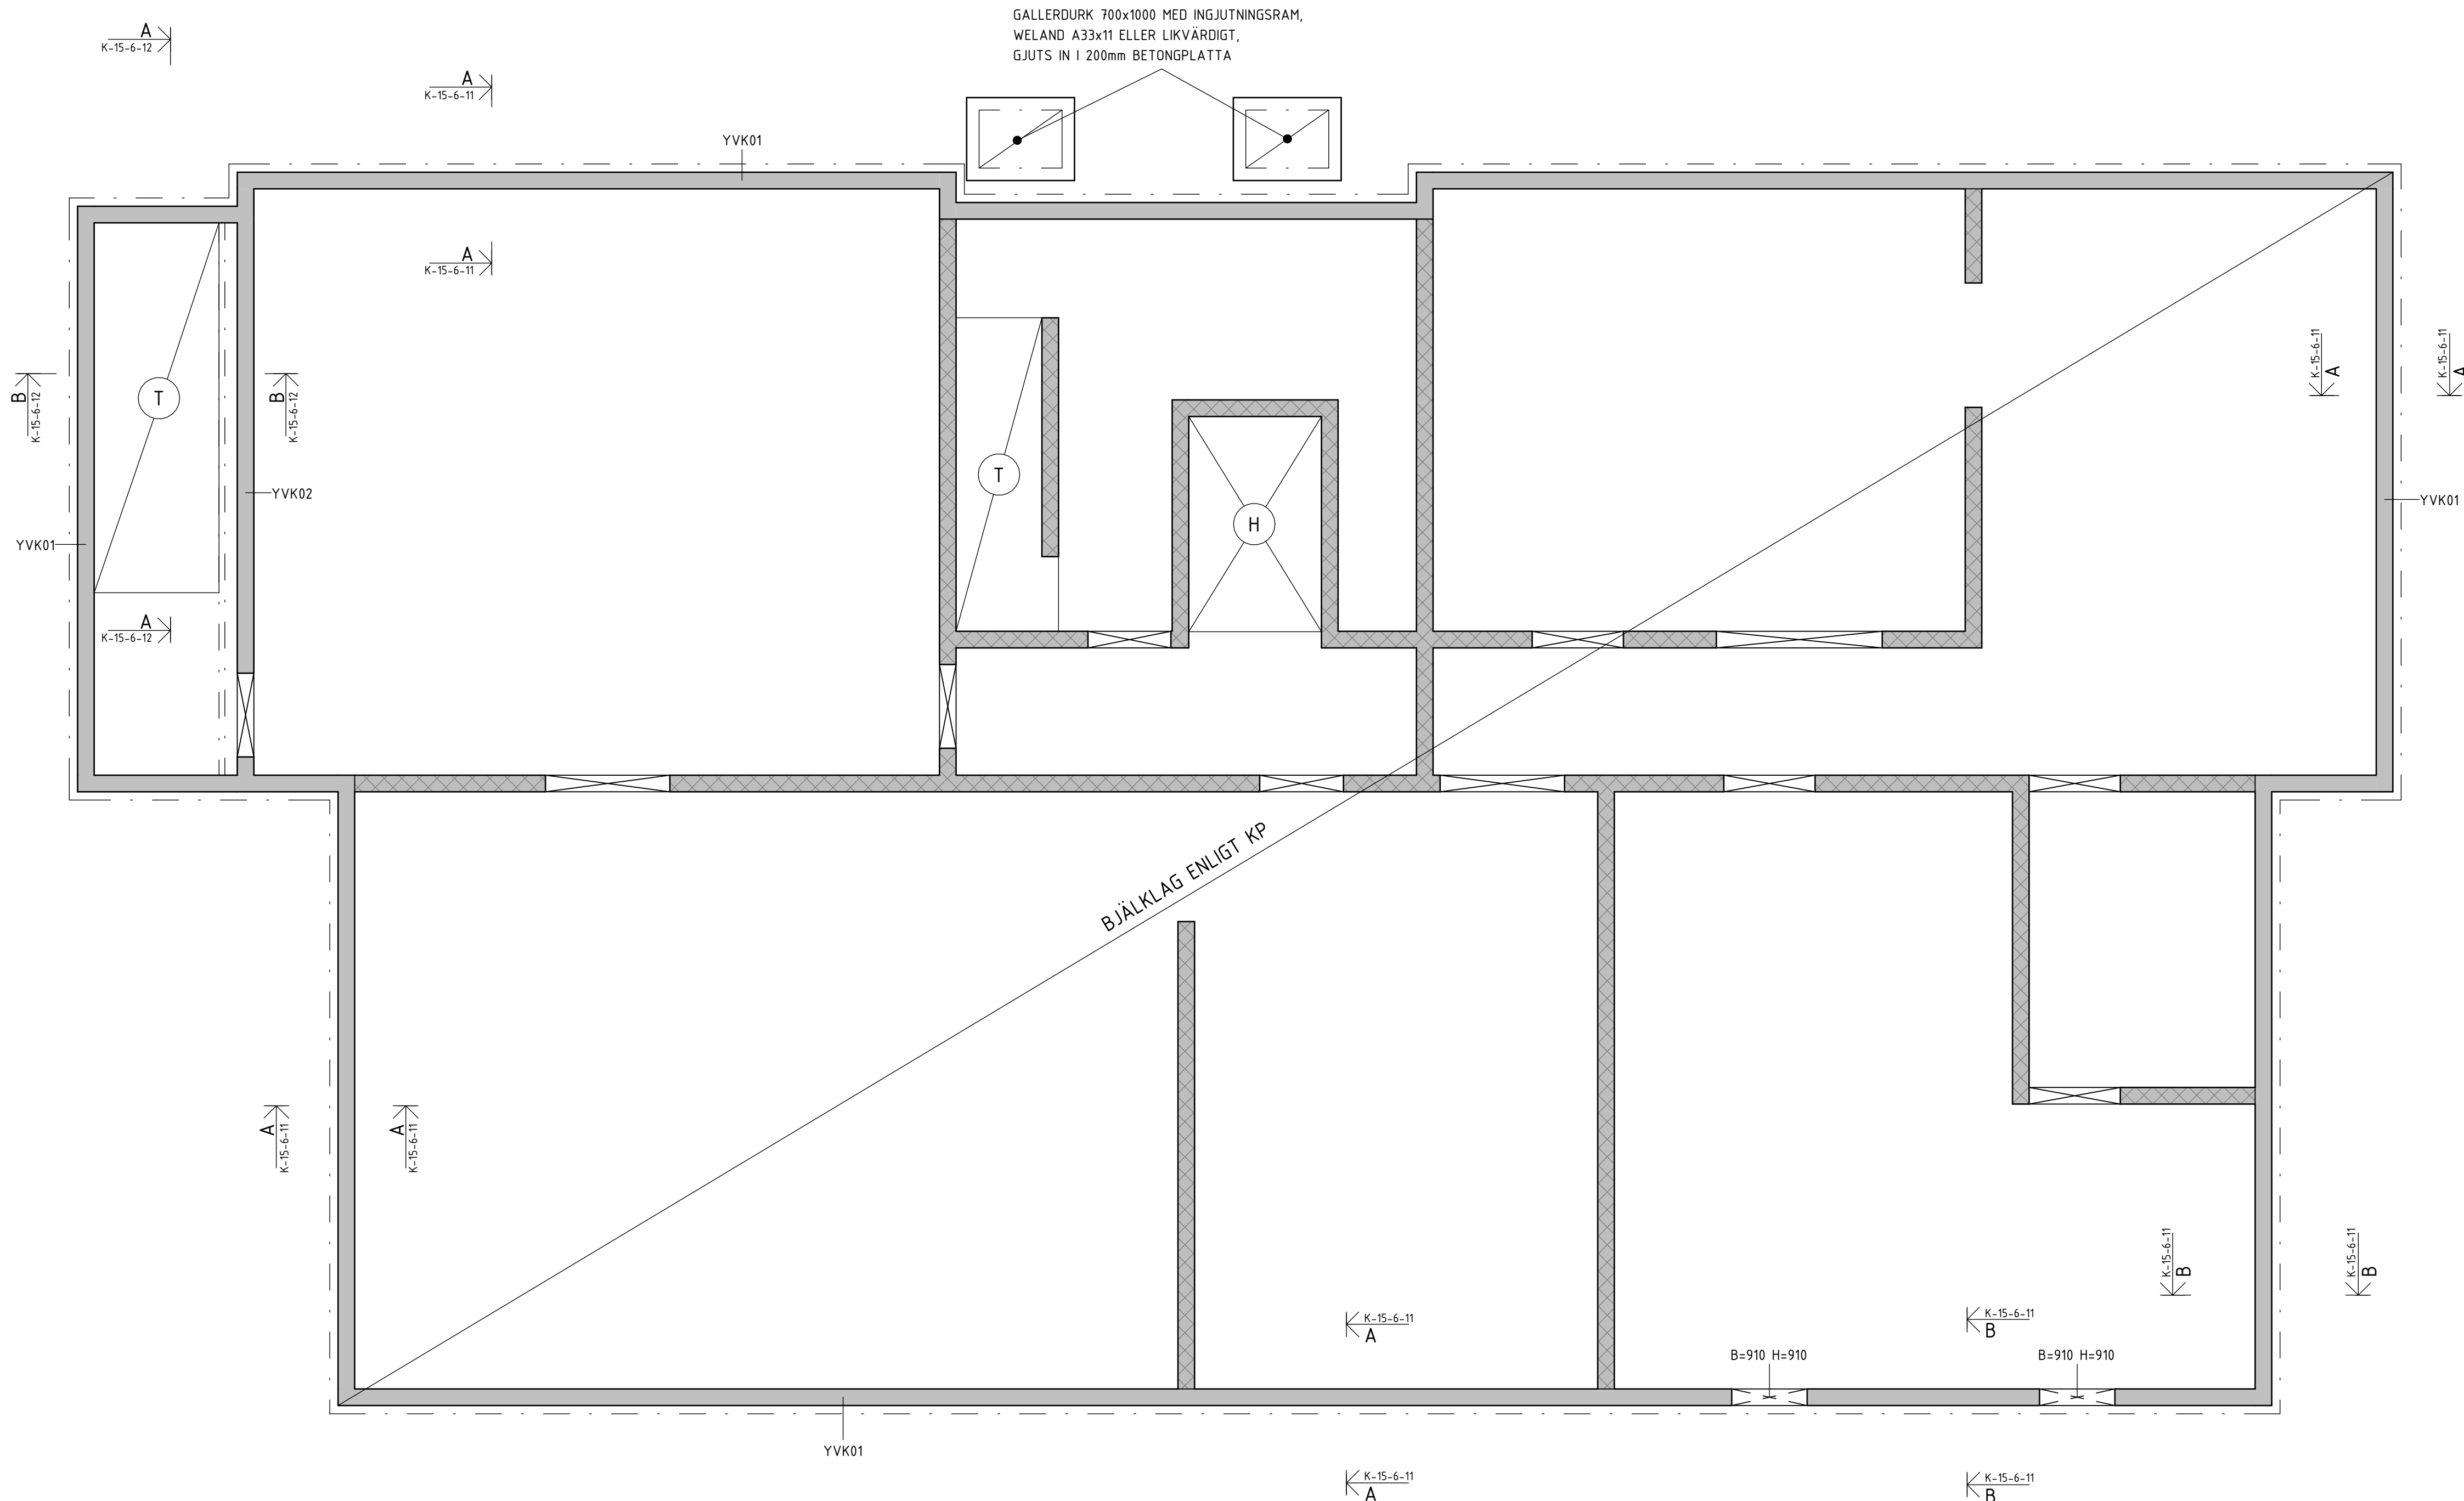

FÖRKLARINGAR

YVK = KÄLLARYTTERTVÄGG, SE K-15-6-10

 = IVB ENLIGT KP

H = HISSCHAKT

T = TRAPPSCHAKT

INSTALLATIONSSCHAKT ENLIGT A/KP

FÖRESKRIFTER

SE RITNING

K-00-0-00

HÄNVISNINGAR

FÖRESKRIFTER

K-00-0-00

PRINCIPDETALJER INKL. TYPDETALJER

K-15-6-10

PRINCIPDETALJER

K-15-6-11

UTVÄNDIG TRAPPA


K-15-6-12

Bef.	Ändringen avser	Datum	Sign
------	-----------------	-------	------

SYSTEMHANDLING



Orienteringsfigur

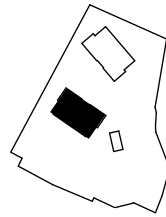

E	ELKONSULT E-TEC AB	073-6655510
G	TREELINE CONSULTING AB	073-0844329
K	KÅVER & MELLIN	072-7326731
L	C.F. MØLLER SVERIGE AB	08-55576000
M	VIKEN MILJÖKONSULT AB	070-6526445
V	DLV AB	076-0224797
VA	NIRAS SWEDEN AB	08-50384400


Uppdragsnr. 24222	Ritad/konstr. av FE	Handläggare FE
Datum 2024-11-29	Ansvarig ANDERS HEDBERG	

SKEVIK, VÄRMDÖ
SKEVIK 1:190

Bjälklag över plan 09 Hus A

Skala a1 1:50	Skala a3 1:100	Nummer K-20-1-109	Bef.
------------------	-------------------	----------------------	------

SKALA 1:50

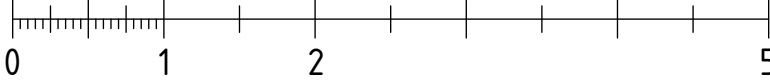

METER