


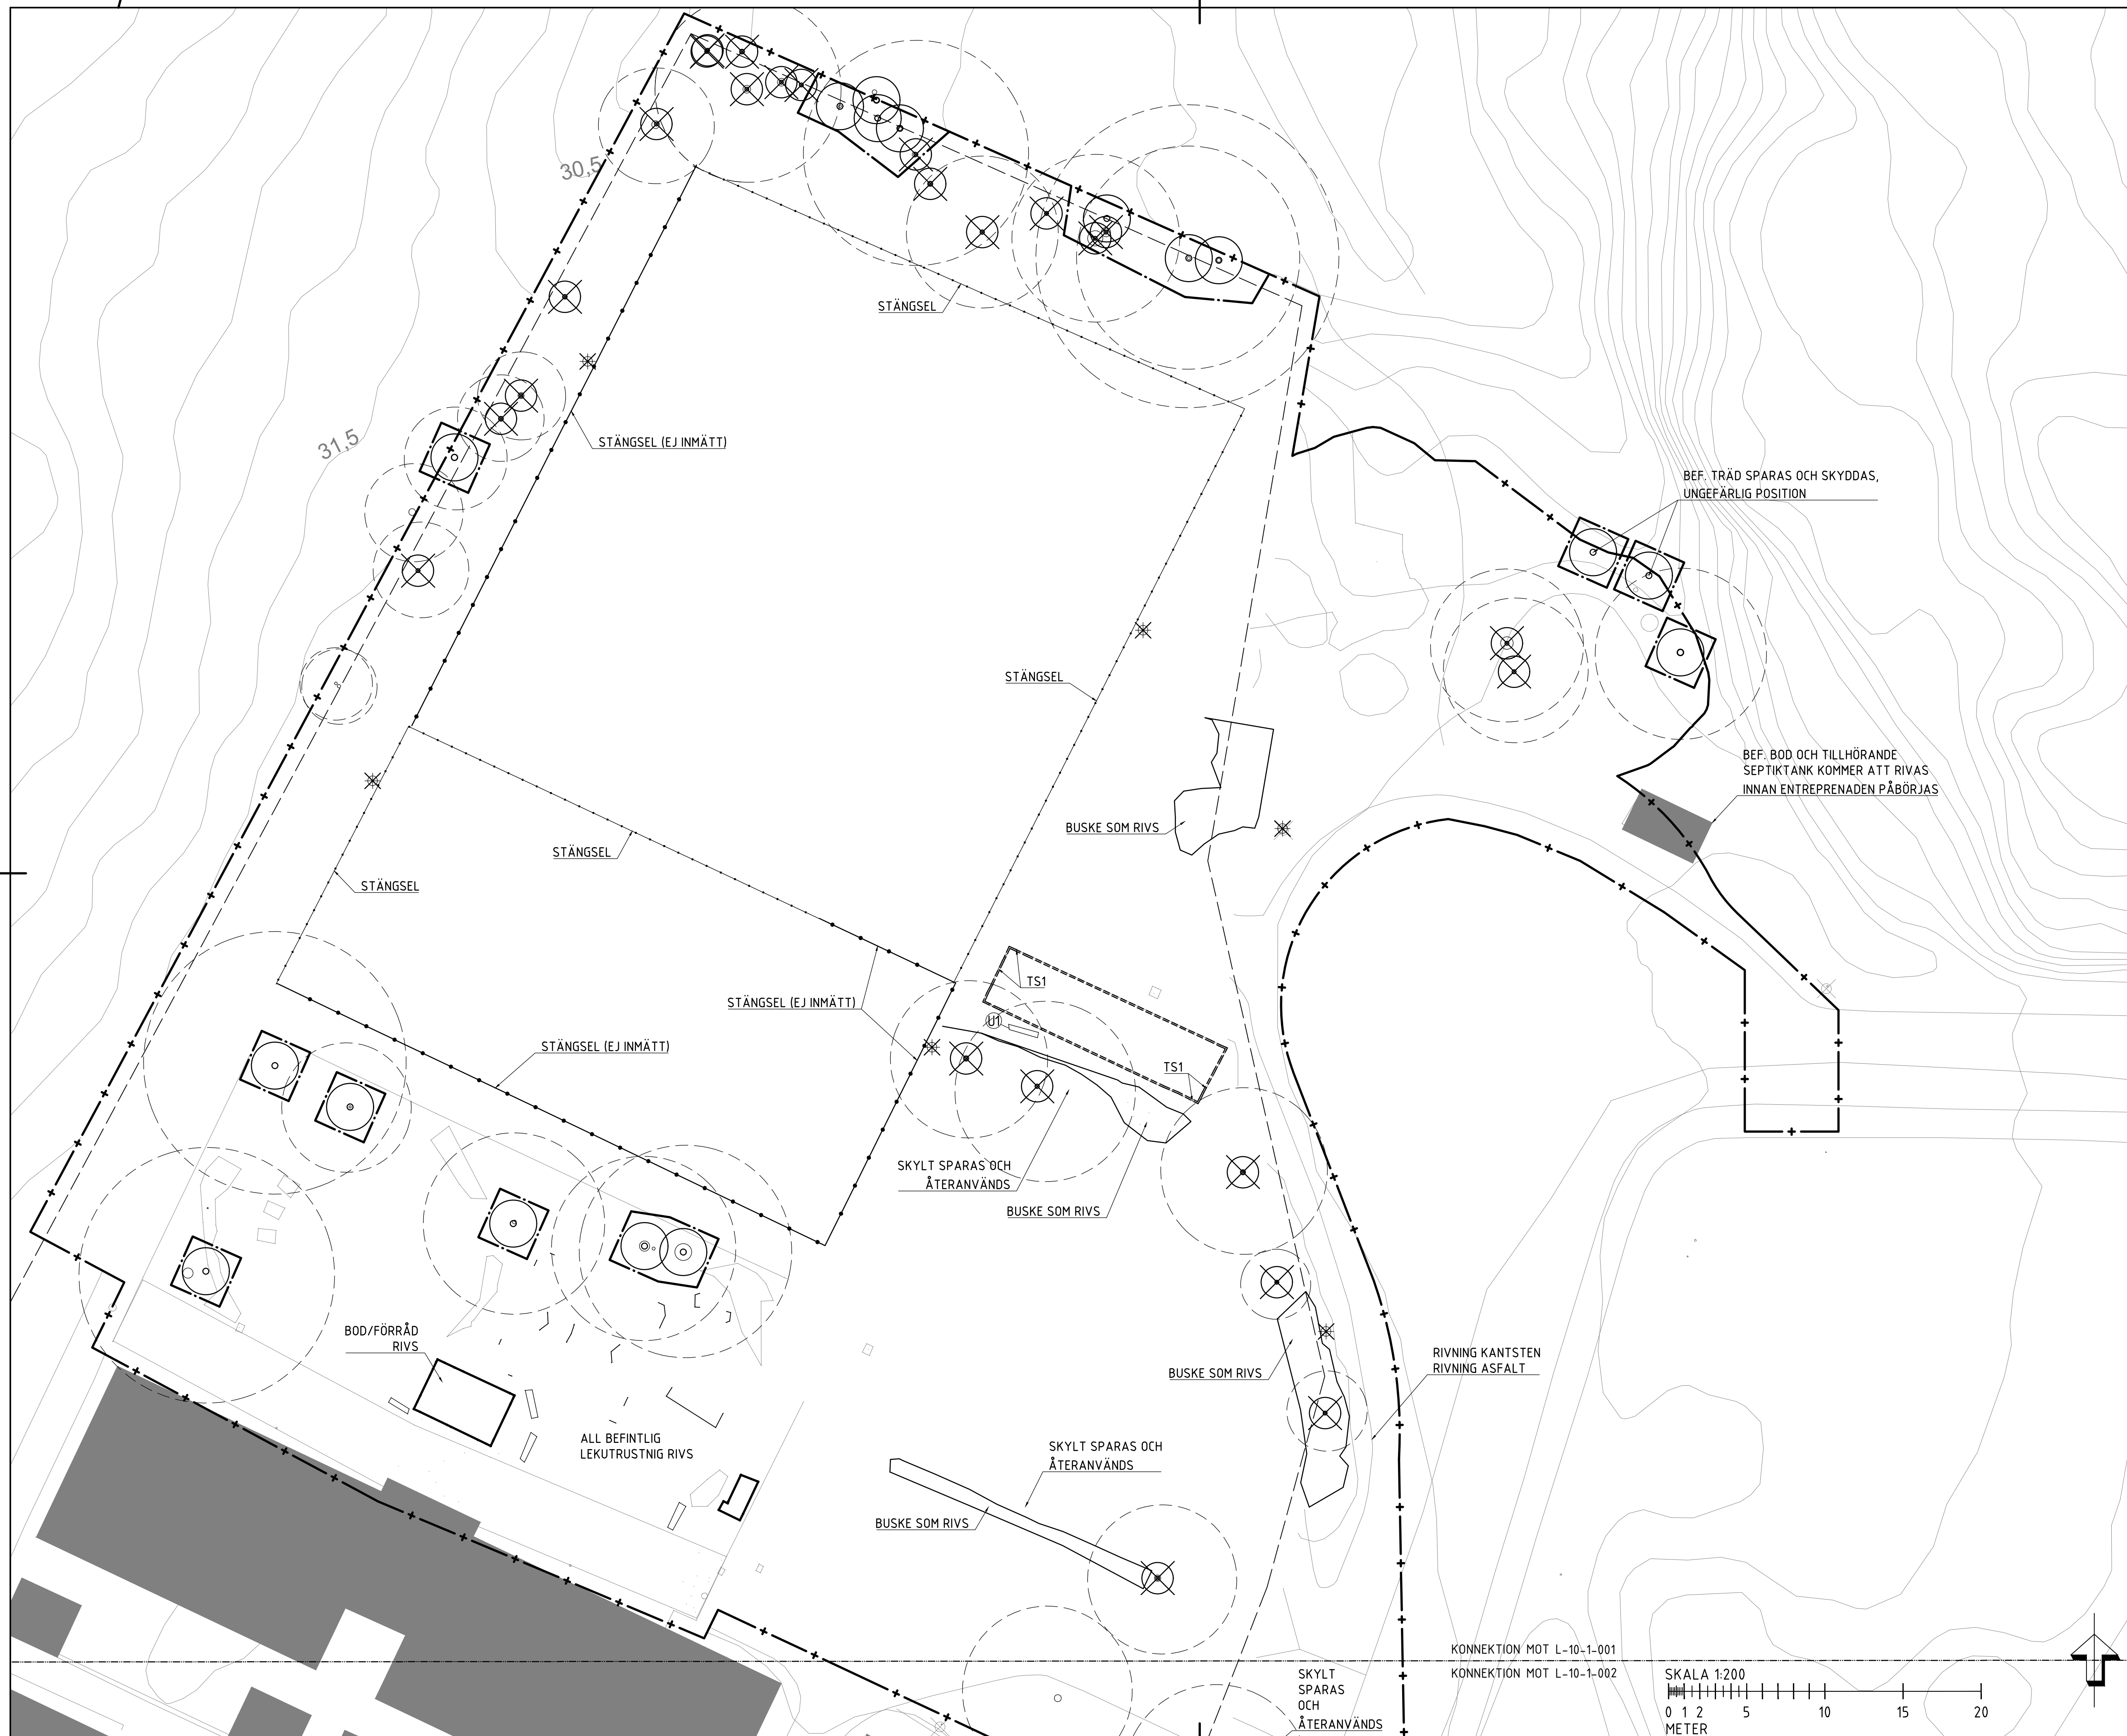

TECKENFÖRKLARING

KOORDINATSYSTEM: SWREF 99 18 00
 HÖJDSYSTEM: RH 2000

- | | |
|---|--|
|  | ARBETSRUMSÄRSGRÄNS RITAD 1 M UTANFÖR
VERKLIG GRÄNS |
|  | FASTIGHETSGRÄNS |
|  | KONNEKTIONSLINJE |
|  | BEFINTLIG TRÄD |
|  | BEFINTLIG TRÄD SOM RIVS |
|  | BEFINTLIG TRÄD SOM BEVARAS OCH SKYDDAS
MED INHÄGNAD UNDER BYGGTIDEN |
|  | INMÄTT TRÄDKRONA/DROPPZON |
|  | BEFINTLIGA BELYSNINGSSTOLPAR INOM
TILLTÄNKT NY GÅRDSMILJÖ RIVS. BEFINTLIGA
BELYSNINGSSTOLPAR MOT BJÖRNSKOGSVÄGEN
DEMONTERAS, KABEL RIVS, FUNDAMENT RIVS
OCH ERSÄTTS MED NYTT OCH STOLPAR
ÅTERMONTERAS, ENLIGT E-HANDLING. |
|  | STÄNGSEL STÄNGSEL SOM DEMONTERAS |
|  | TRÄSÄRG SOM DEMONTERAS |
|  | BANK SOM DEMONTERAS |

Bet.	Ändringen avser	Datum	Sign.
------	-----------------	-------	-------

SYSTEMHANDLING



Orientierungsfiguren



	E	ELKONSULT E-TEC AB	073-6655510
	G	TREELINE CONSULTING AB	073-0844329
	K	KÅVER & MELLIN	072-7326731
X	L	C.F. MÖLLER SVERIGE AB	08-55576000
	M	VIKEN MILJÖKONSULT AB	070-6526445
	V	DLV AB	076-0224797
	VA	NIRAS SWEDEN AB	08-50384400

Uppdrag nr:	Ritad/konstr. av	Handläggare
60764	KTN	KARL TYRVÄINNE
Datum	Ansvarig	
2024-11-29	SELMA BROSTRÖM	

SKEVIK, VÄRMDÖ
SKEVIK 1:190
FINPLANERING LANDSKAP
RIVNINGSPLAN DEL 1

Skala a1	Skala a3	Nummer	Be
1:200	1:400	L-10-1-001	