


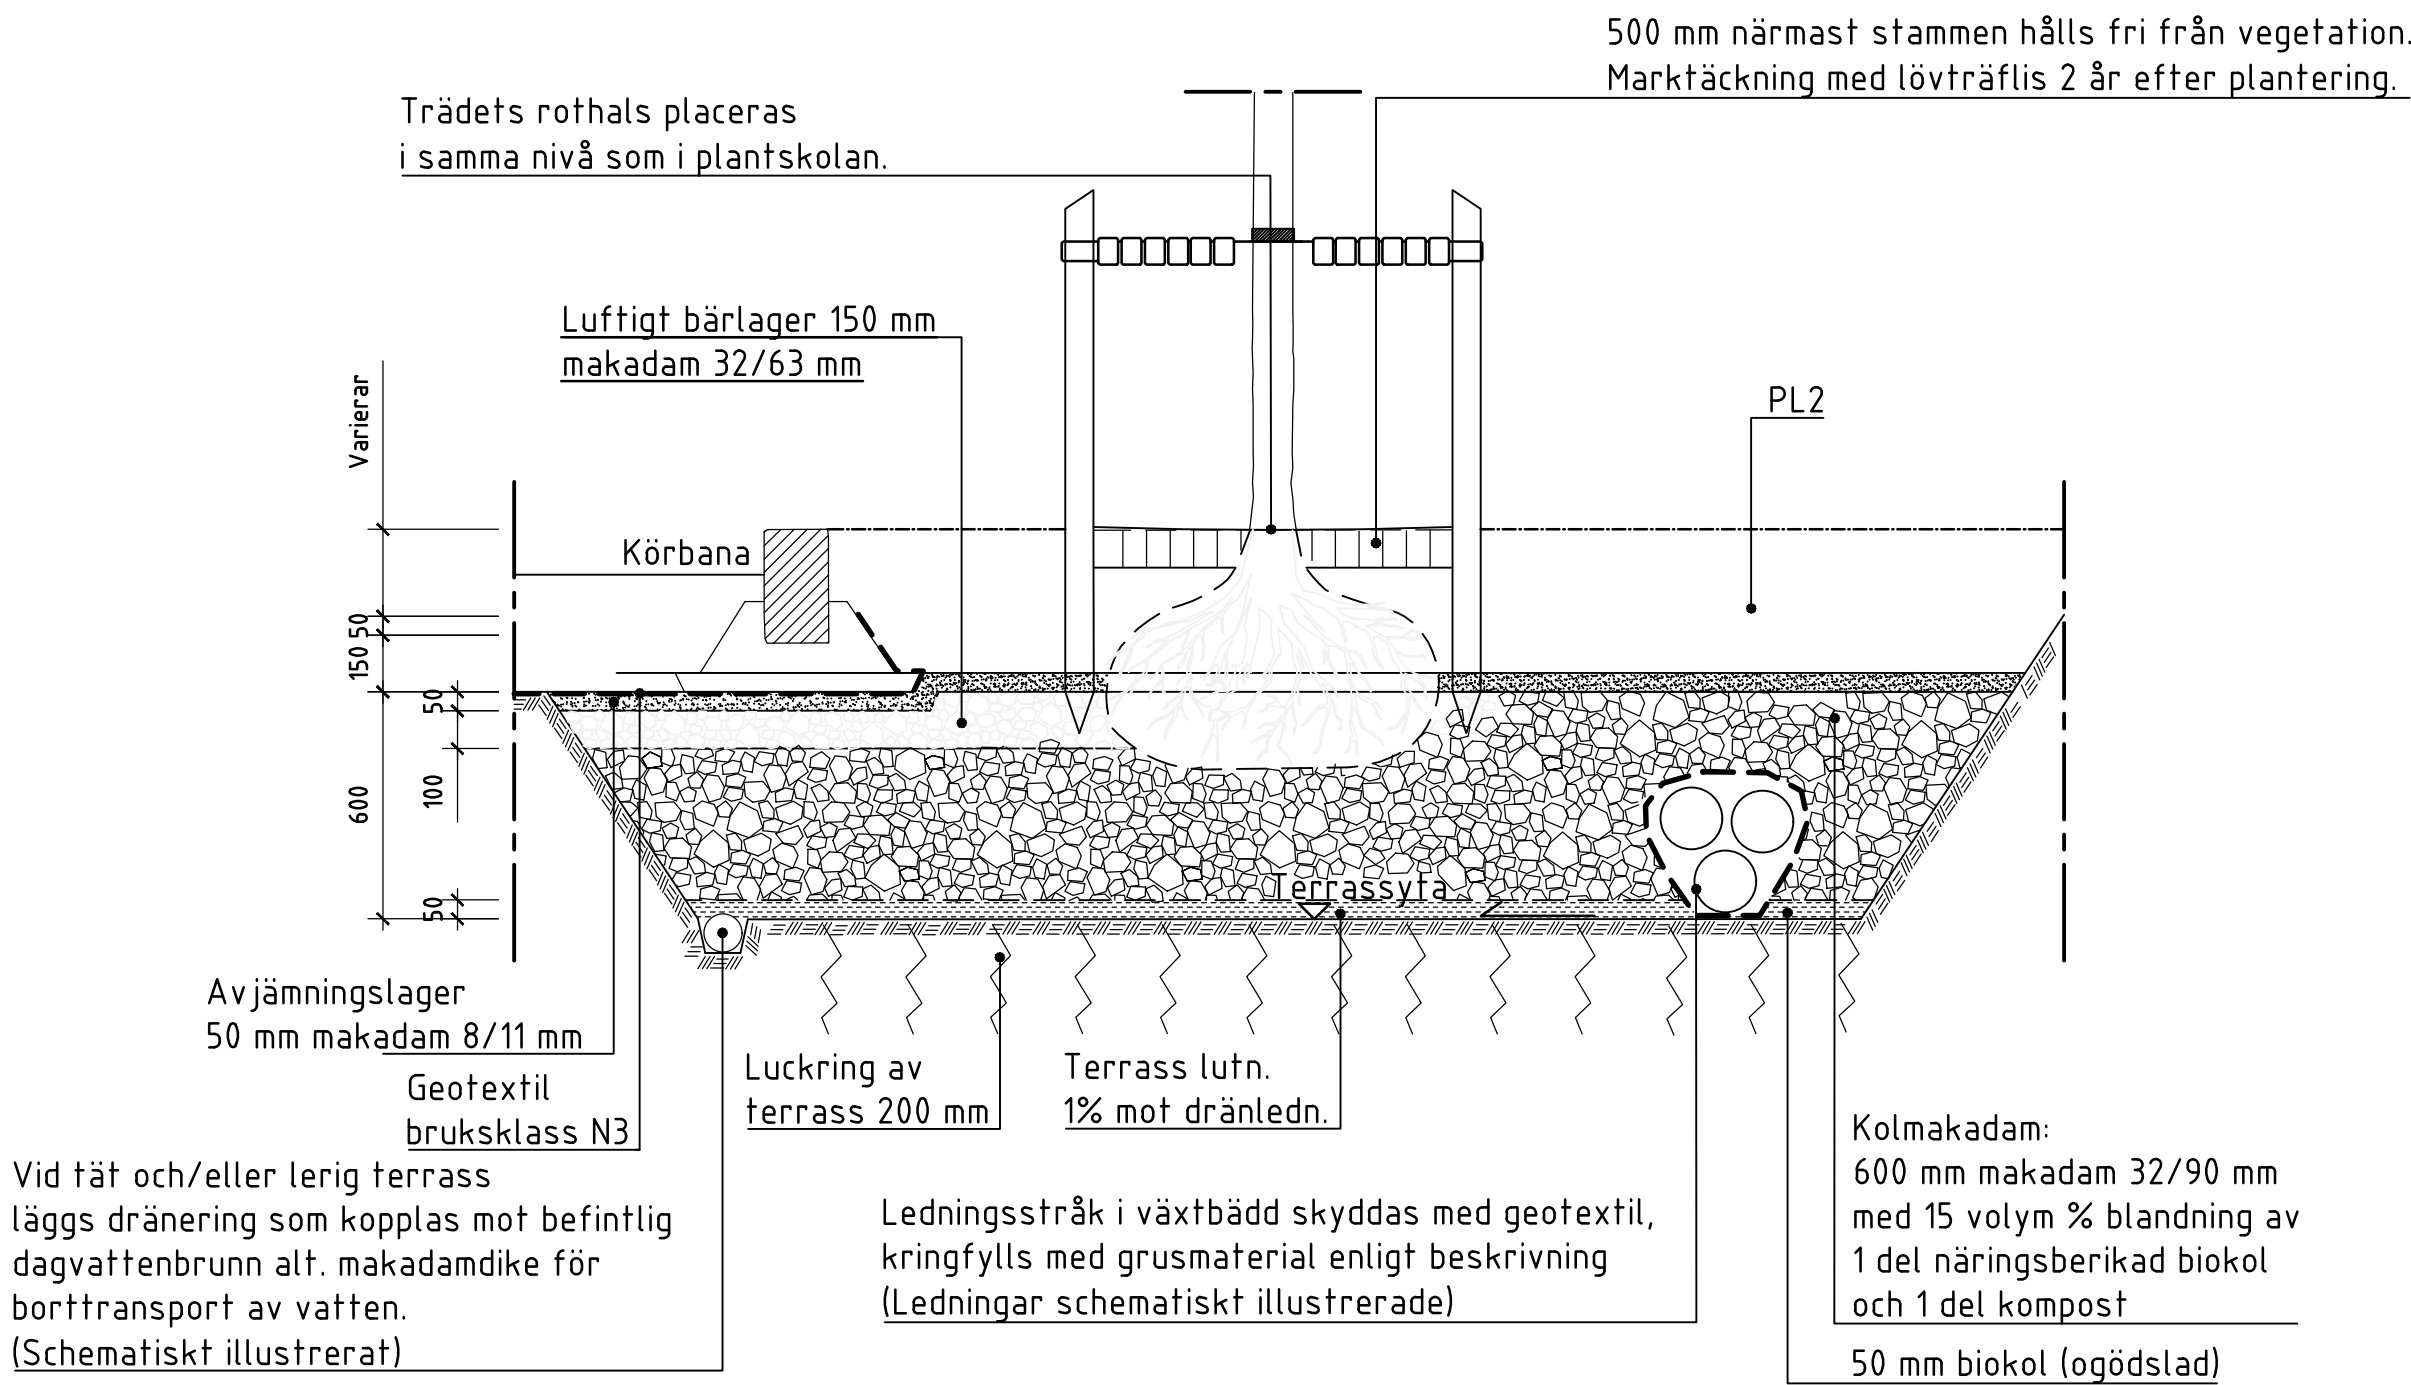


TR1 - TRÄD I HÅRDGJORD YTA MED KOLMAKADAM

PRINCIPSEKTION
SKALA 1:20

ANMÄRKNING

Åtgärder för terrassen anpassas efter dess beskaffenhet. Täta terrassytor kan kräva dränering och allt för genomsläppliga terrasser kan behöva tätas. Luckring utförs om större genomsläpplighet önskas hos en kompakterad terrassyta.

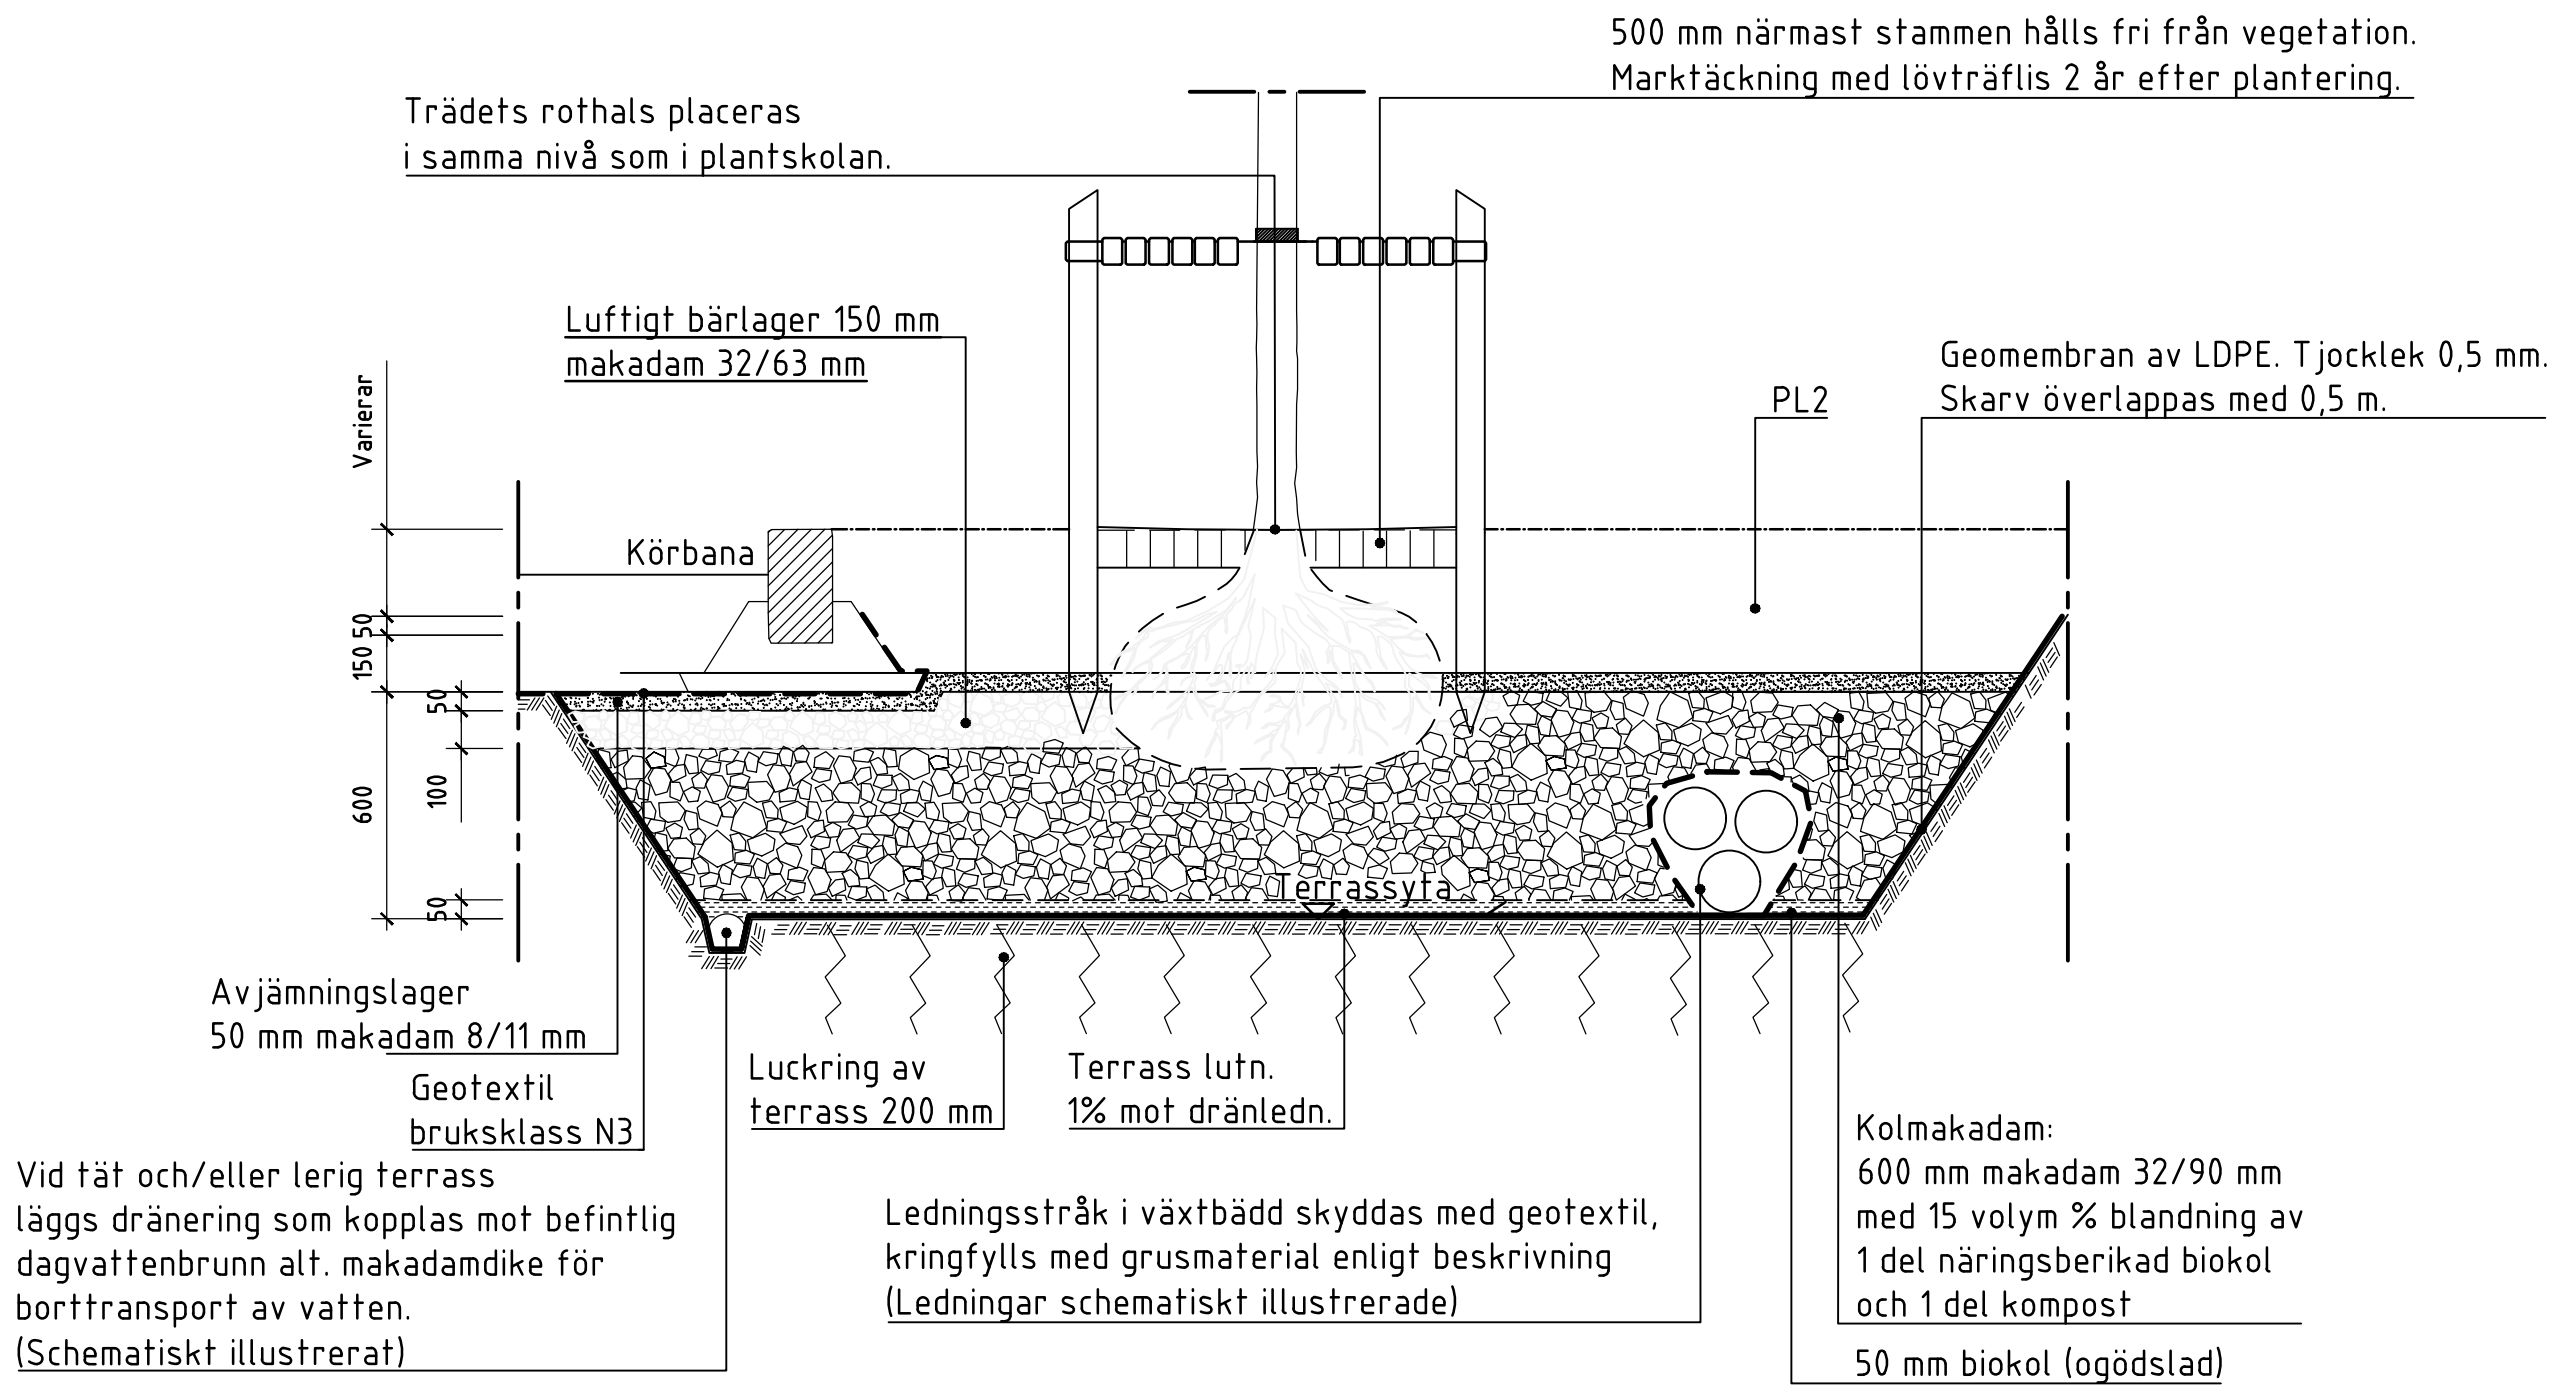


TR3 - TRÄD I HÅRDGJORD YTA MED KOLMAKADAM, TÄT BOTTEN

PRINCIPSEKTION
SKALA 1:20

ANMÄRKNING


Åtgärder för terrassen anpassas efter dess beskaffenhet. Täta terrassytor kan kräva dränering och allt för genomsläppliga terrasser kan behöva tätas. Luckring utförs om större genomsläpplighet önskas hos en kompakterad terrassyta.

Schaktbotten inkl. sidor av skelettjorden täcks med geomembran då terrassen anses vara för genomsläpplig.

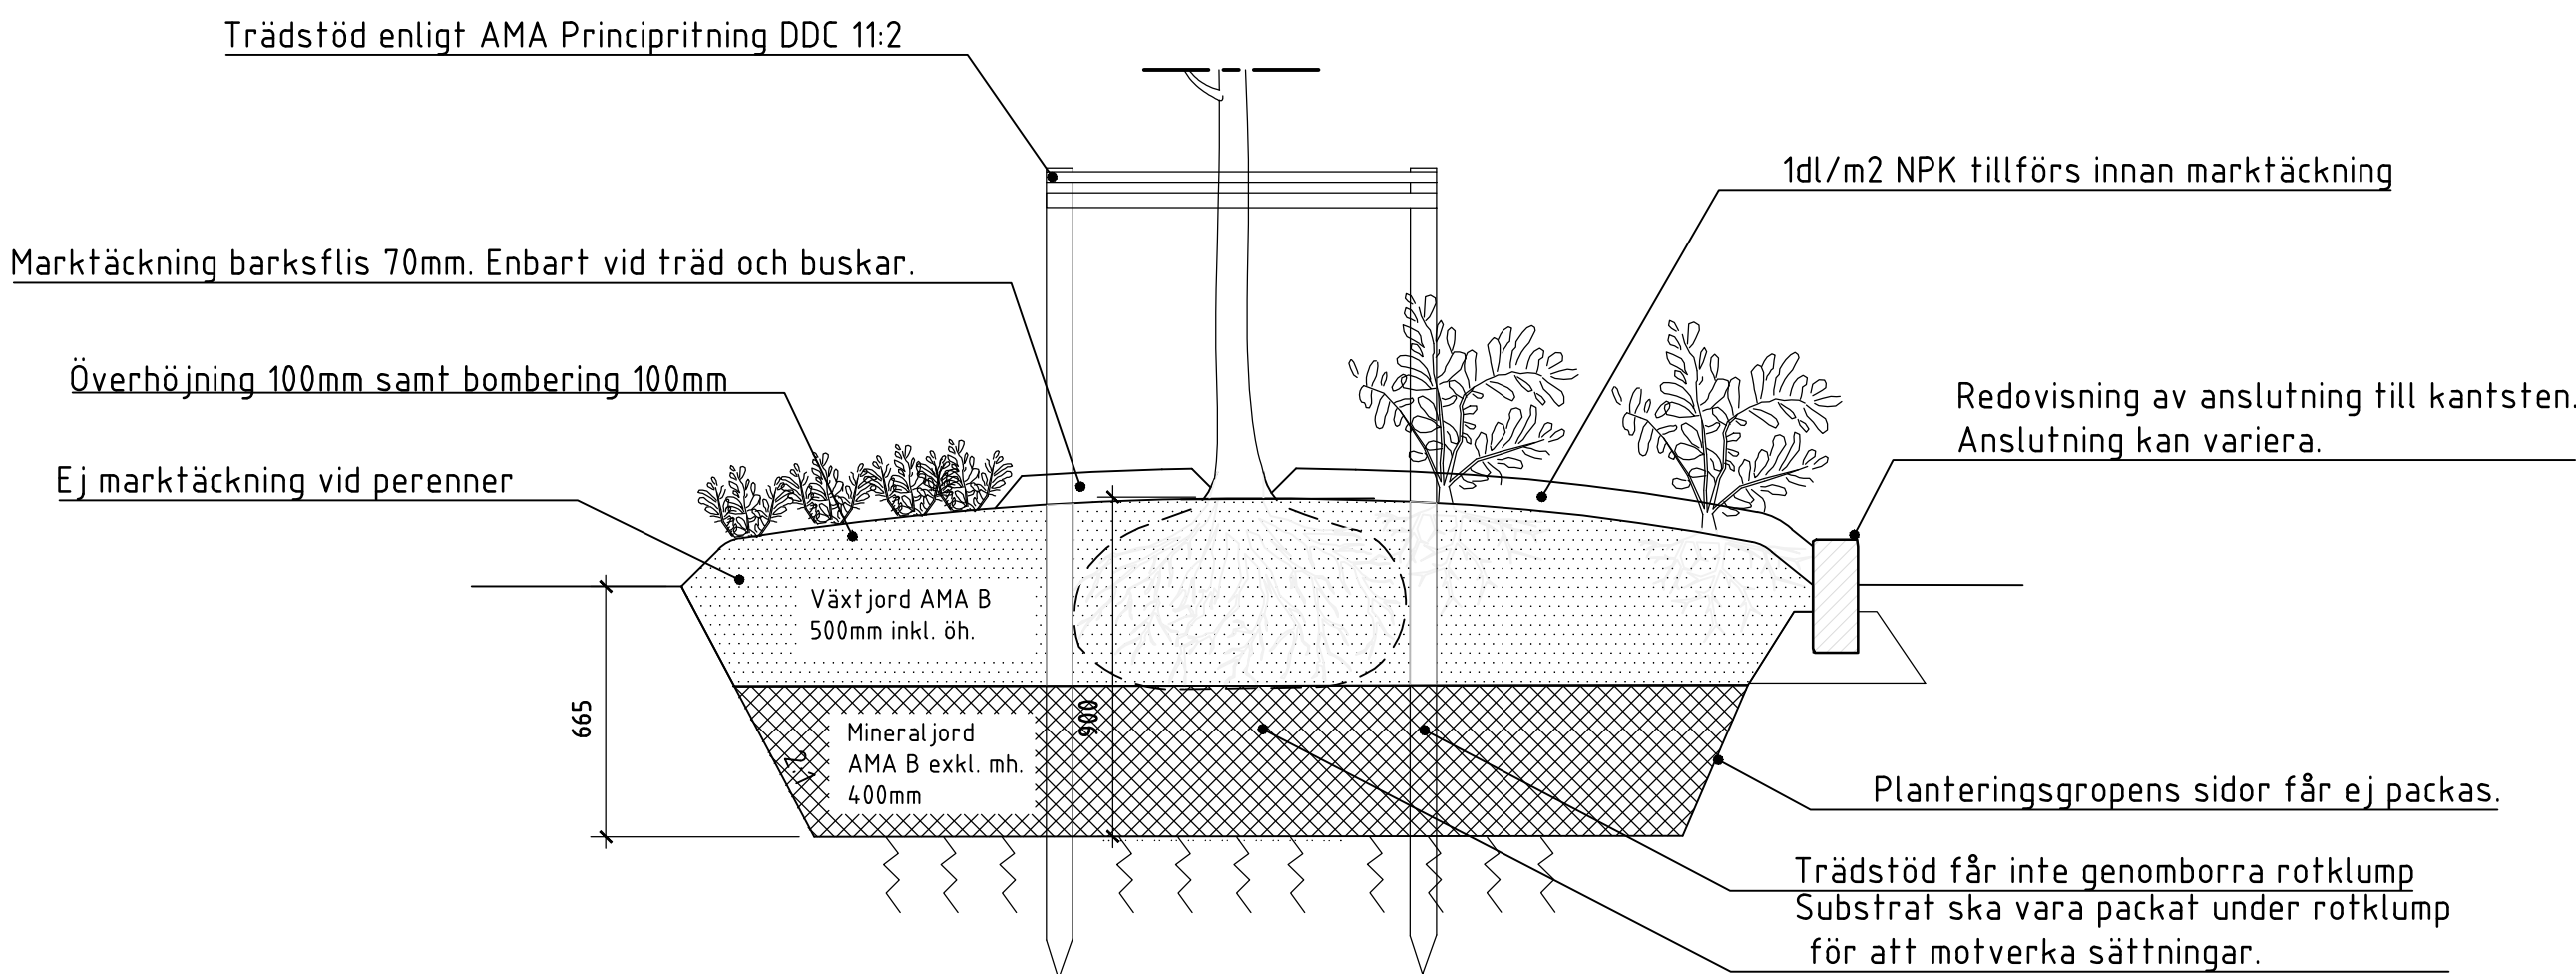

TR2 - TRÄD I VEGETATIONSYTA, NATURLIK MARKPROFIL

PRINCIPSEKTION
SKALA 1:20

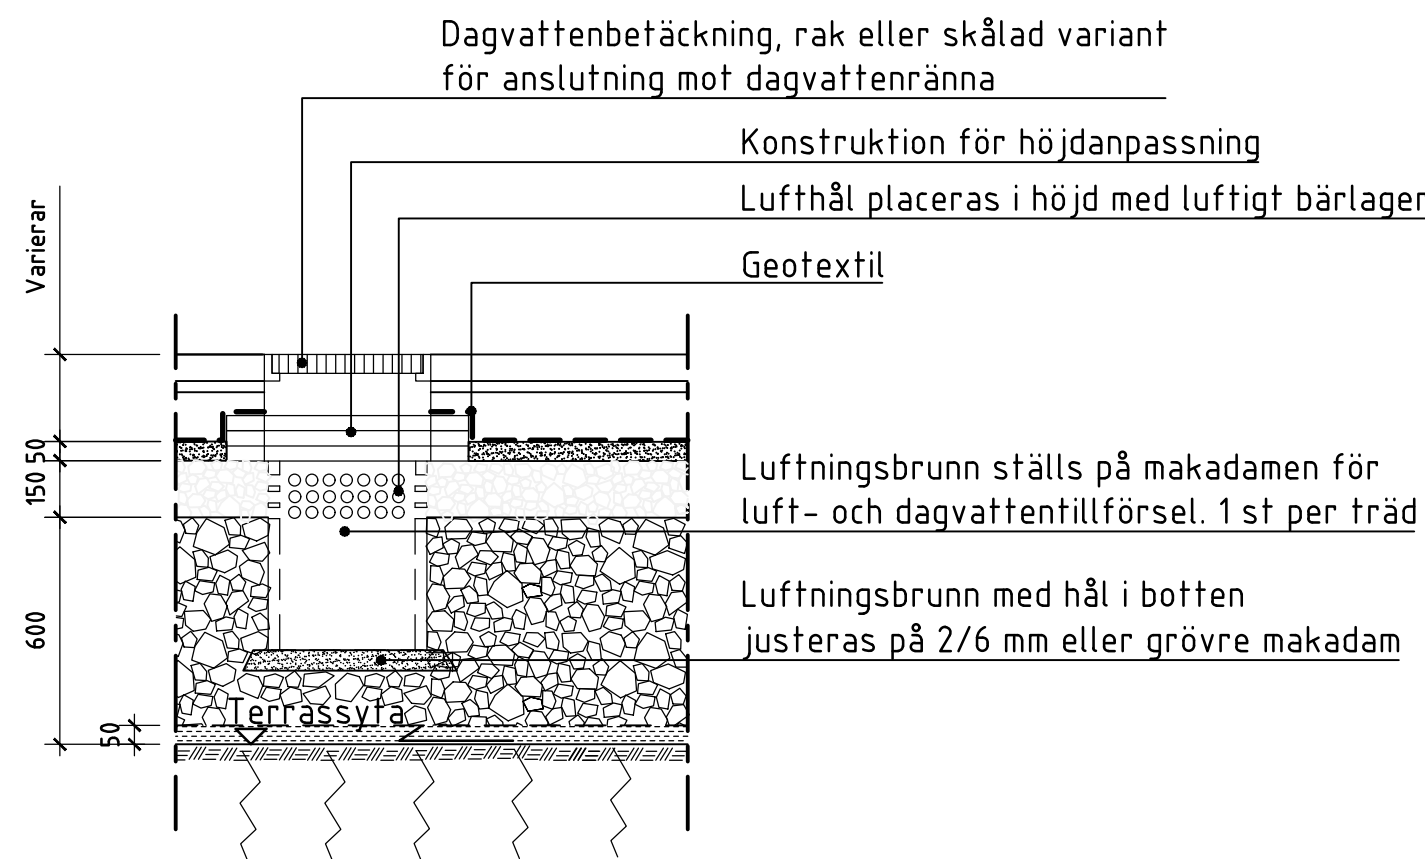


LUFTNINGSBRUNN

PRINCIPSEKTION
SKALA 1:20

ANMÄRKNING

Luftningsbrunn placeras i lågpunkt. Sandfångsvolym 60 liter.

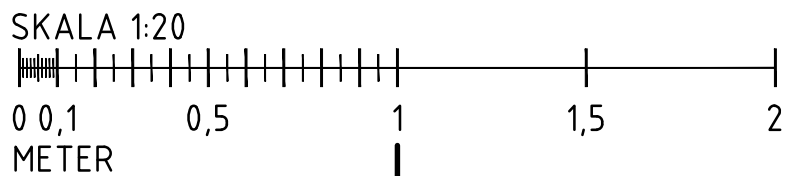

TECKENFÖRKLARING

ALLMÄNT:
ALLA MÅTT I MILLIMETER DÄR EJ ANNAT ANGES

HÄNVISNINGAR

UTBREDNING OCH PLACERING BRUNNAR/LEDNINGAR ENLIGT VA/DAGVATTEN.

ANSLUTNING DAGVATTENNÄT ENLIGT VA-HANDLING.

FUNDAMENT OCH LEDNINGSDRAGNING TILL BELYSNING ENLIGT BELYSNING/E-HANDLING

Bet	Ändringen avser	Datum	Sign
-----	-----------------	-------	------

SYSTEMHANDLING



E	ELKONSULT E-TEC AB	073-6655510
G	TREELINE CONSULTING AB	073-0844329
K	KÄVER & MELLIN	072-7326731
L	C.F. MØLLER SVERIGE AB	08-55576000
M	VKEN MILJÖKONSULT AB	070-6526445
V	DLV AB	076-0224797
VA	NIRAS SWEDEN AB	08-50384400
Lupdrag nr. 60764	Ritad/konstr. av KTN	Hundläggare KARL TYRVÄINEN
Datum 2024-11-29	Ansvarig SELMA BROSTRÖM	

SKEVIK, VÄRMDÖ

SKEVIK 1:190

FINPLANERING LANDSKAP

TRÄDGROPAR

Skala a1	Skala a3	Nummer	Bet.
1:20	1:40	L-30-2-002	