


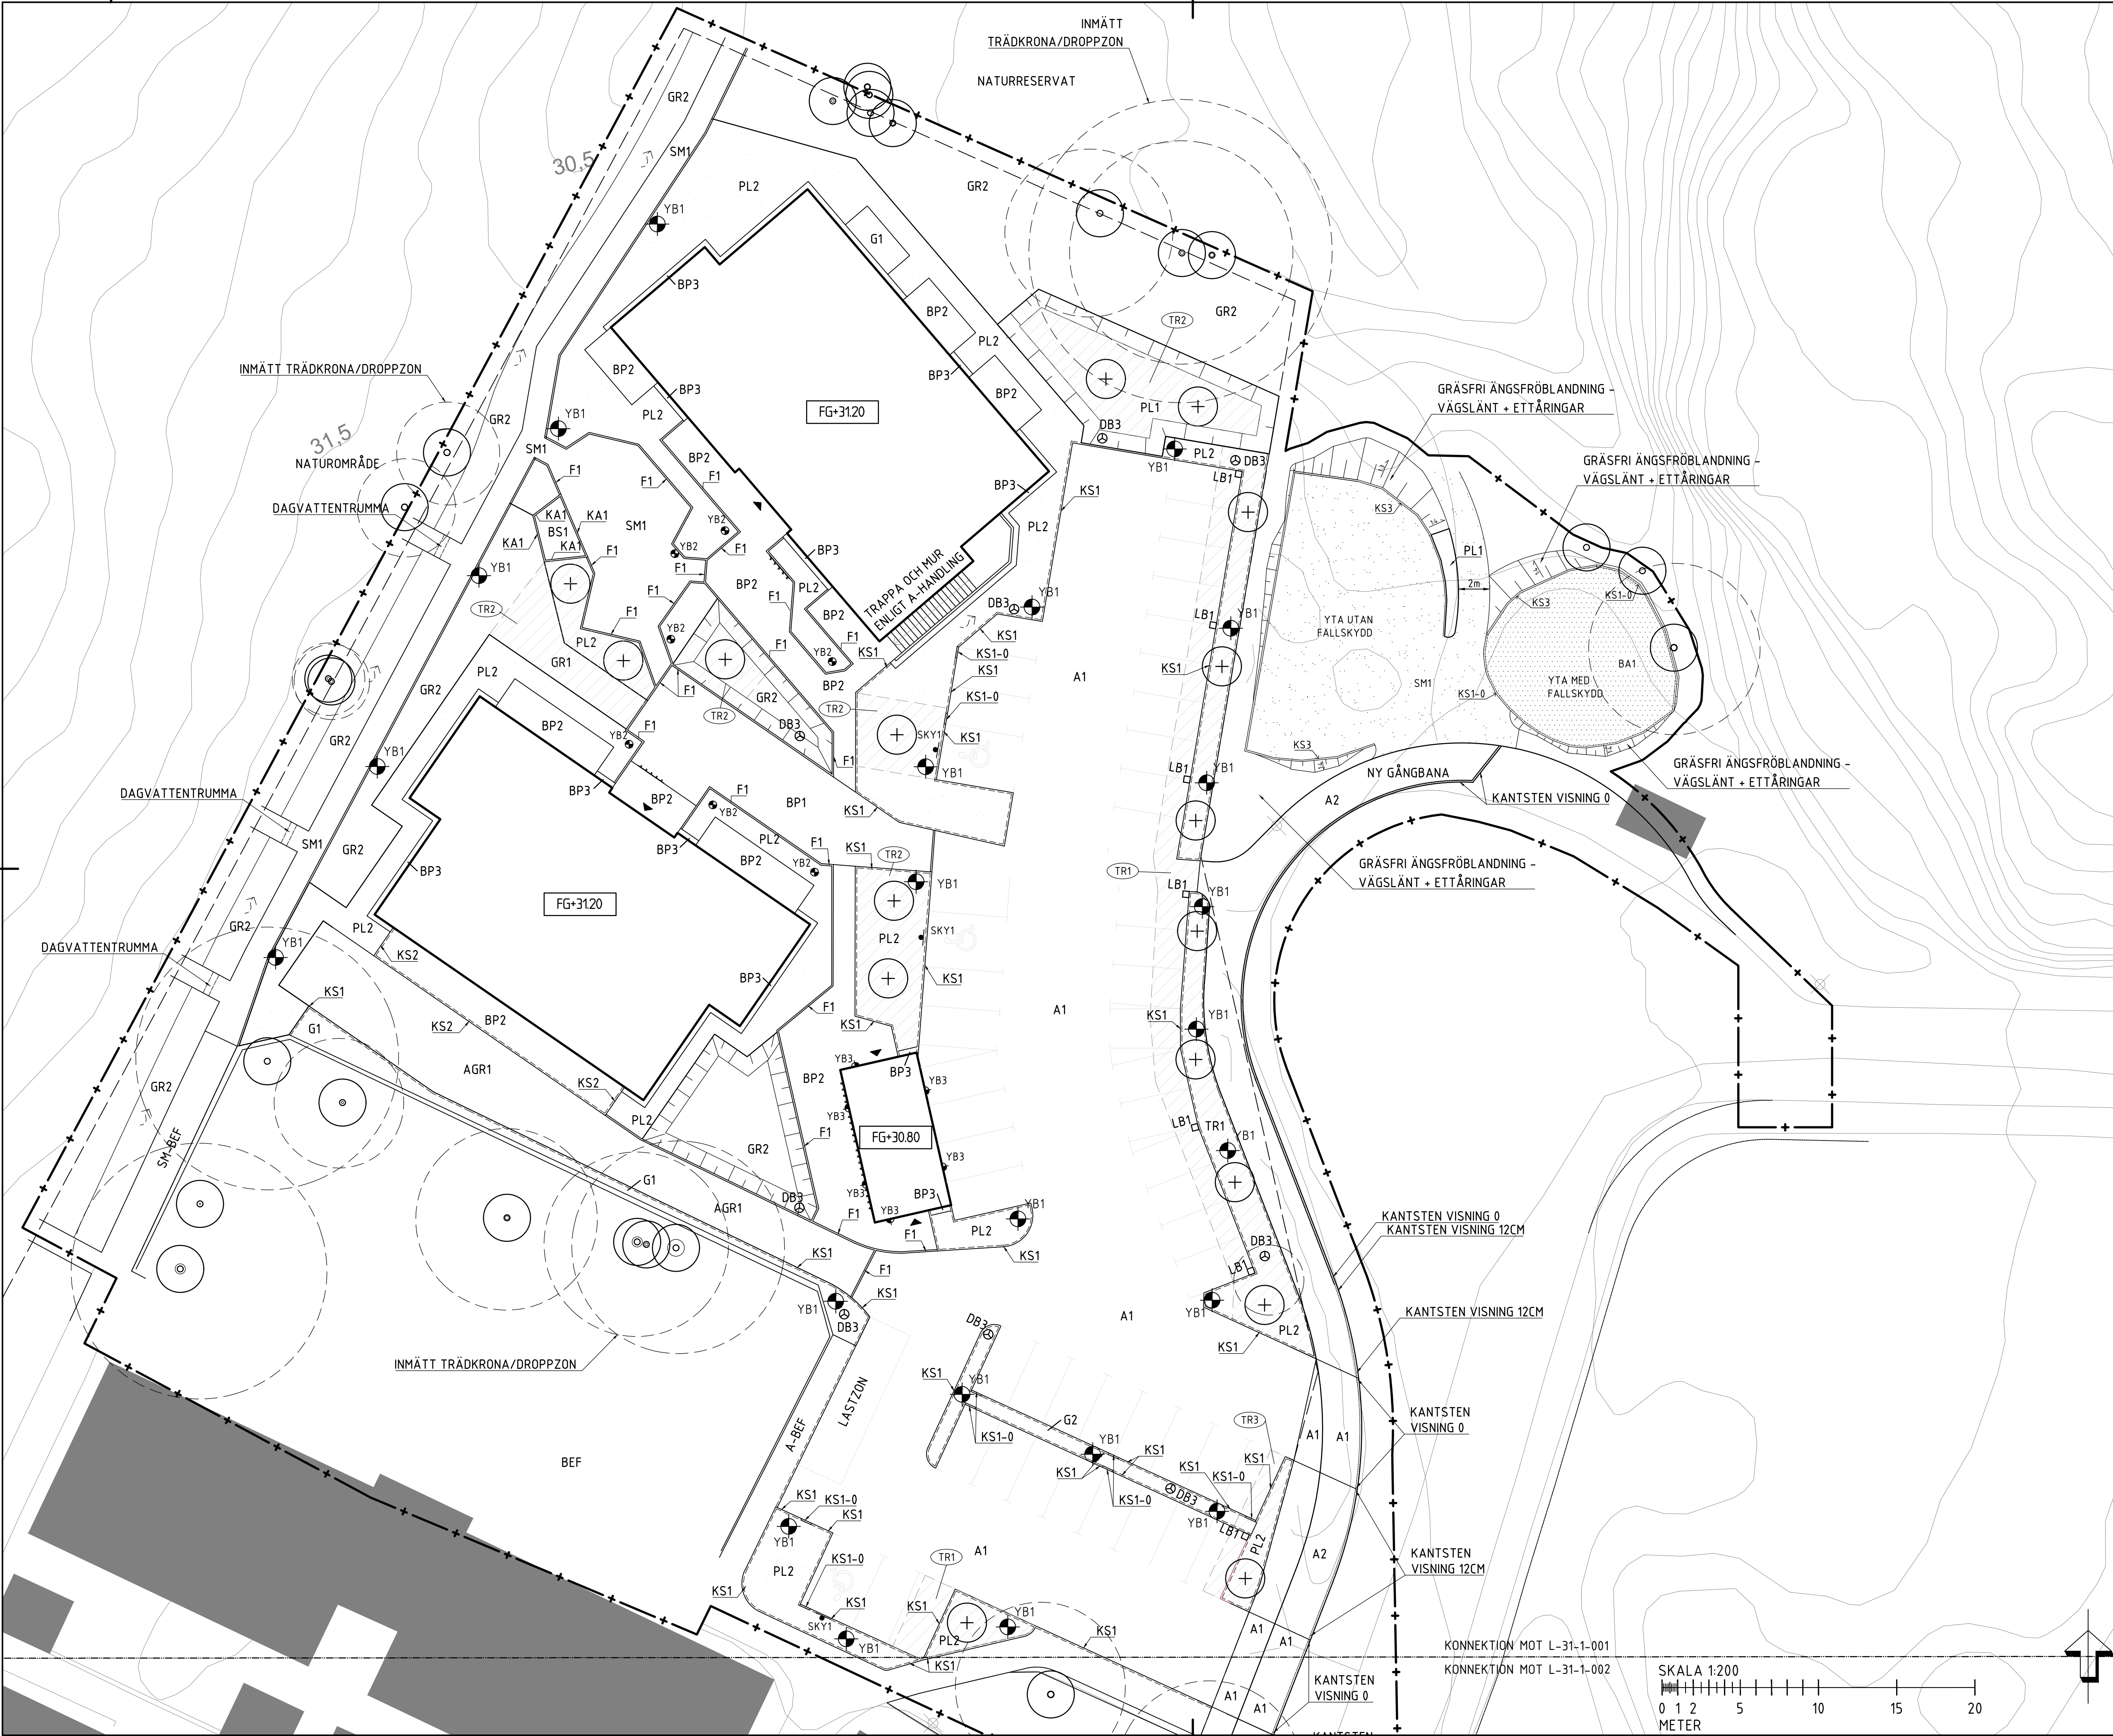

TECKENFÖRKLARING

- KOORDINATSYSTEM: SWEREF 99 18 00
HÖJDSYSTEM: RH 2000
- ARBETSOMRÅDESGRÄNS RITAD 1 M UTANFÖR
 - VERKLIG GRÄNS
 - FASTIGHETSGRÄNS
 - FASADLINJE I MARK
 - KONNEKTIONSLINJE
 - ENTRÉ
 - FG+00.00 FÄRDIG GOLVHÖJD
 - SLÄNT
 - LÅGPUNKTSLINJE
 - KS1 KANTSTÖD, VISNING 120 MM
 - KS1-0 KANTSTÖD, NOLLAD/FÖRSÄNKAT
 - KS2 KANTSTÖD, FÖRHÖJT, VISNING VARIERANDE
 - KS2 KANTSTÖD, FÖRHÖJT, VISNING VARIERANDE
 - KS3 KANTSTÖD MED AVVÄKNINGSSKYDD

- KA1 KANTSTÖD AV KUBBSARG, Ø120MM, SYNLIK HÖJD 120 MM. SÄTTS I JORDPUKTLIG BETONG
- F1 FRIS AV BETONGMARKSTEN. SÄTTS I JORDPUKTLIG BETONG
- X-BEF BEFINTLIG YTSKIKT SOM BEHÅLLS
- A1 ASFALTSYTA, KÖRBAR
- A2 ASFALTSYTA, GÅNGBAR
- BP1 BETONGPLATTOR, KÖRBAR
- BP2 BETONGPLATTOR, GÅNGBAR
- BP3 BETONGPLATTOR, PLATTRAD RUNT HUS
- AGR1 GRÄSARMERING, BRANDVÄG
- G1 MAKADAM
- G2 MAKADAM, TÄT BOTTEN
- SM1 STENMJÖL
- BS1 BAKSAND
- GR1 GRÄSYTA, SÄDD
- GR2 GRÄS-/ÄNGSYTA, SÄDD
- PL1 PLANTERINGSYTA BUSKAR
- PL2 PLANTERINGSYTA BUSKAR, STÖRD MARKPROFIL
- BA1 BARKFLIS, FALLSKYDD

- TR1 TRÄDGRÖP/SKELETTJORD VID TRAFIKYTA, UTBREDDNING
- TR2 TRÄDGRÖP/SKELETTJORD I GRÄS- ELLER PLANTERINGSYTA, UTBREDDNING
- TR3 TRÄDGRÖP/SKELETTJORD VID TRAFIKYTA, TÄT BOTTEN, UTBREDDNING

- BEFINTLIGT TRÄD SOM BEVARAS
- NYTT TRÄD, SORT ENLIGT VÄXTFÖRTECKNING
- INMÄTT TRÄDKRONA/DROPPZON
- SKY1 SKYLT PARKERING FÖR RÖRELSHINDRAD
- YB1 STOLP ARMATUR, ENL. E-HANDLING
- YB2 POLLAR ARMATUR, ENL. E-HANDLING
- YB3 VÄGG ARMATUR, ENL. E-HANDLING
- LINJEMÅLNING
- DB1 DAGVATTENBRUNN, ENL. VA-HANDLING
- LB1 LUFTBRUNN FÖR SKELETTJORD
- DB3 KUPOLBRUNN, ENL. VA-HANDLING
- BETONGTRUMMA FÖR DAGVATTENAVLEDNING

HÄNVISNINGAR

GÅNGPASSAGE/ÖVERGÅNGSSTÄLLE UTFÖRS ENLIGT TEKNISK HANDBOK, MED MÅLNING OCH TILLHÖRANDE SKYLTLING.

Bet	Ändringen avser	Datum	Sign
-----	-----------------	-------	------

SYSTEMHANDLING



E	ELKONSULT E-TEC AB	073-6655510
G	TREELINE CONSULTING AB	073-0844329
K	KÄVER & MELLIN	072-7326731
L	C.F. MØLLER SVERIGE AB	08-55576000
M	VKEN MILJÖKONSULT AB	070-6526445
V	DLV AB	076-0224797
VA	NIRAS SWEDEN AB	08-50384400

Uppdrag nr: 60764	Ritad/konstr. av: KTN	Handläggare: KARL TYRVAÄNEN
Datum: 2024-11-29	Ansvarig: SELMA BROSTRÖM	

SKEVIK, VÄRMDÖ
SKEVIK 1:190

FINPLANERING LANDSKAP
MARKPLANERINGSPLAN DEL 1

Skala a1	Skala a3	Nummer	Bet.
1:200	1:400	L-31-1-001	

