


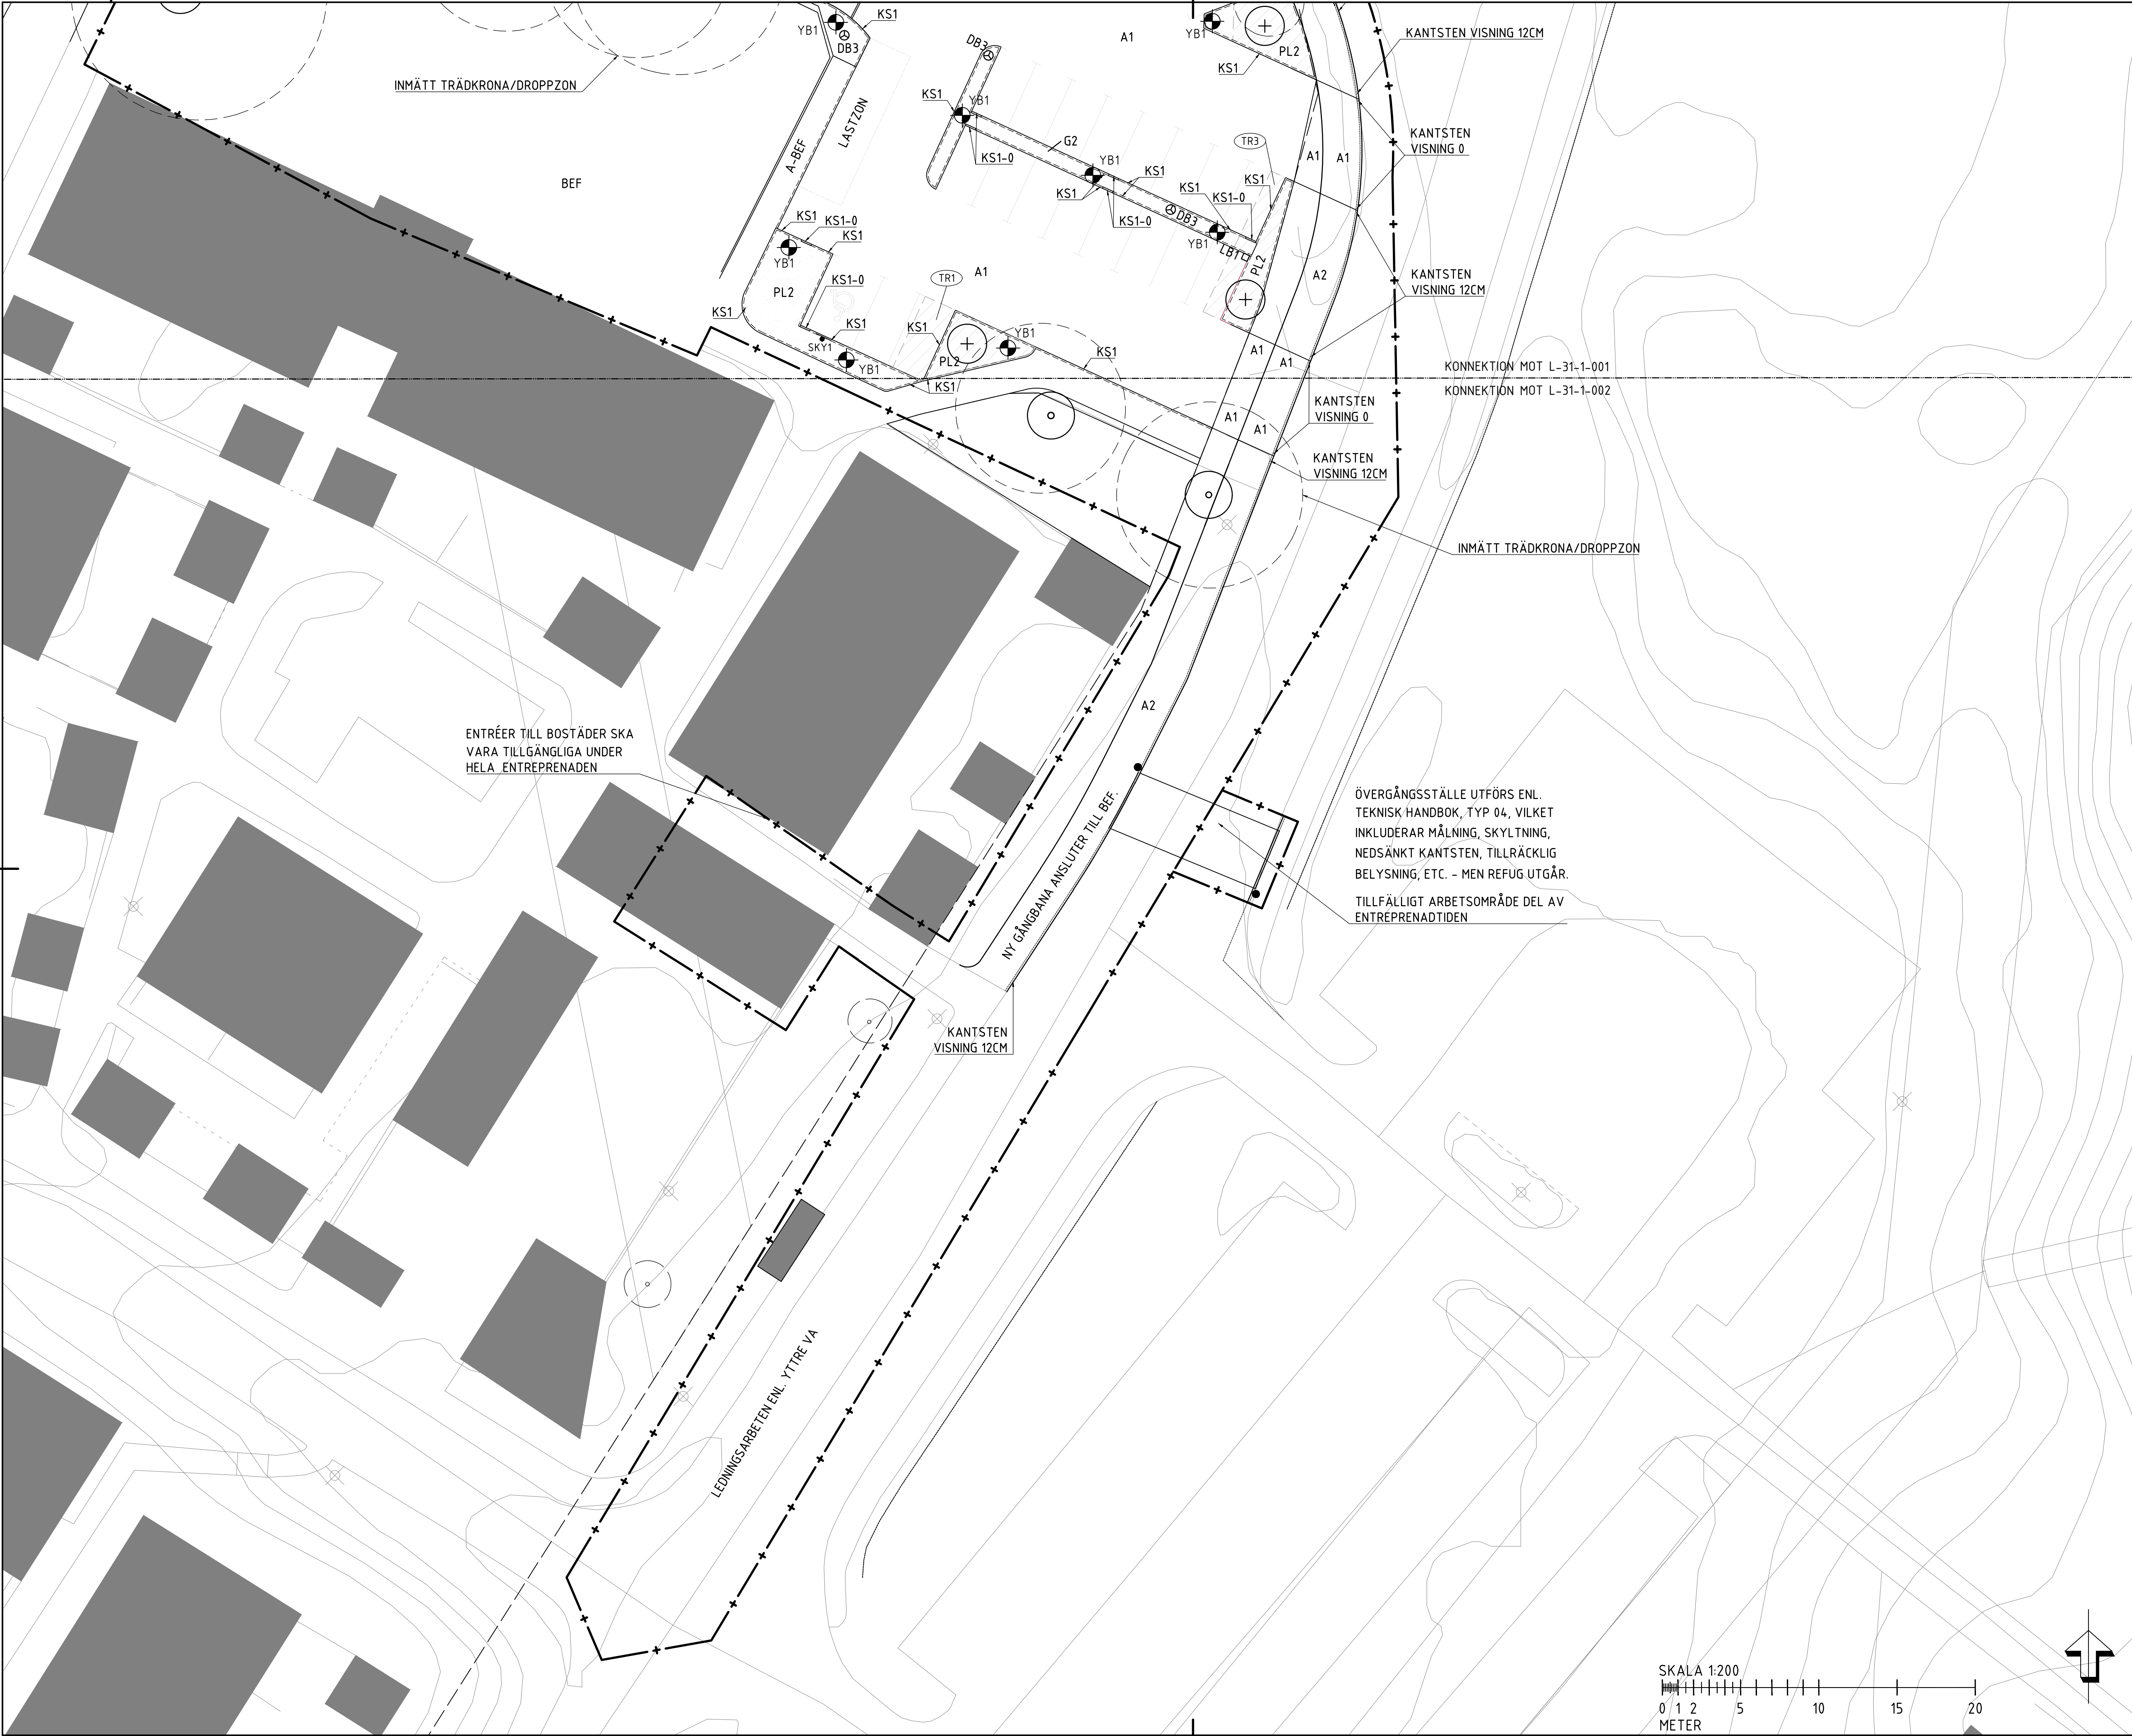

TECKENFÖRKLARING

KOORDINATSYSTEM: SWEREF 99 18 00
HÖJDSYSTEM: RH 2000

- ARBETSSOMRÅDESGRÄNS RITAD 1 M UTANFÖR
- VERKLIG GRÄNS
- FASTIGHETSGRÄNS
- FASADLINJE I MARK
- KONNEKTIONSLINJE
- ENTRÉ
- FG-00.00 FÄRDIG GOLVHÖJD
- SLÄNT
- LÅGPUNKTSLINJE
- KANTSTÖD, VISNING 120 MM
- KANTSTÖD, NOLLAD/FÖRSÄNKAT
- KANTSTÖD, FÖRHÖJT, VISNING VARIERANDE
- KANTSTÖD, FÖRHÖJT, VISNING VARIERANDE
- KANTSTÖD MED AVVÄNNINGSSKYDD

KA1	KANTSTÖD AV KUBBSÄRG, Ø120MM, SYNLIIG HÖJD 120 MM. SÄTTS I JORDPUKTLIG BETONG.
F1	FRIS AV BETONGMARKSTEN. SÄTTS I JORDPUKTLIG BETONG.
X-BEF	BEFINTLIG YTSKIKT SOM BEHÅLLS
A1	ASFALTSYTA, KÖRBAR
A2	ASFALTSYTA, GÅNGBAR
BP1	BETONGPLATTOR, KÖRBAR
BP2	BETONGPLATTOR, GÅNGBAR
BP3	BETONGPLATTOR, PLATTRAD RUNT HUS.
AGR1	GRÄSARMERING, BRANDVÄG
G1	MAKADAM
G2	MAKADAM, TÄT BOTTEN
SM1	STENMJÖL
BS1	BAKSAND
GR1	GRÄSYTA, SÄDD
GR2	GRÄS-/ÄNGSYTA, SÄDD
PL1	PLANTERINGSYTA BUSKAR
PL2	PLANTERINGSYTA BUSKAR, STÖRD MARKPROFIL
BA1	BARKFLIS, FALLSKYDD
TR1	TRÄDGRÖP/SKELETTJORD VID TRAFIKYTA, UTBREDDNING
TR2	TRÄDGRÖP/SKELETTJORD I GRÄS- ELLER PLANTERINGSYTA, UTBREDDNING
TR3	TRÄDGRÖP/SKELETTJORD VID TRAFIKYTA, TÄT BOTTEN, UTBREDDNING
○	BEFINTLIGT TRÄD SOM BEVARAS
+	NYTT TRÄD, SORT ENLIGT VÄXTFÖRTECKNING
○	INMÄTT TRÄDKRONA/DROPPZON
SKY1	SKYLT PARKERING FÖR RÖRELSEHINDRAD
YB1	STOLP ARMATUR, ENL. E-HANDLING
YB2	POLLAR ARMATUR, ENL. E-HANDLING
YB3	VÄGG ARMATUR, ENL. E-HANDLING
	LINJEMÄLNING
DB1	DAGVATTENBRUNN, ENL. VA-HANDLING
LB1	LUFTBRUNN FÖR SKELETTJORD
DB3	KUPOLBUNN, ENL. VA-HANDLING
	BETONGTRUMMA FÖR DAGVATTENAVLEDNING

HÄNVISNINGAR

GÅNGPASSAGE/ÖVERGÅNGSSTÄLLE UTFÖRS ENLIGT TEKNISK HANDBOK, MED MÄLNING OCH TILLHÖRANDE SKYLTNING.

Bef	Ändringen avser	Datum	Sign
SYSTEMHANDLING			
Orienteringsfigur			
E	ELKONSULT E-TEC AB	073-6655510	
G	TREELINE CONSULTING AB	073-0844329	
K	KÄVER & MELLIN	072-7326731	
X	L C.F. MØLLER SVERIGE AB	08-55576000	
M	VKEN MILJÖKONSULT AB	070-6526445	
V	DLV AB	076-0224797	
VA	NIRAS SWEDEN AB	08-50384400	
Köpdag nr: 60764	Ritad/kontroll: av KTN	Handläggare: KARL TYR VÄINEN	
Datum: 2024-11-29	Ansvarig: SELMA BROSTRÖM		
SKEVIK, VÄRMDÖ SKEVIK 1:190 FINPLANERING LANDSKAP MARKPLANERINGSPLAN DEL 2			
Skala a1: 1:200	Skala a3: 1:400	Nummer: L-31-1-002	Bef:

SKALA 1:200

0 1 2 5 10 15 20
METER

Ö