


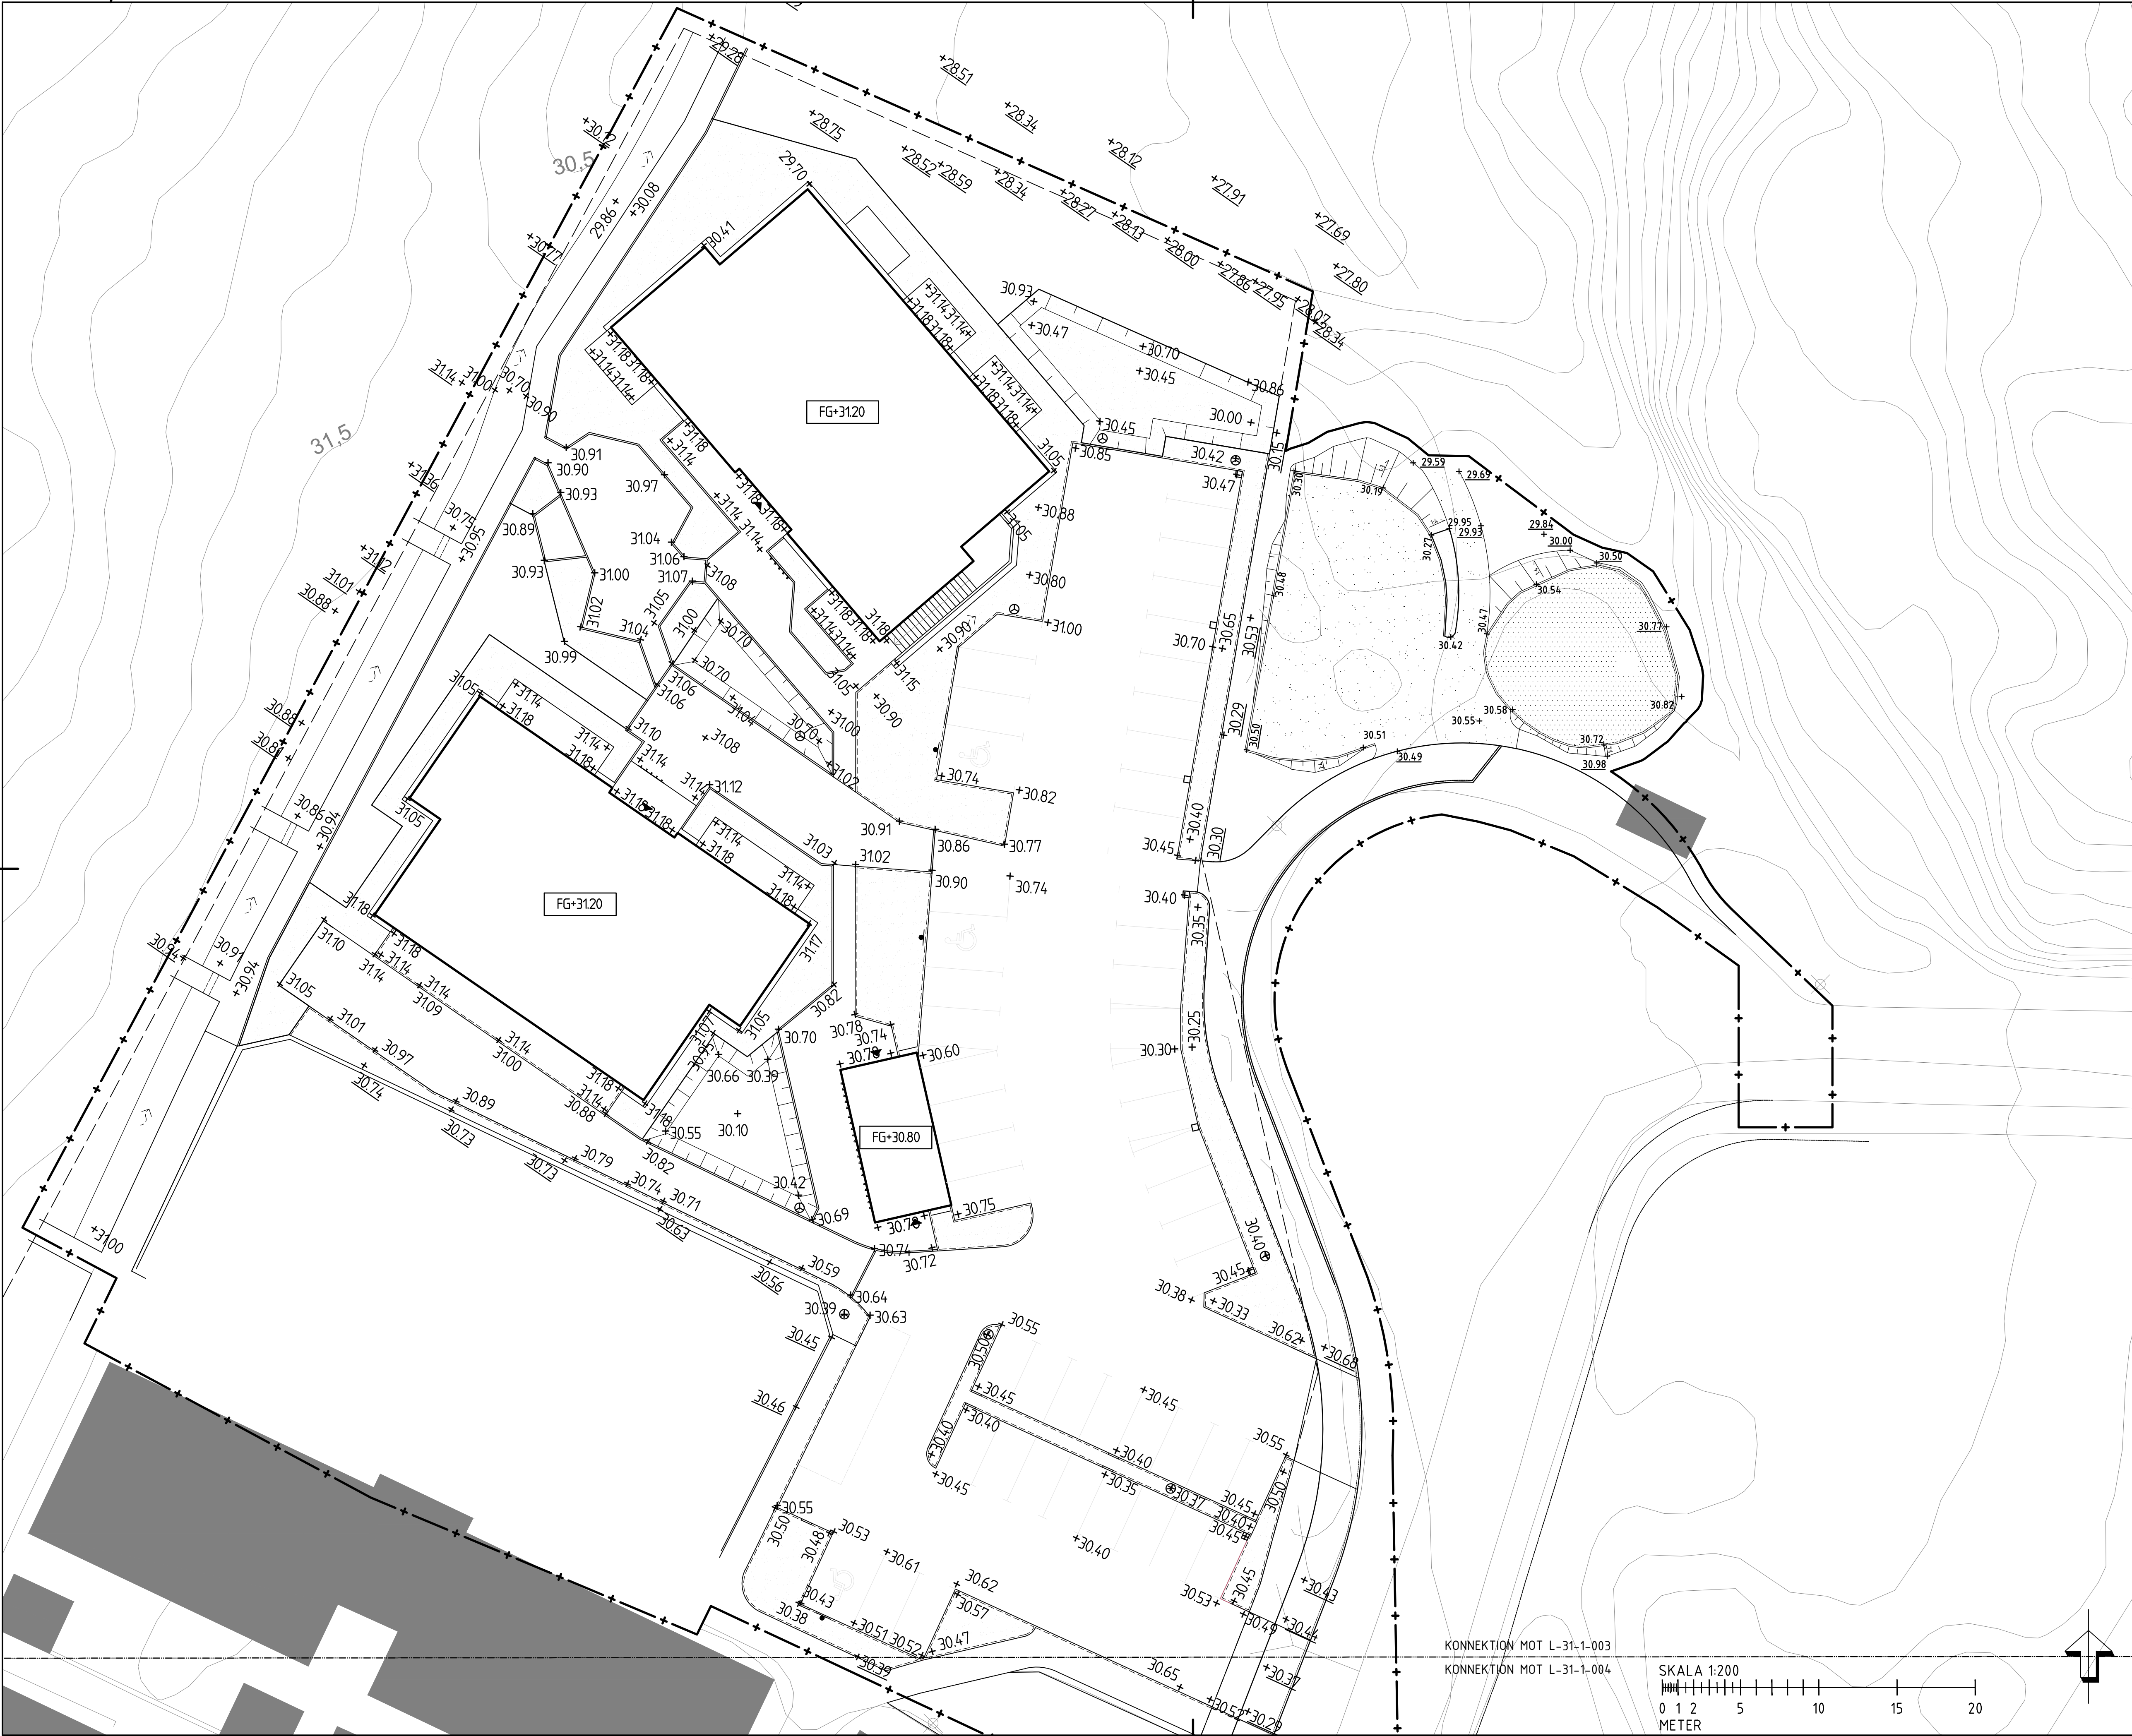

- TECKENFÖRKLARING
- KOORDINATSYSTEM: SWEREF 99 18 00
HÖJDSYSTEM: RH 2000
- ARBETSSOMRÅDESGRÄNS RITAD 1 M UTANFÖR
 - VERKLIG GRÄNS
 - FASTIGHETSGRÄNS
 - FASADLINJE I MARK
 - KONNEKTIONSLINJE
 - ENTRÉ
 - FG+00.00 FÄRDIG GOLVHÖJD
 - SLÄNT
 - LÅGPUNKTSLINJE
 - +0.00 BEFINTLIG MARKHÖJD SOM BEHÅLLS
 - +0.00 NY MARKHÖJD
 - DB1 DAGVATTENBRUNN, ENL. VA-HANDLING
 - LB1 LUFTBRUNN FÖR SKELETTJORD
 - DB3 KUPOLBRUNN, ENL. VA-HANDLING
 - BETONGTRUMMA FÖR DAGVATTENAVLEDNING

Bet	Ändringen avser	Datum	Sign
-----	-----------------	-------	------

SYSTEMHANDLING

E	ELKONSULT E-TEC AB	073-6655510
G	TREELINE CONSULTING AB	073-0844329
K	KÄVER & MELLIN	072-7326731
L	C.F. MØLLER SVERIGE AB	08-55576000
M	VKEN MILJÖKONSULT AB	070-6526445
V	DLV AB	076-0224797
VA	NIRAS SWEDEN AB	08-50384400

Koppdrag nr: 60764	Ritad/konstr. av KTN	Handläggare KARL TYRIVÄINEN
Datum 2024-11-29	Ansvarig SELMA BROSTRÖM	

SKEVIK, VÄRMDÖ

SKEVIK 1:190

FINPLANERING LANDSKAP

HÖJDSÄTTNINGSPÅN DEL 1

Skala a1 1:200	Skala a3 1:400	Nummer L-31-1-003	Bet.
-------------------	-------------------	----------------------	------

KONNEKTION MOT L-31-1-003
KONNEKTION MOT L-31-1-004

