



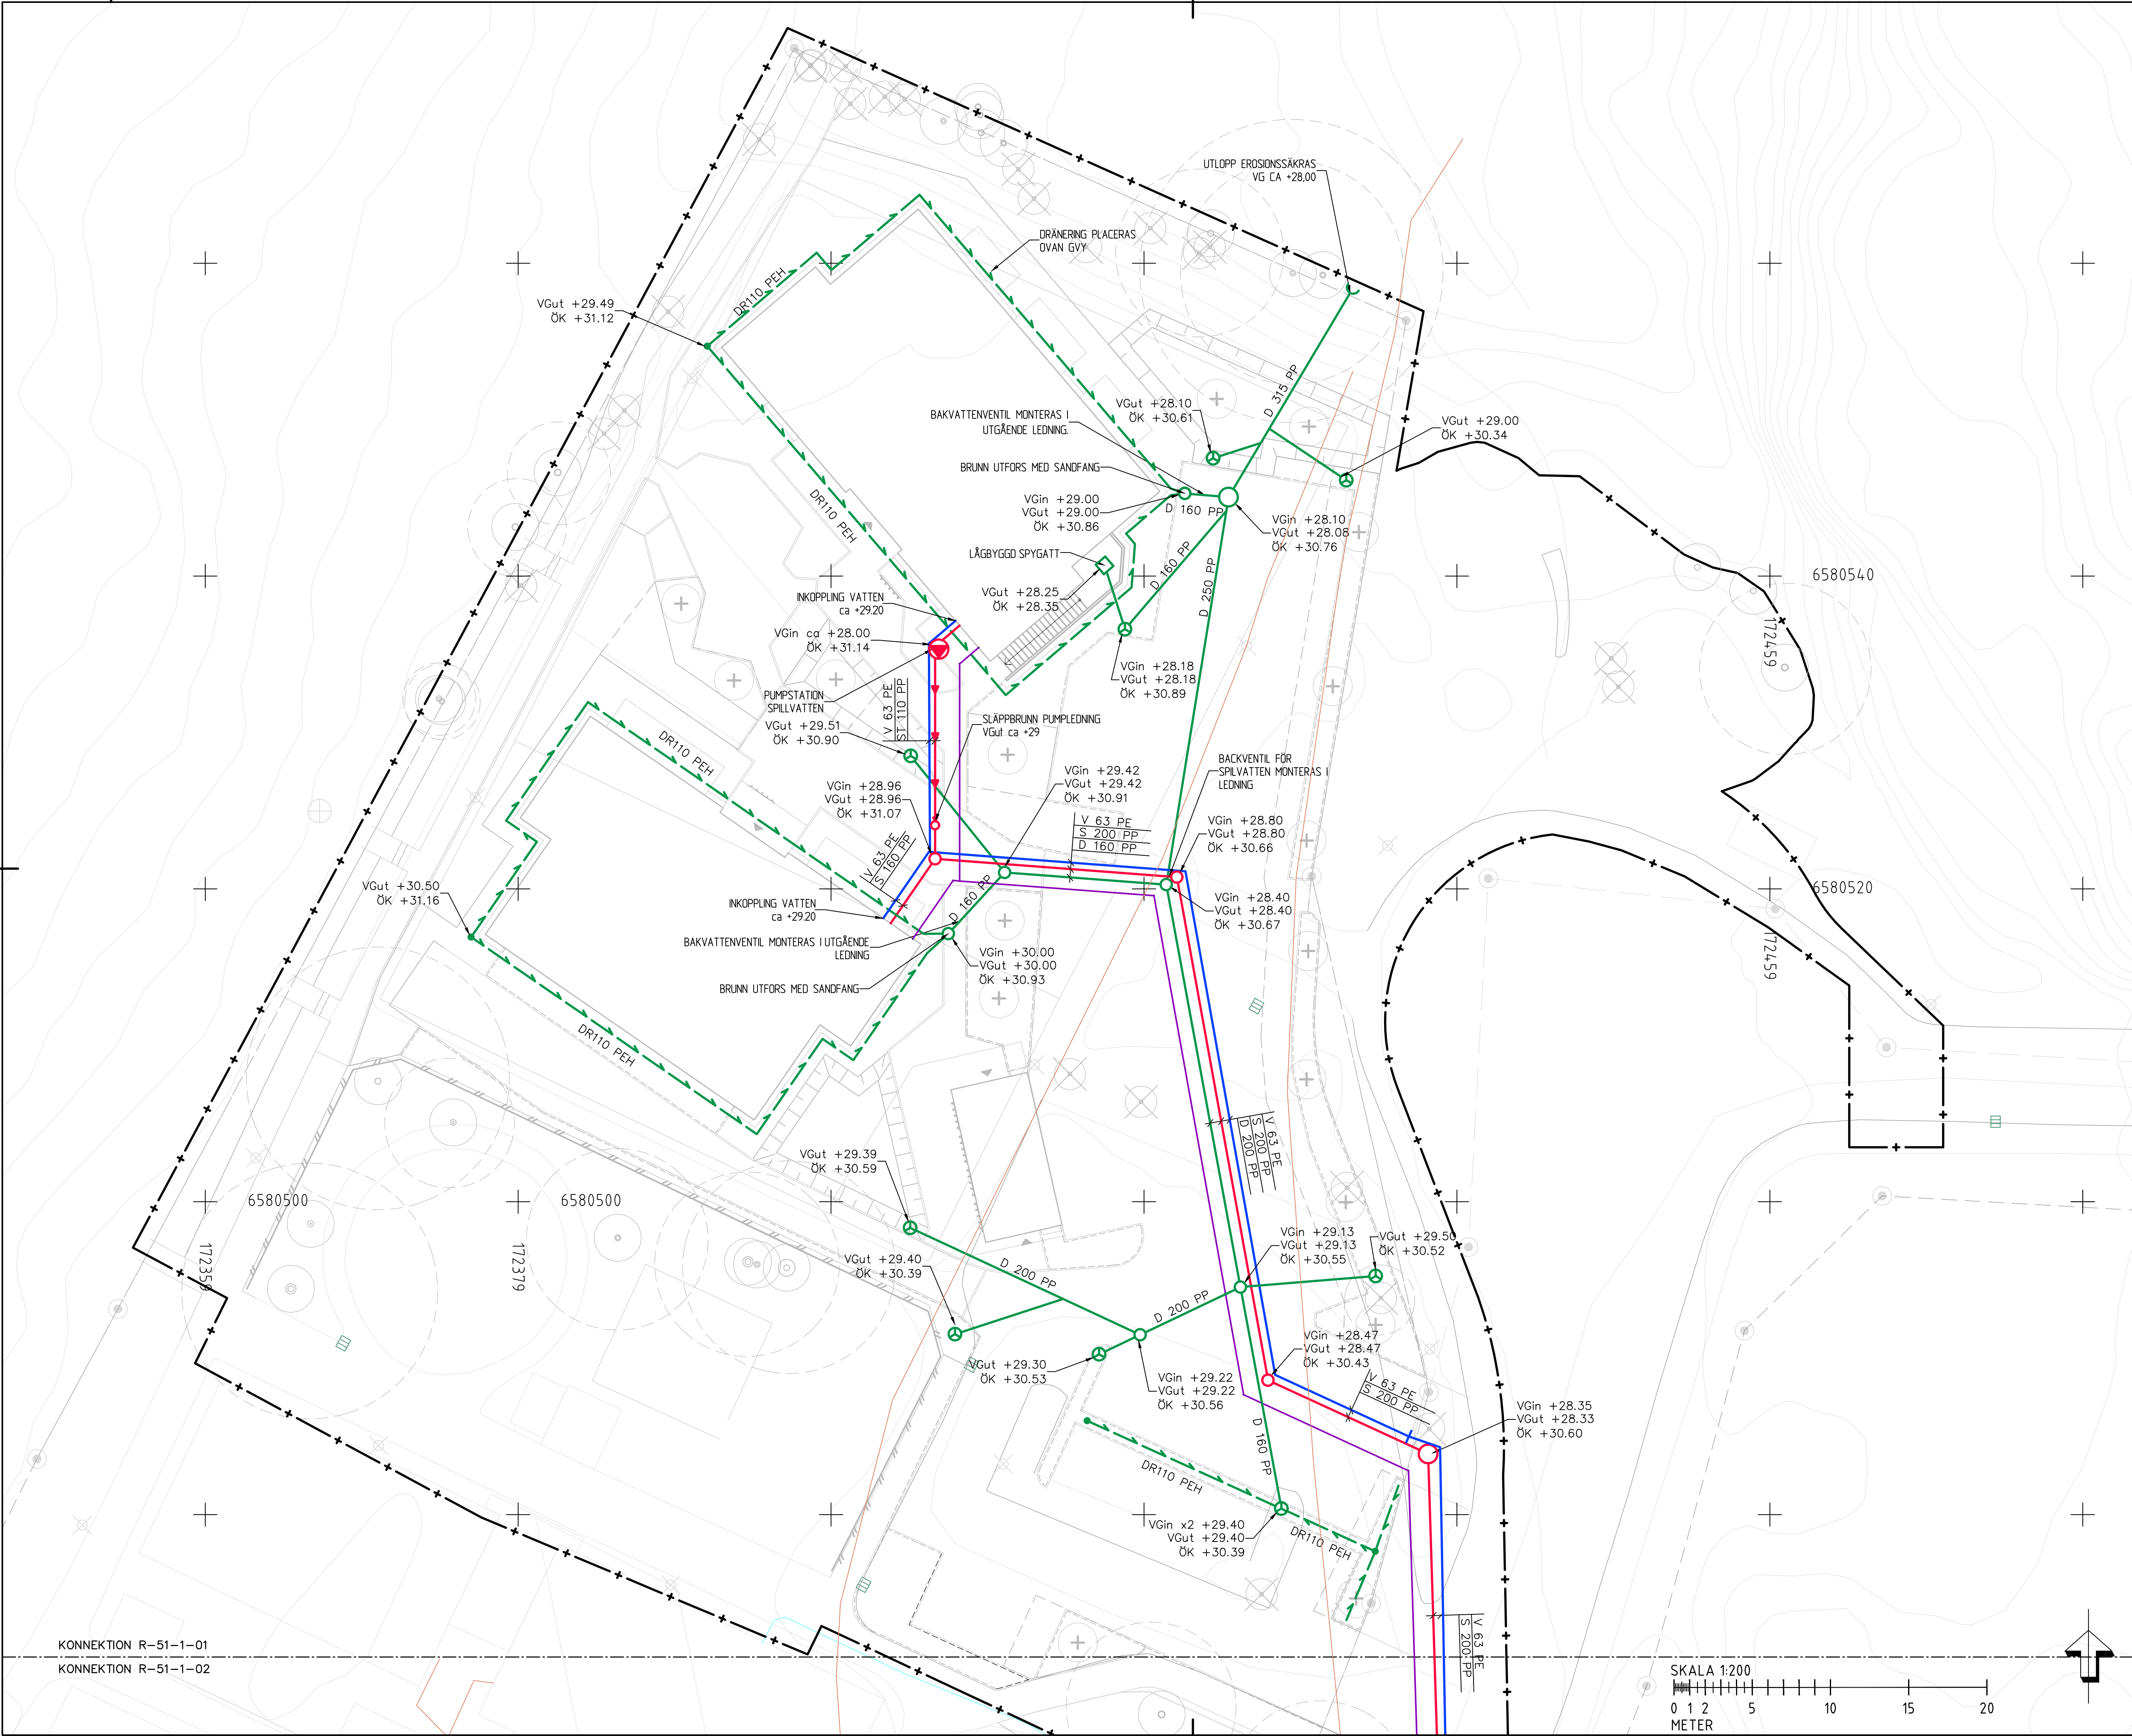

KONNEKTION R-51-1-01
KONNEKTION R-51-1-02

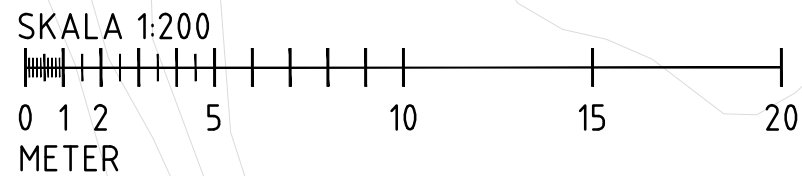

TECKENFÖRKLARING

KOORDINATSYSTEM: SWEREF 99 1800
HÖJDSYSTEM: RH2000

PROJETERAT VA

- SPILLVATTEN
- SPILLVATTEN TRYCK
- DAGVATTEN
- VATTEN
- RENSBRUNN Ø200
- TILLSYNSBRUNN Ø600
- NEDSTIGNINGSBRUNN Ø1000
- DAGVATTENBRUNN MED KUPOLBETÄCKNING OCH SANDFÅNG Ø400 PP
- SPYGATT
- UTLOPP
- PUMPSTATION

PROJETERAT ÖVRIGT

- FJÄRRVÄRME
- ARBETSSOMRÅDESGRÄNS

BEFINTLIGT

- OPTO
- SKANOVA (INTOLKAT UNGEFÄRLIGT LÄGE)
- SPILLVATTEN
- DAGVATTEN
- VATTEN

ANMÄRKNINGAR

SPILLVATTEN OCH VATTENLEDNINGAR ANLÄGGS PÅ FROSTFRITT DJUP. SPILLVATTENLEDNINGAR ANLÄGGS MED MINST 10 ‰ LUTNING.

ANSLUTNINGSPUNKTER FÖR SPILL- OCH VATTENLEDNING KONTROLLERAS I SKICK OCH NIVÅER.

DAGVATTENLEDNING MELLAN DAGVATTENBRUNN OCH HUVUDLEDNING ÄR 160 PP.

ÖK BRUNNAR ANTAGNA FRÅN LA HANDLING. BRUNNSLOCK ANPASSAS TILL NY MARKNIVÅ I NÄSTA SKEDE.

FJÄRRVÄRME ENBART SCHEMATISKT PLACERAD. DIMENSIONERING SAMT DETALJERAD PROJEKTERING I NÄSTA SKEDE. ANTAGEN DN 160.


PLOTTAS I FÄRG.

Bet	Ändringen avser	Datum	Sign
-----	-----------------	-------	------

SYSTEMHANDLING



Orienteringsfigur

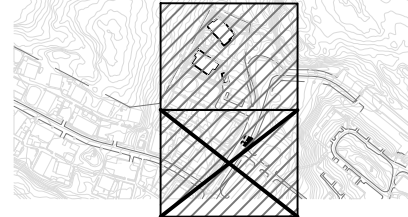

E	ELKONSULT E-TEC AB	073-6655510
G	TREELINE CONSULTING AB	073-0844329
K	KÅVER & MELLIN	072-7326731
L	C.F. MØLLER SVERIGE AB	08-55576000
M	VIKEN MILJÖKONSULT AB	070-6526445
V	DLV AB	076-0224797
X	VA NIRAS SWEDEN AB	08-50384400

Uppdrag nr. 60764	Ritad/tecknat av KUSH	Handläggare ELISE BAUMANN
Datum 2024-11-29	Ansvarig ELISE BAUMANN	

SKEVIK, VÄRMDÖ
SKEVIK 1:190
VA PLAN 1/2

Skala a1 1:200	Skala a3 1:400	Nummer R-51-1-01	Bet.
-------------------	-------------------	---------------------	------