


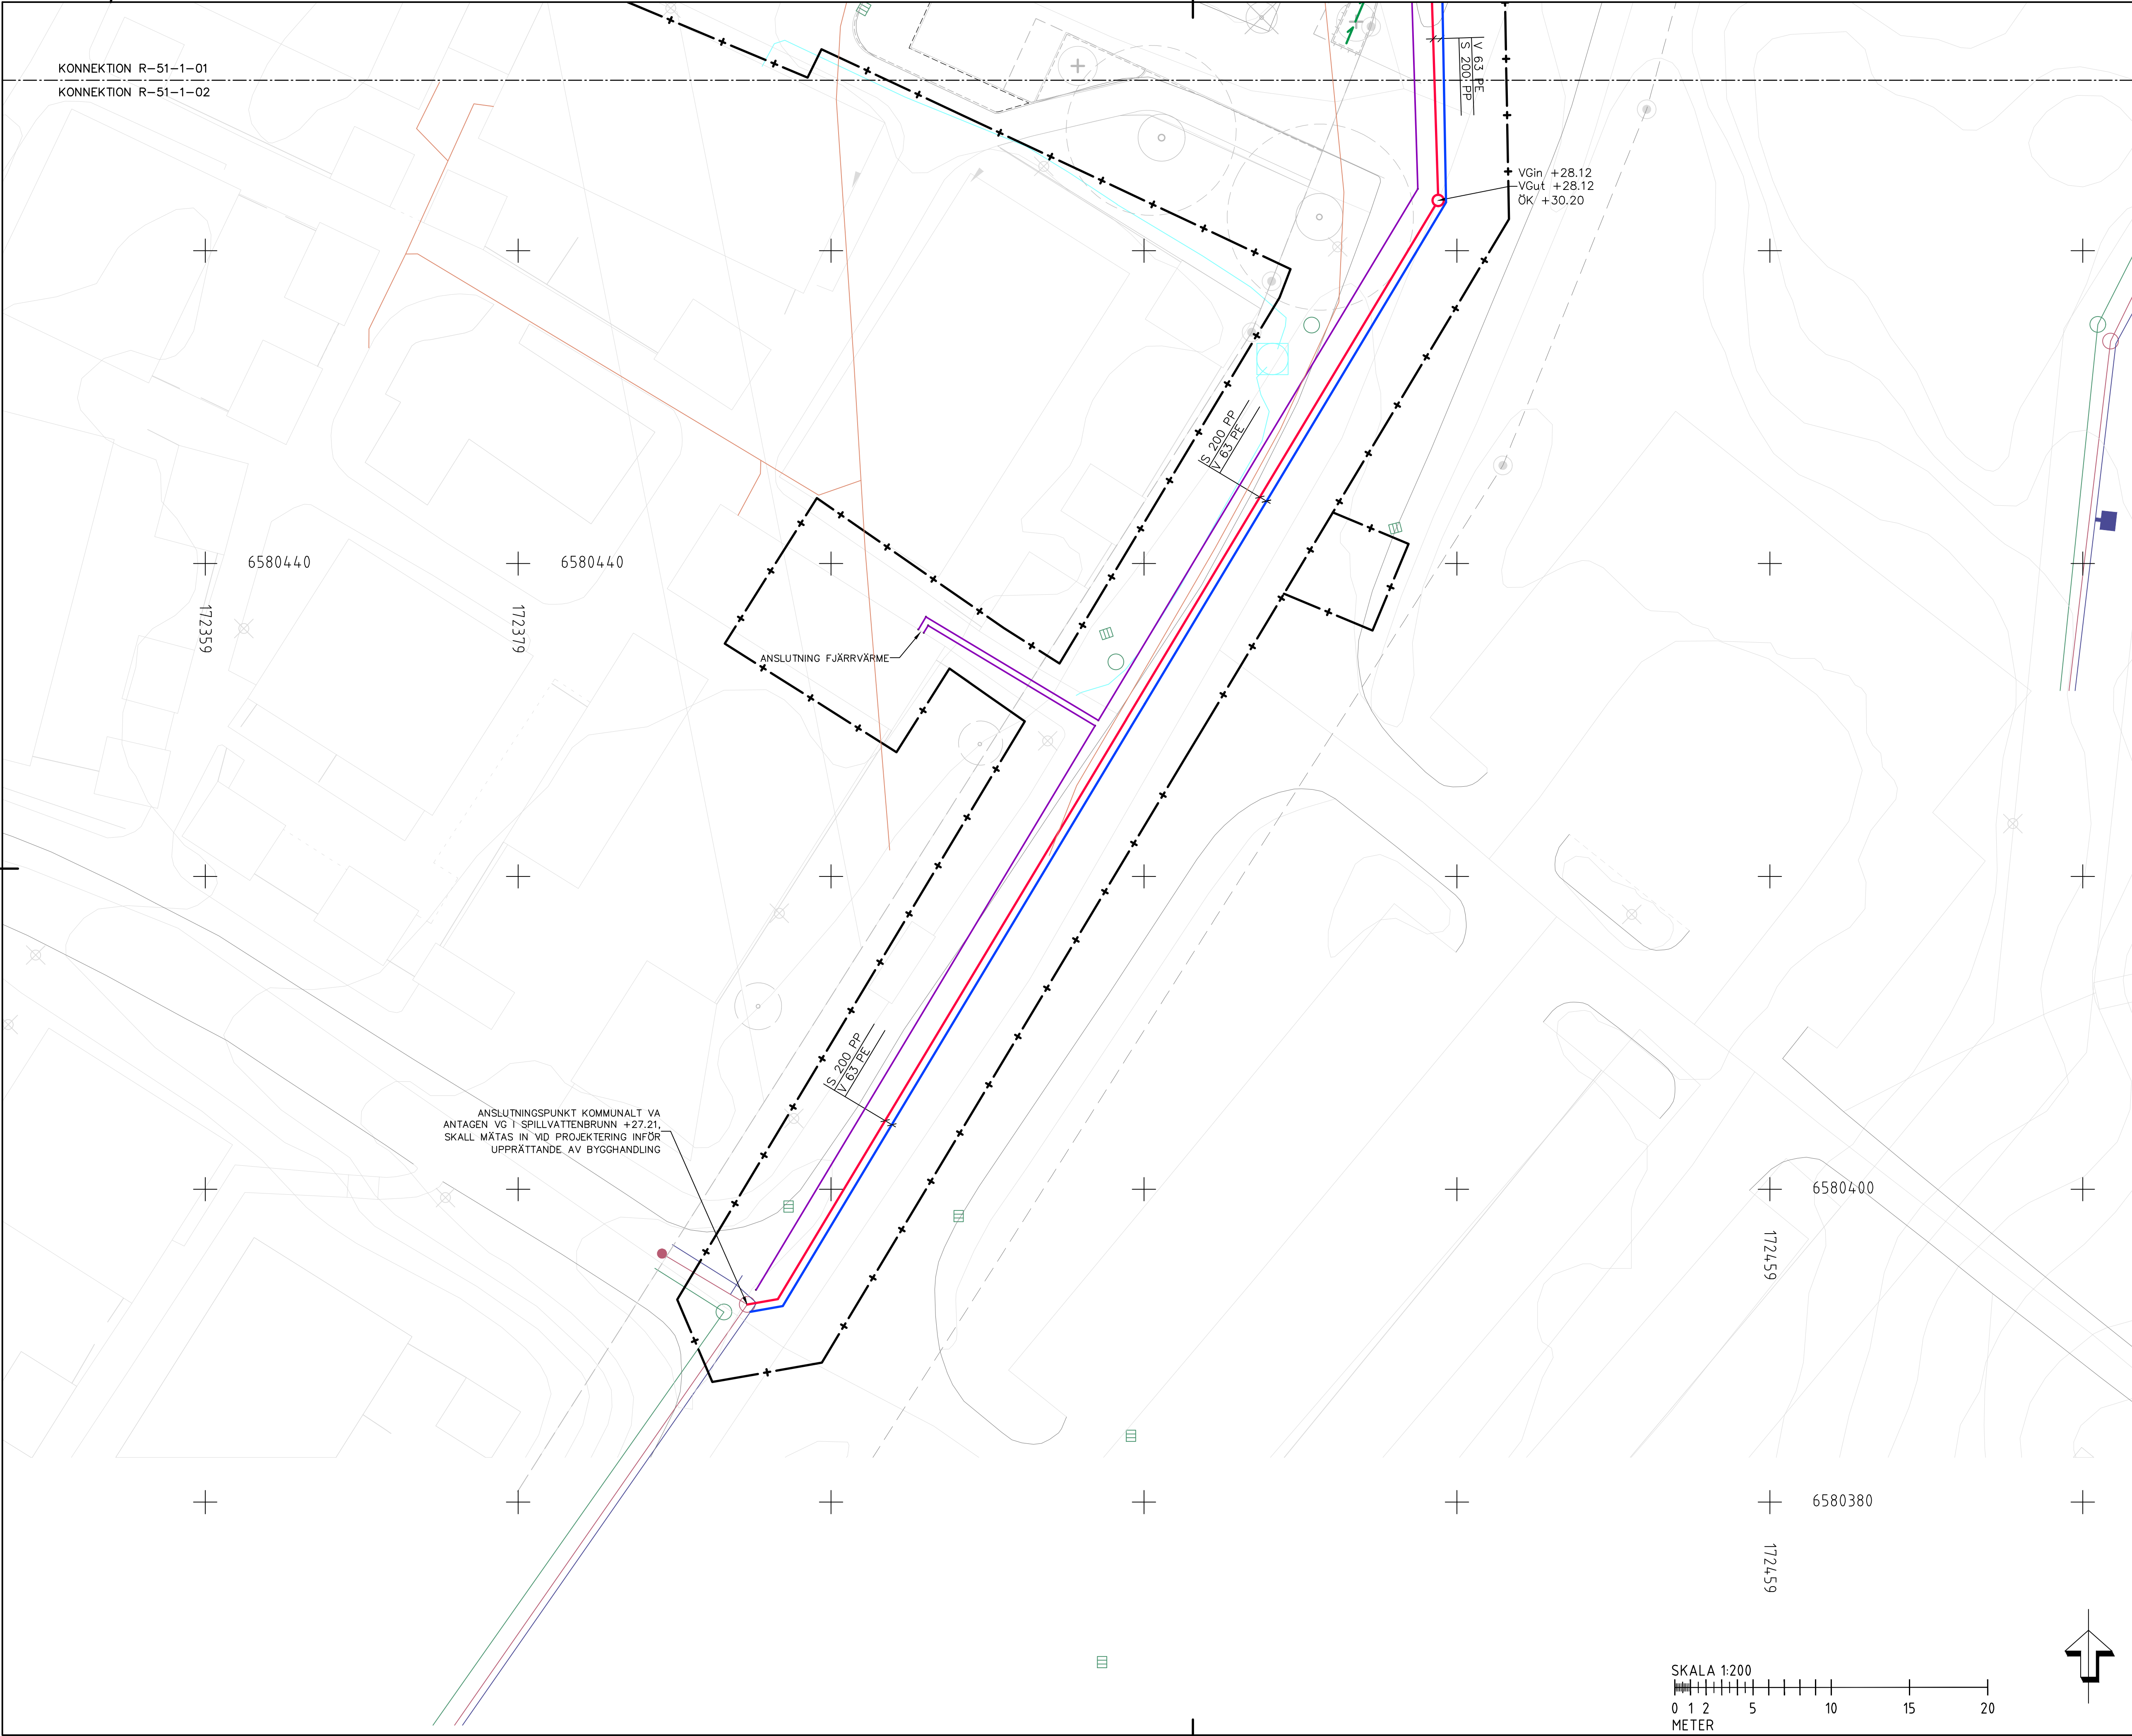

KONNEKTION R-51-1-01
KONNEKTION R-51-1-02

ANSLUTNINGSPUNKT KOMMUNALT VA
ANTAGEN VG 1-SPILLVATTENBRUNN +27.21,
SKALL MÄTAS IN VID PROJEKTERING INFÖR
UPPRÄTTANDE AV BYGGHANDLING

ANSLUTNING FJÄRRVÄRME

V 63 PE
S 200 PP
VGin / +28.12
VGut / +28.12
ÖK / +30.20

S 200 PP
V 63 PE

- TECKENFÖRKLARING
- KOORDINATSYSTEM: SWREF 99 1800
HÖJDSYSTEM: RH2000
- PROJEKTERAT VA
- SPILLVATTEN
 - SPILLVATTEN TRYCK
 - DAGVATTEN
 - VATTEN
- RENSBRUNN Ø200
 - TILLSYNSBRUNN Ø600
 - NEDSTIGNINGSBRUNN Ø1000
 - DAGVATTENBRUNN MED KUPOLBETÄCKNING OCH SANDFÄNG Ø400 PP
 - SPYGATT
 - UTLOPP
 - PUMPSTATION

- PROJEKTERAT ÖVRIGT
- FJÄRRVÄRME
 - ARBETSSOMRÅDESGRÄNS

- BEFINTLIGT
- OPTO
 - SKANOVA (INTOLKAT UNGEFÄRLIGT LÄGE)
 - SPILLVATTEN
 - DAGVATTEN
 - VATTEN

ANMÄRKNINGAR

SPILLVATTEN OCH VATTENLEDNINGAR ANLÄGGS PÅ FROSTFRITT DJUP. SPILLVATTENLEDNINGAR ANLÄGGS MED MINST 10 ‰ LÜTNING.


ANSLUTNINGSPUNKTER FÖR SPILL- OCH VATTENLEDNING KONTROLLERAS I SKICK OCH NIVÅER.

DAGVATTENLEDNING MELLAN DAGVATTENBRUNN OCH HUVUDLEDNING ÄR 160 PP.

ÖK BRUNNAR ANTAGNA FRÅN LA HANDLING. BRUNNSLOCK ANPASSAS TILL NY MARKNIVÅ I NÄSTA SKEDE.

FJÄRRVÄRME ENBART SCHEMATISKT PLACERAD. DIMENSIONERING SAMT DETALJERAD PROJEKTERING I NÄSTA SKEDE. ANTAGEN DN 160.

PLOTTAS I FÄRG.

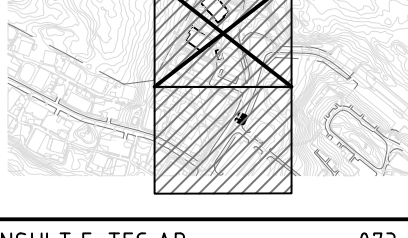Bet.	Ändringen avser	Datum	Sign.
SYSTEMHANDLING			
			
Orienteringsfigur			
			
E	ELKONSULT E-TEC AB	073-6655510	
G	TREELINE CONSULTING AB	073-0844329	
K	KÄVER & MELLIN	072-7326731	
L	C.F. MØLLER SVERIGE AB	08-55576000	
M	VIKEN MILJÖKONSULT AB	070-6526445	
V	DLV AB	076-0224797	
X	VA NIRAS SWEDEN AB	08-50384400	
Uppdrag nr. 60764		Ritad/konstr. av KUSH	Handläggare ELISE BAUMANN
Datum 2024-11-29		Ansvarig ELISE BAUMANN	
SKEVIK, VÄRMDÖ			
SKEVIK 1:190			
VA PLAN 2/2			
Skala a1 1:200	Skala a3 1:400	Nummer R-51-1-02	
Bet.			

SKALA 1:200

0 1 2 5 10 15 20

METER

