



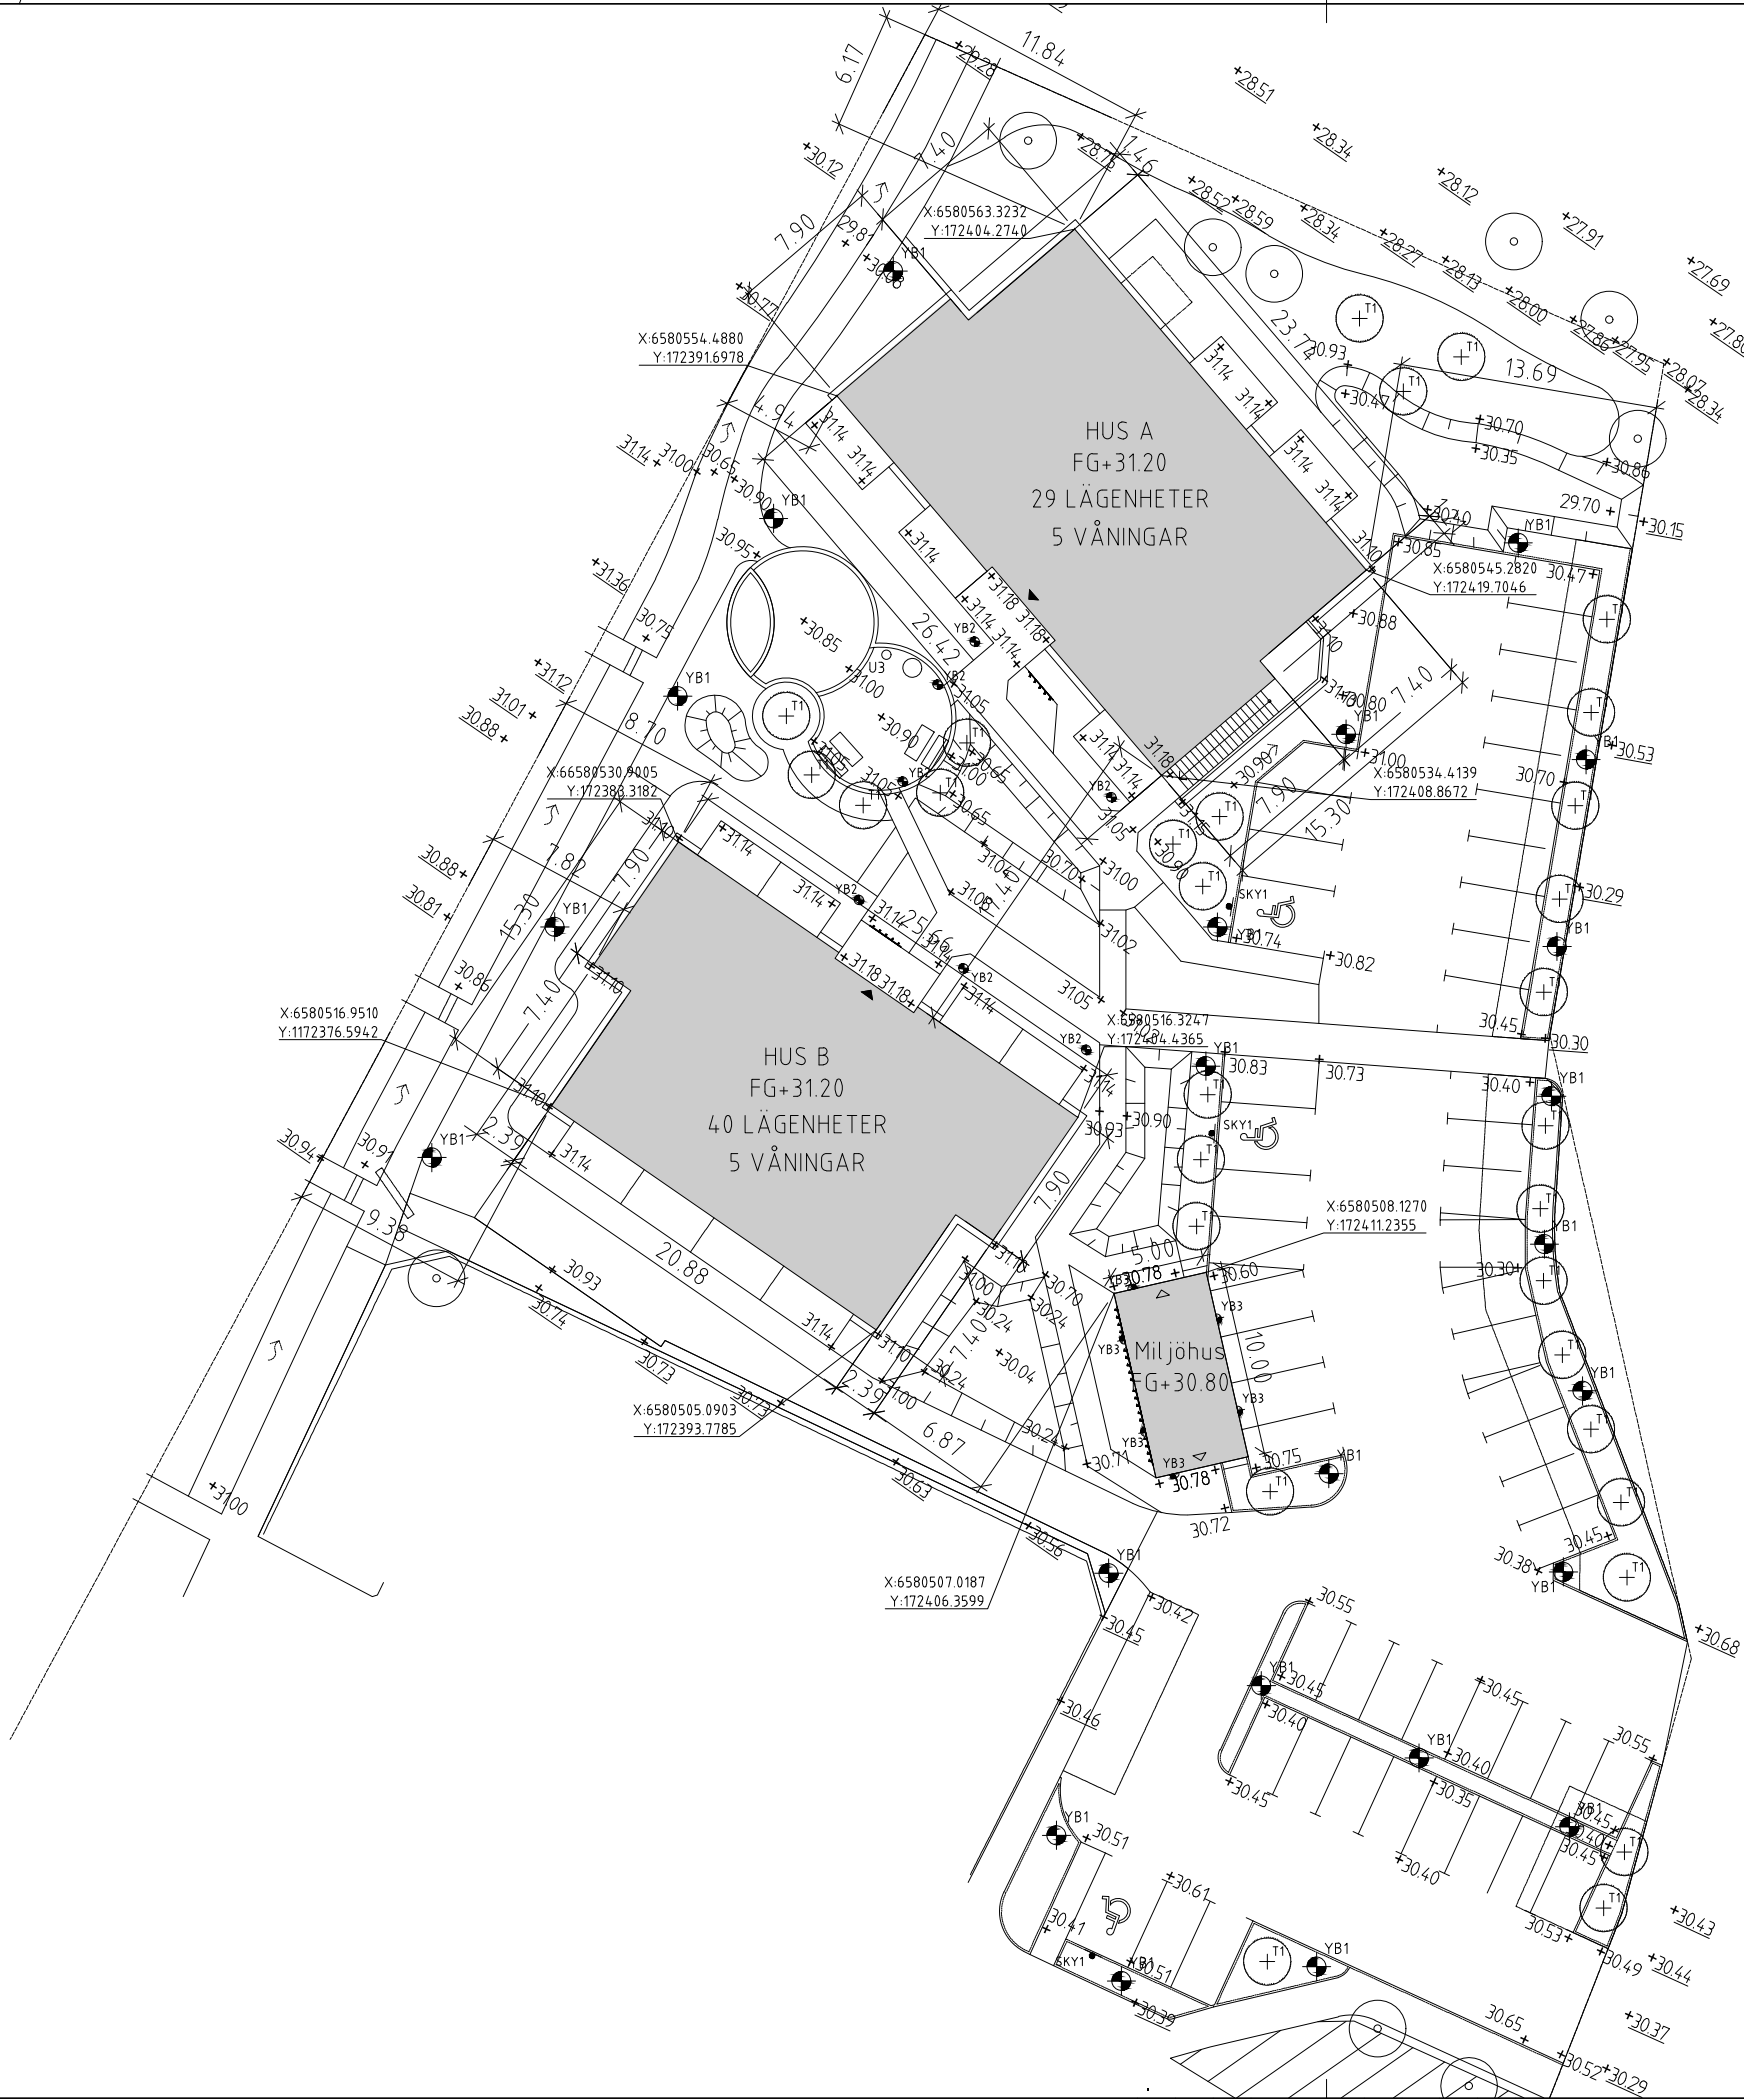

SKALA 1:200 (A1) 0 1 2 5 10 15 20

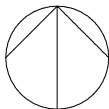

FÖRESKRIFTER

Höjdsystem: SWEREF 99 18 00
Koordinatsystem: RH 2000

FÖRKLARINGAR

- Fastighetsgräns
- Fasadliv byggnad
- Entrémarkering byggnad
- Taköverhäng, byggnadsdel över mark
- FG+00.00 Nivå färdig golvhöjd
- +00.00 Befintlig markhöjd
- +00.00 Projekterad markhöjd
- Slänt, släntkrön resp släntfot
- Rännalsplattor 350x350x70 mm
- Lågpunktlinje (dikesanvisning)
- Trappa

Total antal p-platser boende :
47 st, varav 2 st HKP och 1 st MC.

Total antal p-platser förskola:
3 st, varav 1 st HKP.

BET	ANT	ÄNDRINGEN AVSER	SIGN	DATUM
-----	-----	-----------------	------	-------

BYGGLOVSHANDLING

JSB VI BYGGER
FÖR FLER



A	MINJAR AB	0739-10 01 05
K	MINJAR AB	0739-10 01 14
VS	AFRY	072-204 5949
V	VENTEX ENTREPRENAD AB	0456-135 95
E	ETG EL-TELEGRUPPEN AB	0454-30 64 97
L	PARK I SYD	0424-45 23 00

UPPDRAG NR 9801030	RITAD / KONSTRUERAD AV YB, SG	HANDLAGGARE YB, SG
DATUM 2021-12-22	ANSVARIG SG	

SKEVIK 1:190, VÄRMDÖ
NYBYGGNAD AV FLERBOSTADSHUS

SITUATIONSPLAN

SKALA A1 1:200	SKALA A3 1:400	NUMMER A-01-1-001	BET
-------------------	-------------------	----------------------	-----