



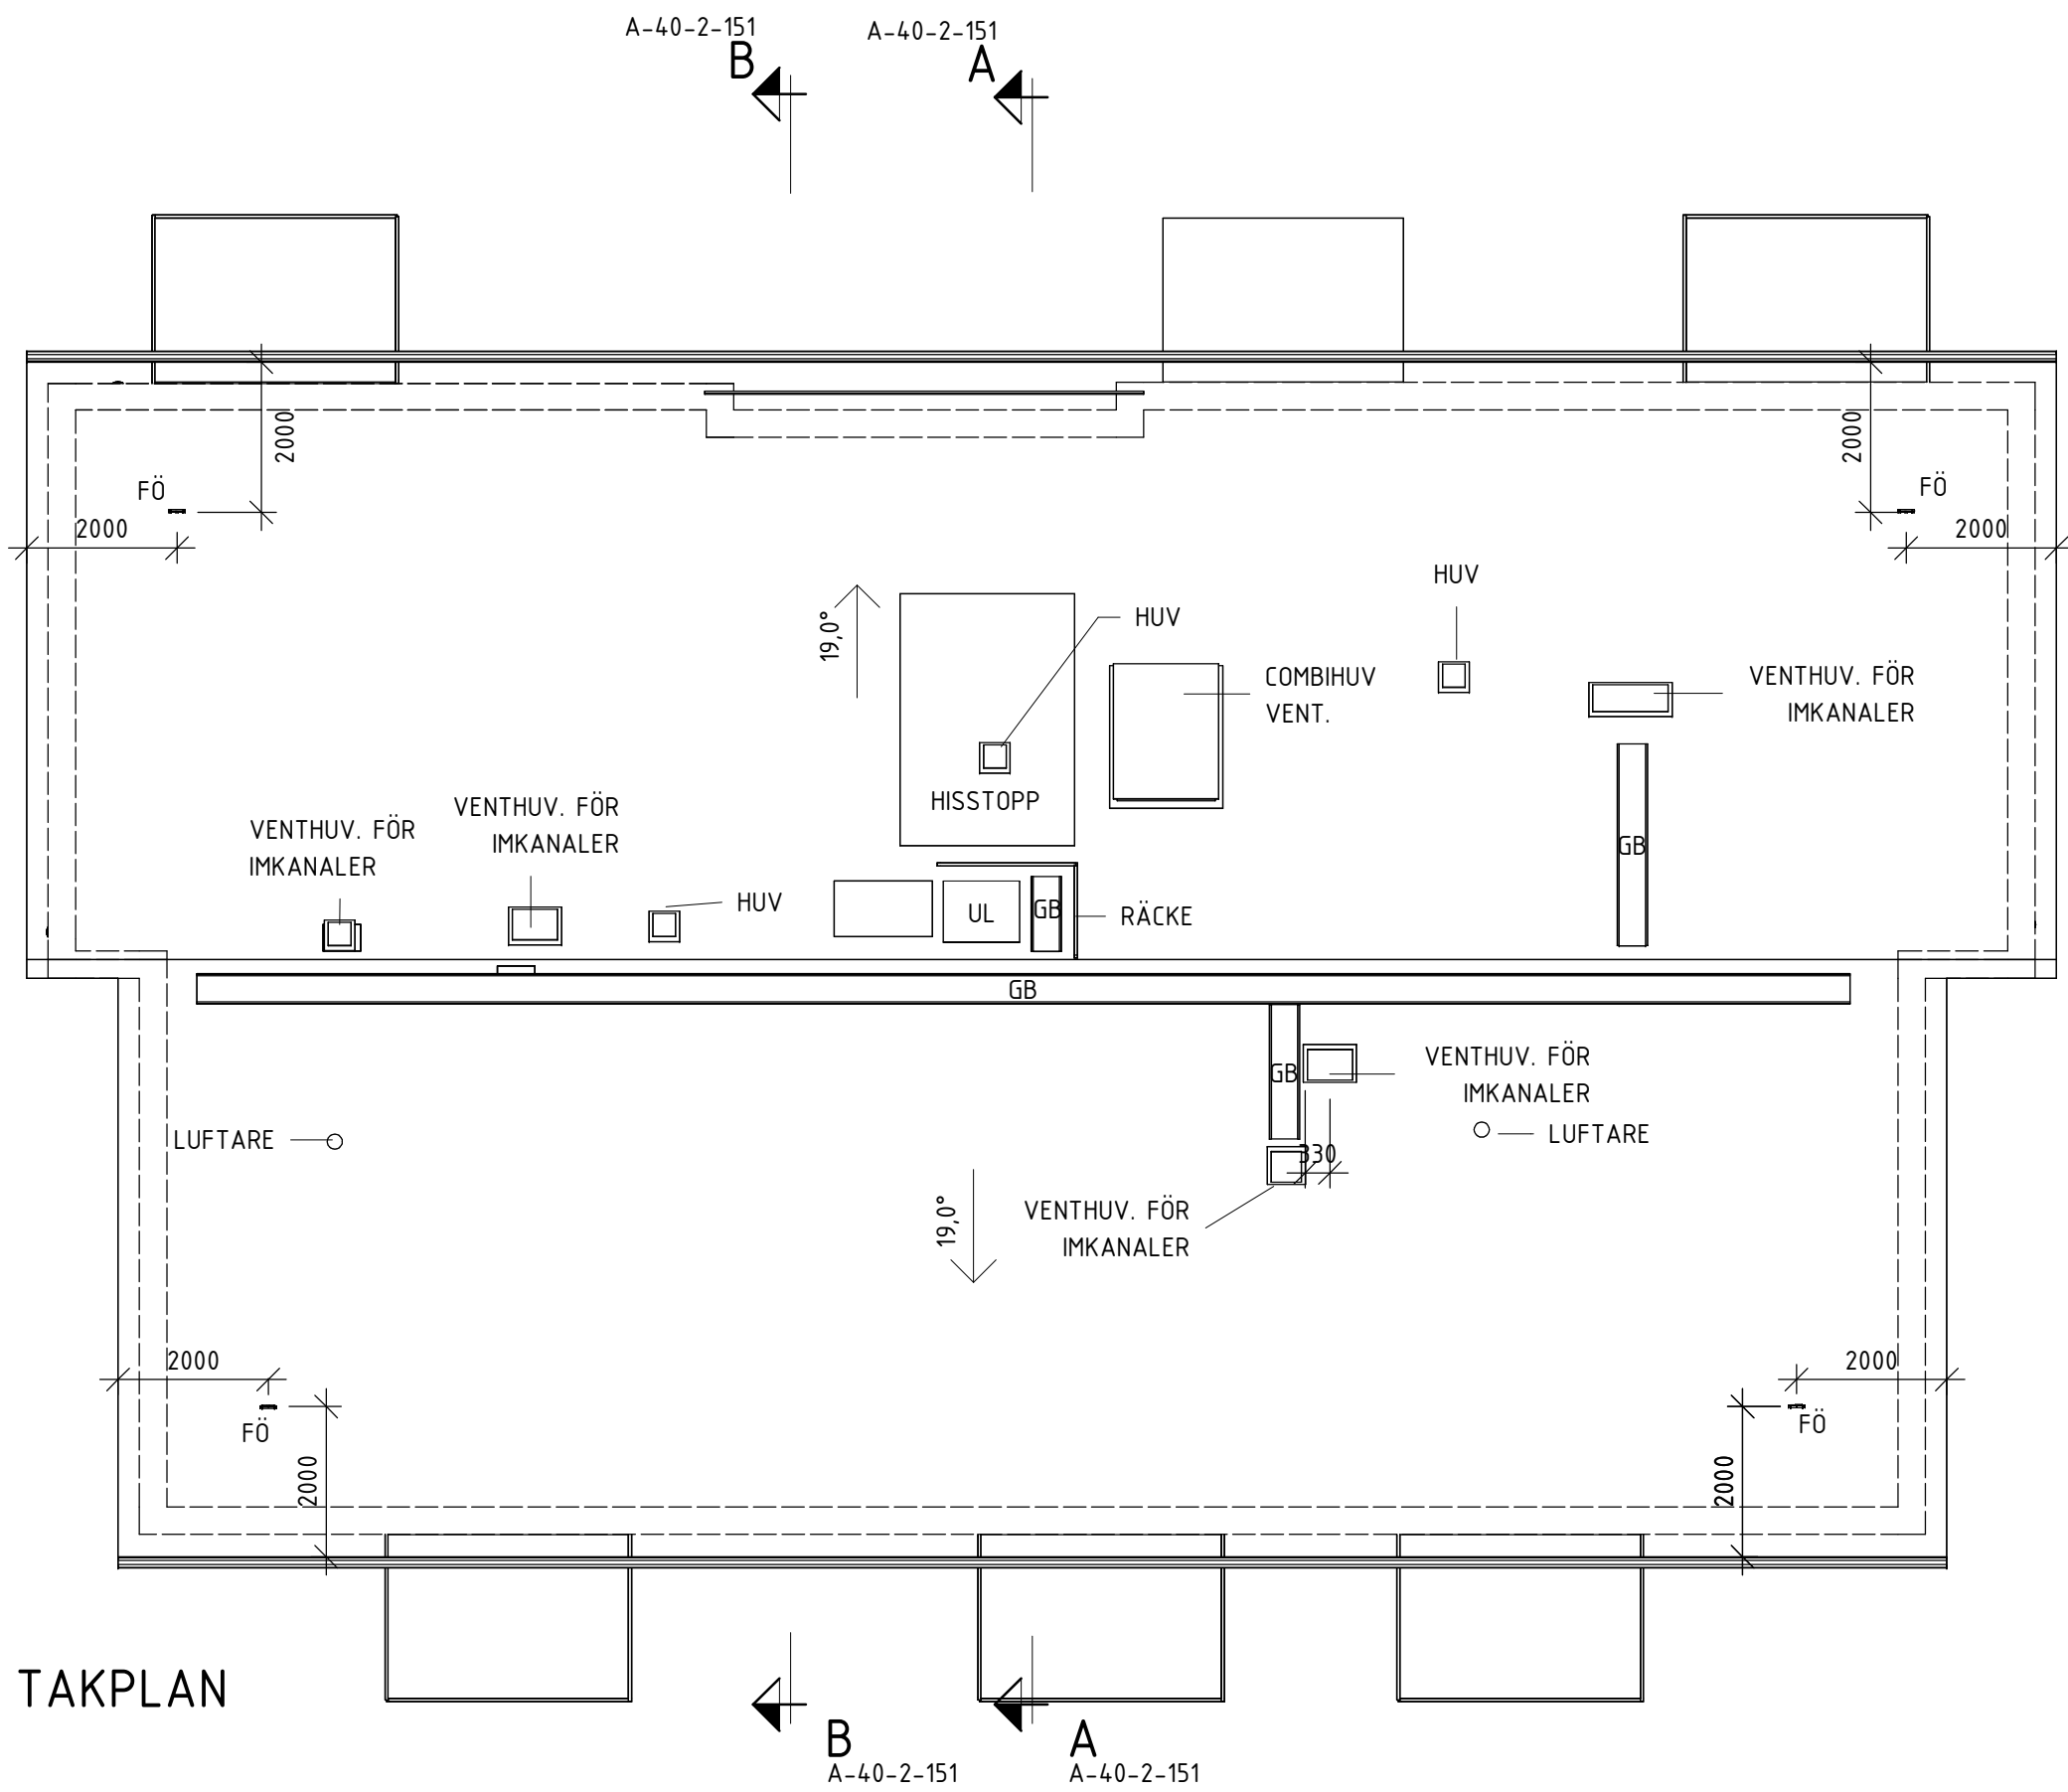

TAKPLAN

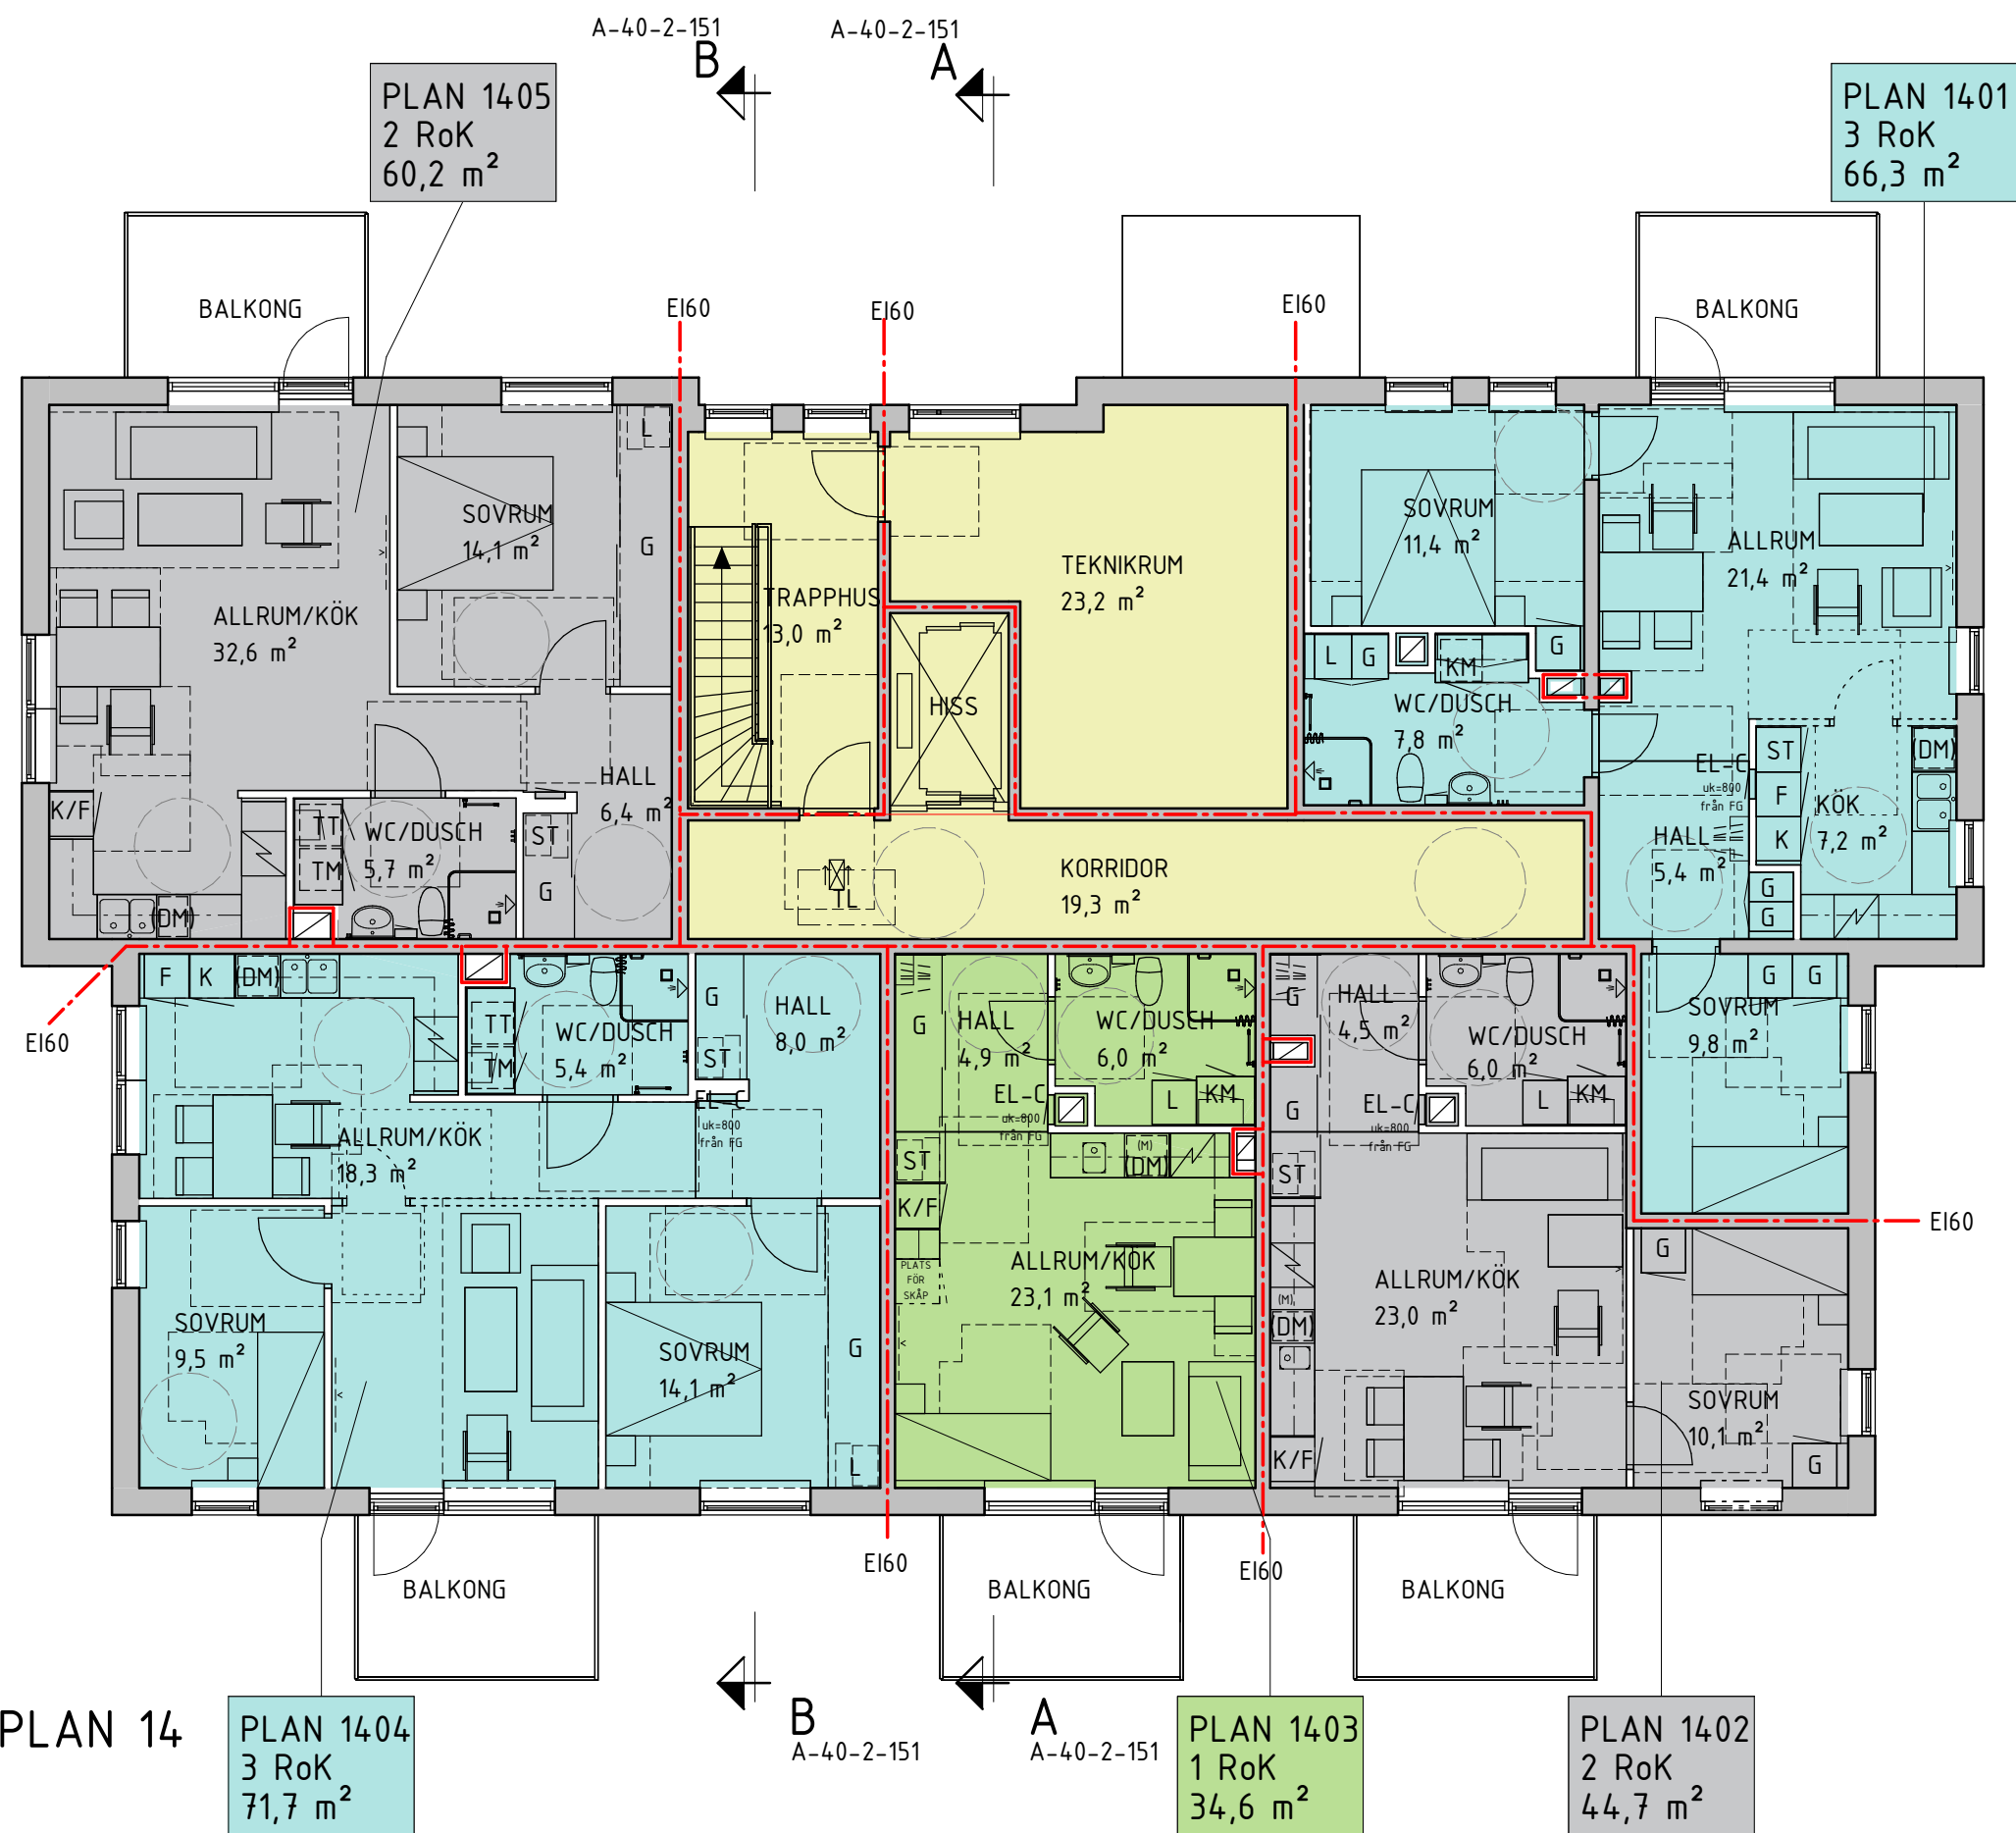

PLAN 14

Fördelning lägenheter Hus A		
LGH-Nummer	BOA	Name
1001	34,7 m ²	1 RoK
1002	44,8 m ²	2 RoK
1003	44,8 m ²	2 RoK
1004	34,6 m ²	1 RoK
1005	71,9 m ²	3 RoK
1006	60,4 m ²	2 RoK
1101	34,6 m ²	1 RoK
1102	44,7 m ²	2 RoK
1103	44,7 m ²	2 RoK
1104	34,6 m ²	1 RoK
1105	71,8 m ²	3 RoK
1106	60,3 m ²	2 RoK
1201	34,6 m ²	1 RoK
1202	44,7 m ²	2 RoK
1203	44,7 m ²	2 RoK
1204	34,6 m ²	1 RoK
1205	71,9 m ²	3 RoK
1206	60,4 m ²	2 RoK
1301	34,6 m ²	1 RoK
1302	44,7 m ²	2 RoK
1303	44,7 m ²	2 RoK
1304	34,6 m ²	1 RoK
1305	71,7 m ²	3 RoK
1306	60,2 m ²	2 RoK
1401	66,3 m ²	3 RoK
1402	44,7 m ²	2 RoK
1403	34,6 m ²	1 RoK
1404	71,7 m ²	3 RoK
1405	60,2 m ²	2 RoK
Antal lägenheter: 1440,9 m ²		
29		

ALLMÄNNA ANVISNINGAR:

MÅTT ANGES I MILLIMETER (mm).
PLUSHÖJDER ANGES I METER (m).

FÖRKLARINGAR:

--- E160 BRANDCELLSGRÄNS

ABK ARMBÅGSKONTAKT

EL-C ELCENTRAL ENL E

(DM) FÖRBERETT FÖR DISKMASKIN

(M) FÖRBERETT FÖR MICRO

K/F KYL/FRYS

G GARDEROB

L LINNESKÅP

ST STÄDSKÅP

SKJUTDÖRRSGARDEROB

HATTHYLLA

TV

PB POSTBOX, ANTAL ANPASSAS

TRM TORKMATT

GS GLIDSKYDD

GB GÅNGBRYGGA

FÖ FÄSTÖGLA

STR STUPRÖR

UL UPPSTIGNINGSLUCKA

UTRYMNINGSSKYLT

KM KOMBIMASKIN

1 RoK

2 RoK

3 RoK

Plan	BOA	Plan	BT
PLAN 10	291,3 m ²	PLAN 09	381,7 m ²
PLAN 11	290,7 m ²	PLAN 10	383,3 m ²
PLAN 12	291,0 m ²	PLAN 11	383,3 m ²
PLAN 13	290,5 m ²	PLAN 12	383,3 m ²
PLAN 14	277,5 m ²	PLAN 13	383,3 m ²
	1440,9 m ²	PLAN 14	383,3 m ²
			2298,1 m ²

BYA INKL. BALKONGER OCH SKÄRMTAK 430,8 m².
OPA (YTA UNDER BALKONGER/SKÄRMTAK) 47,5 m².

PM01-A		2022-03-14	SG
BET	ÄNDRINGEN AVSER	DATUM	SIGN
BYGGLOVSHANDLING			
JSB VI BYGGER FÖR FLER			
 minjar			
X	A MINJAR AB	0739-10 00 98	
	K MINJAR AB	0739-10 01 14	
	VS COMFORT-KEDJAN AB	019-777 02 00	
	V VENTEX ENTREPRENAD AB	0456-135 95	
	E ETG EL-TELEGRUPPEN AB	0454-30 64 97	
	M PARK I SYD	076-645 23 05	
	G SWECO	072-212 96 62	
UPPDRAG NR 9801030		BITAD/KONSTR. AV OF	HANDLÄGGARE SG
DATUM 2021-12-22		ANSVARIG SARAH GHAZIEH	
SKEVIK 1:190, VÄRMDÖ			
BOMINI/BAS- 6-SPÄNNARE			
HUS A			
PLAN 14 & TAKPLAN			
SKALA A1	SKALA A3	NUMMER	BET
1:100	1:200	A-40-1-152	A

