



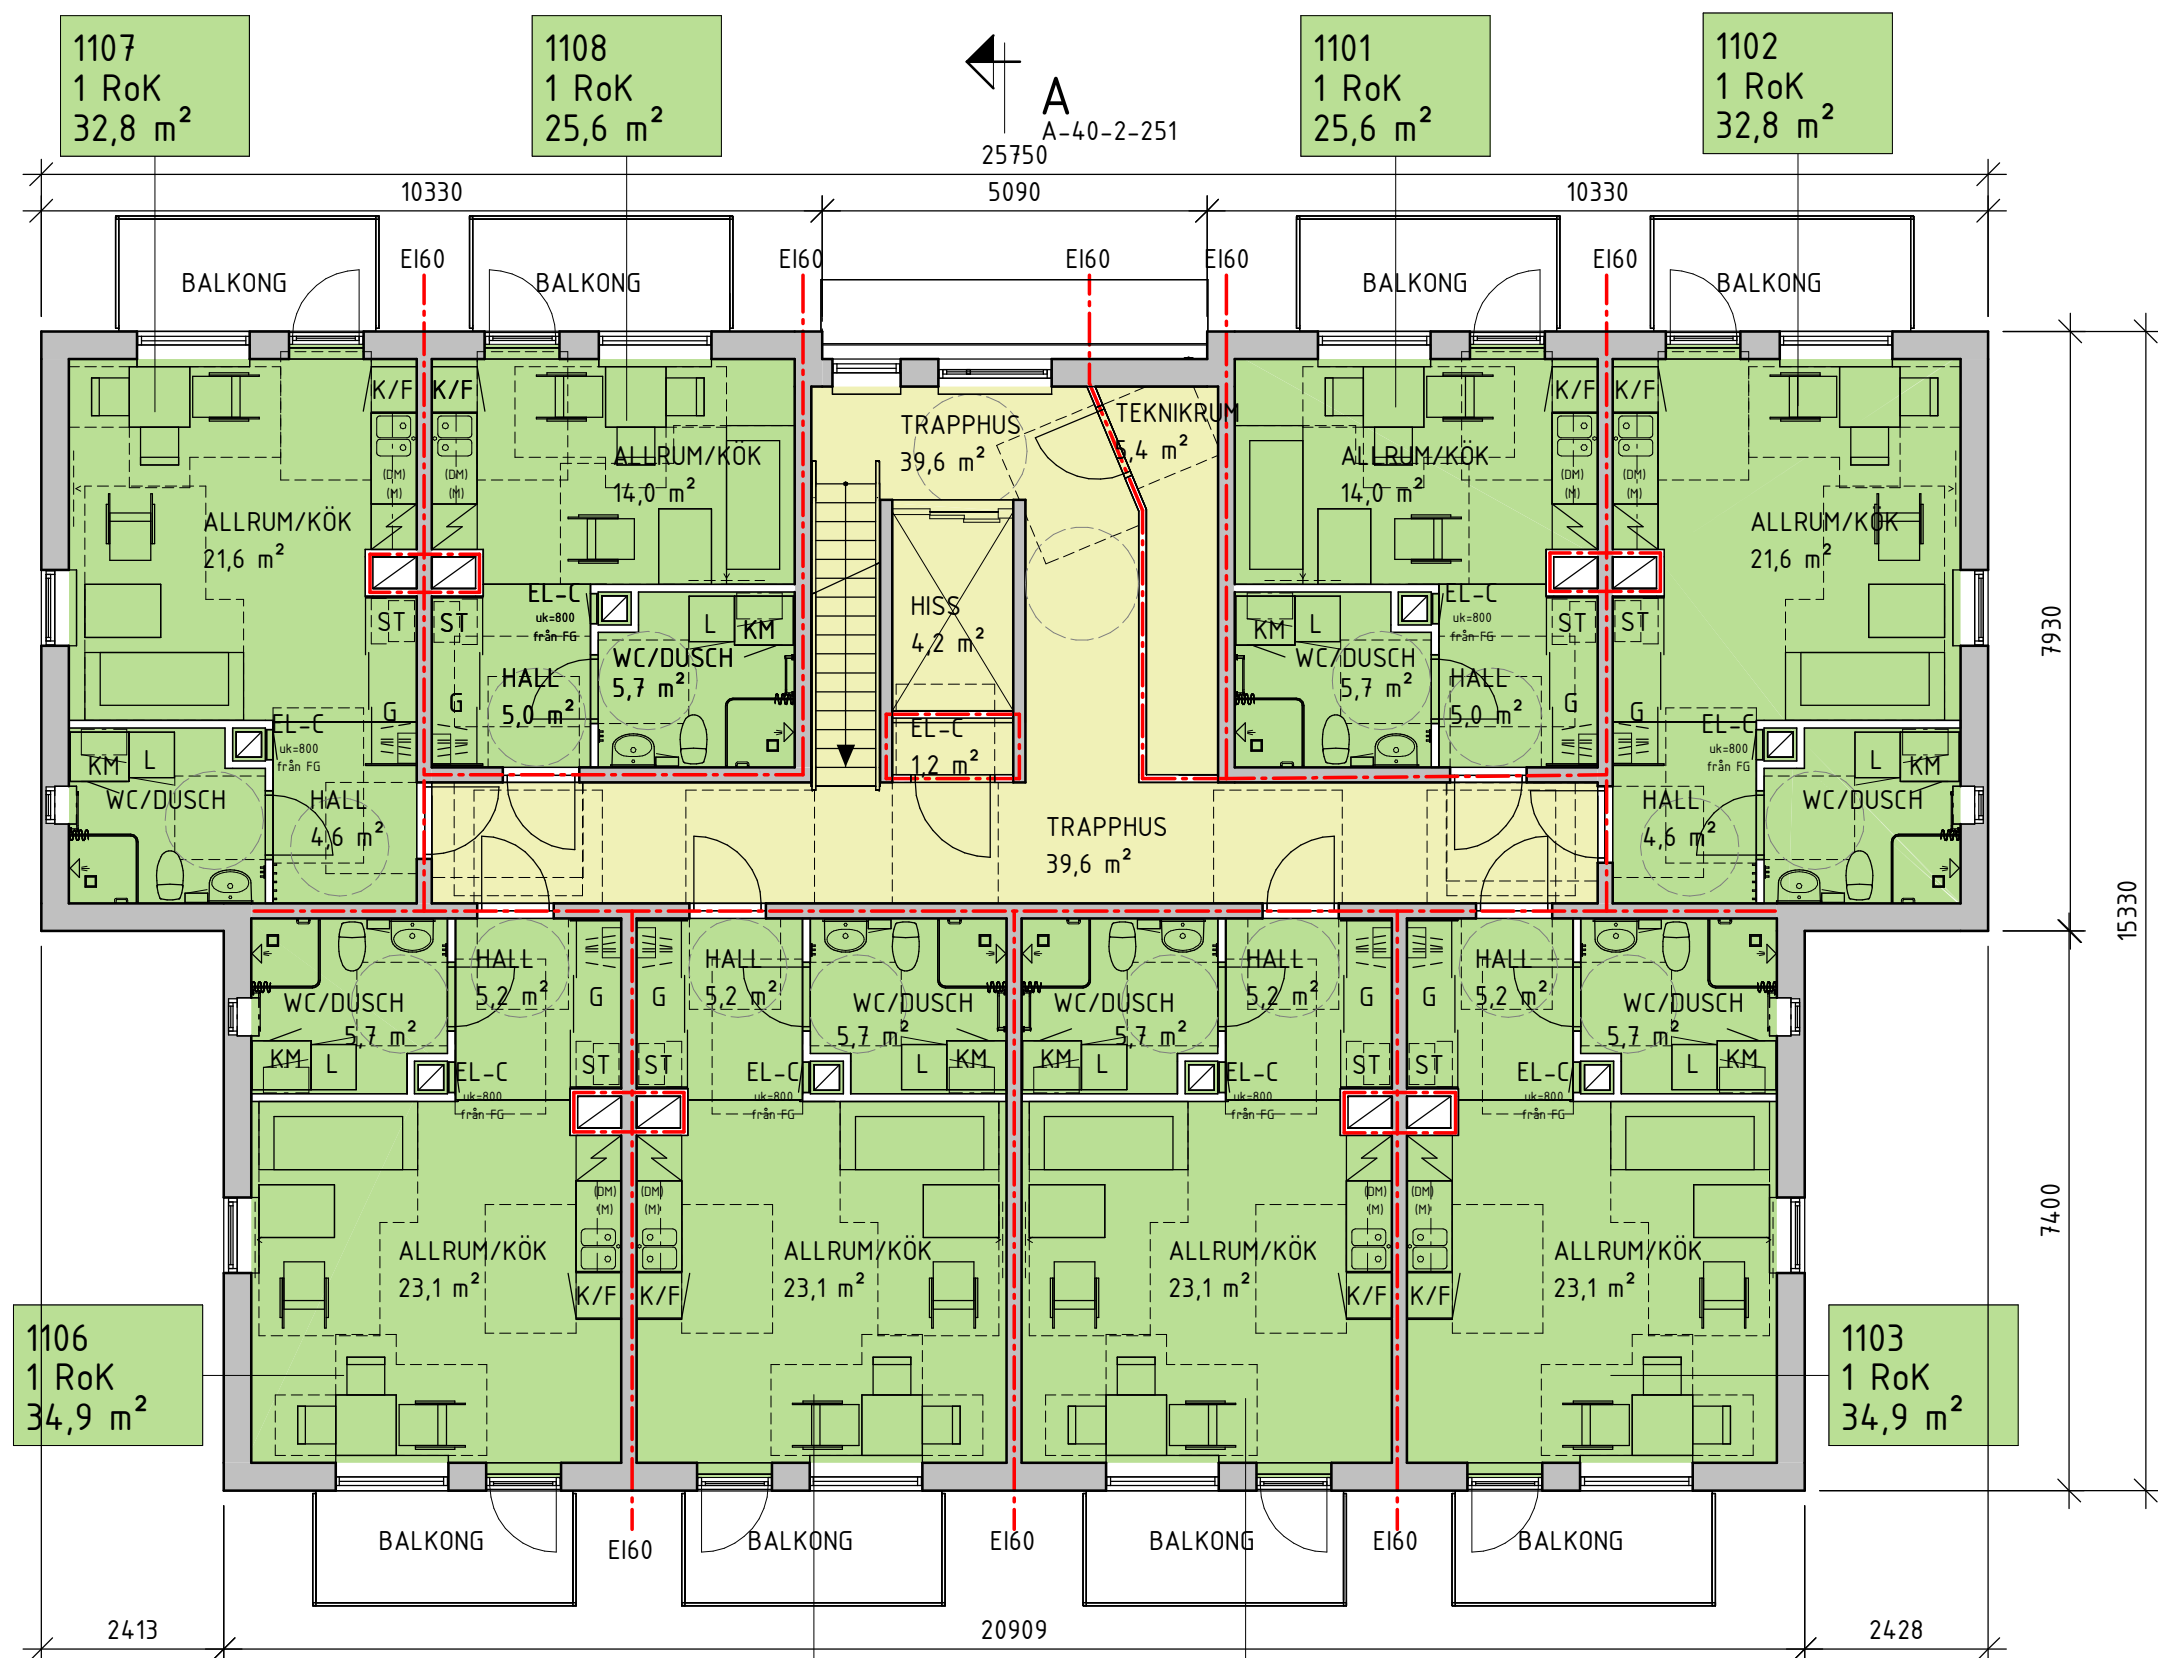


PLAN 11-13

A-40-2-251

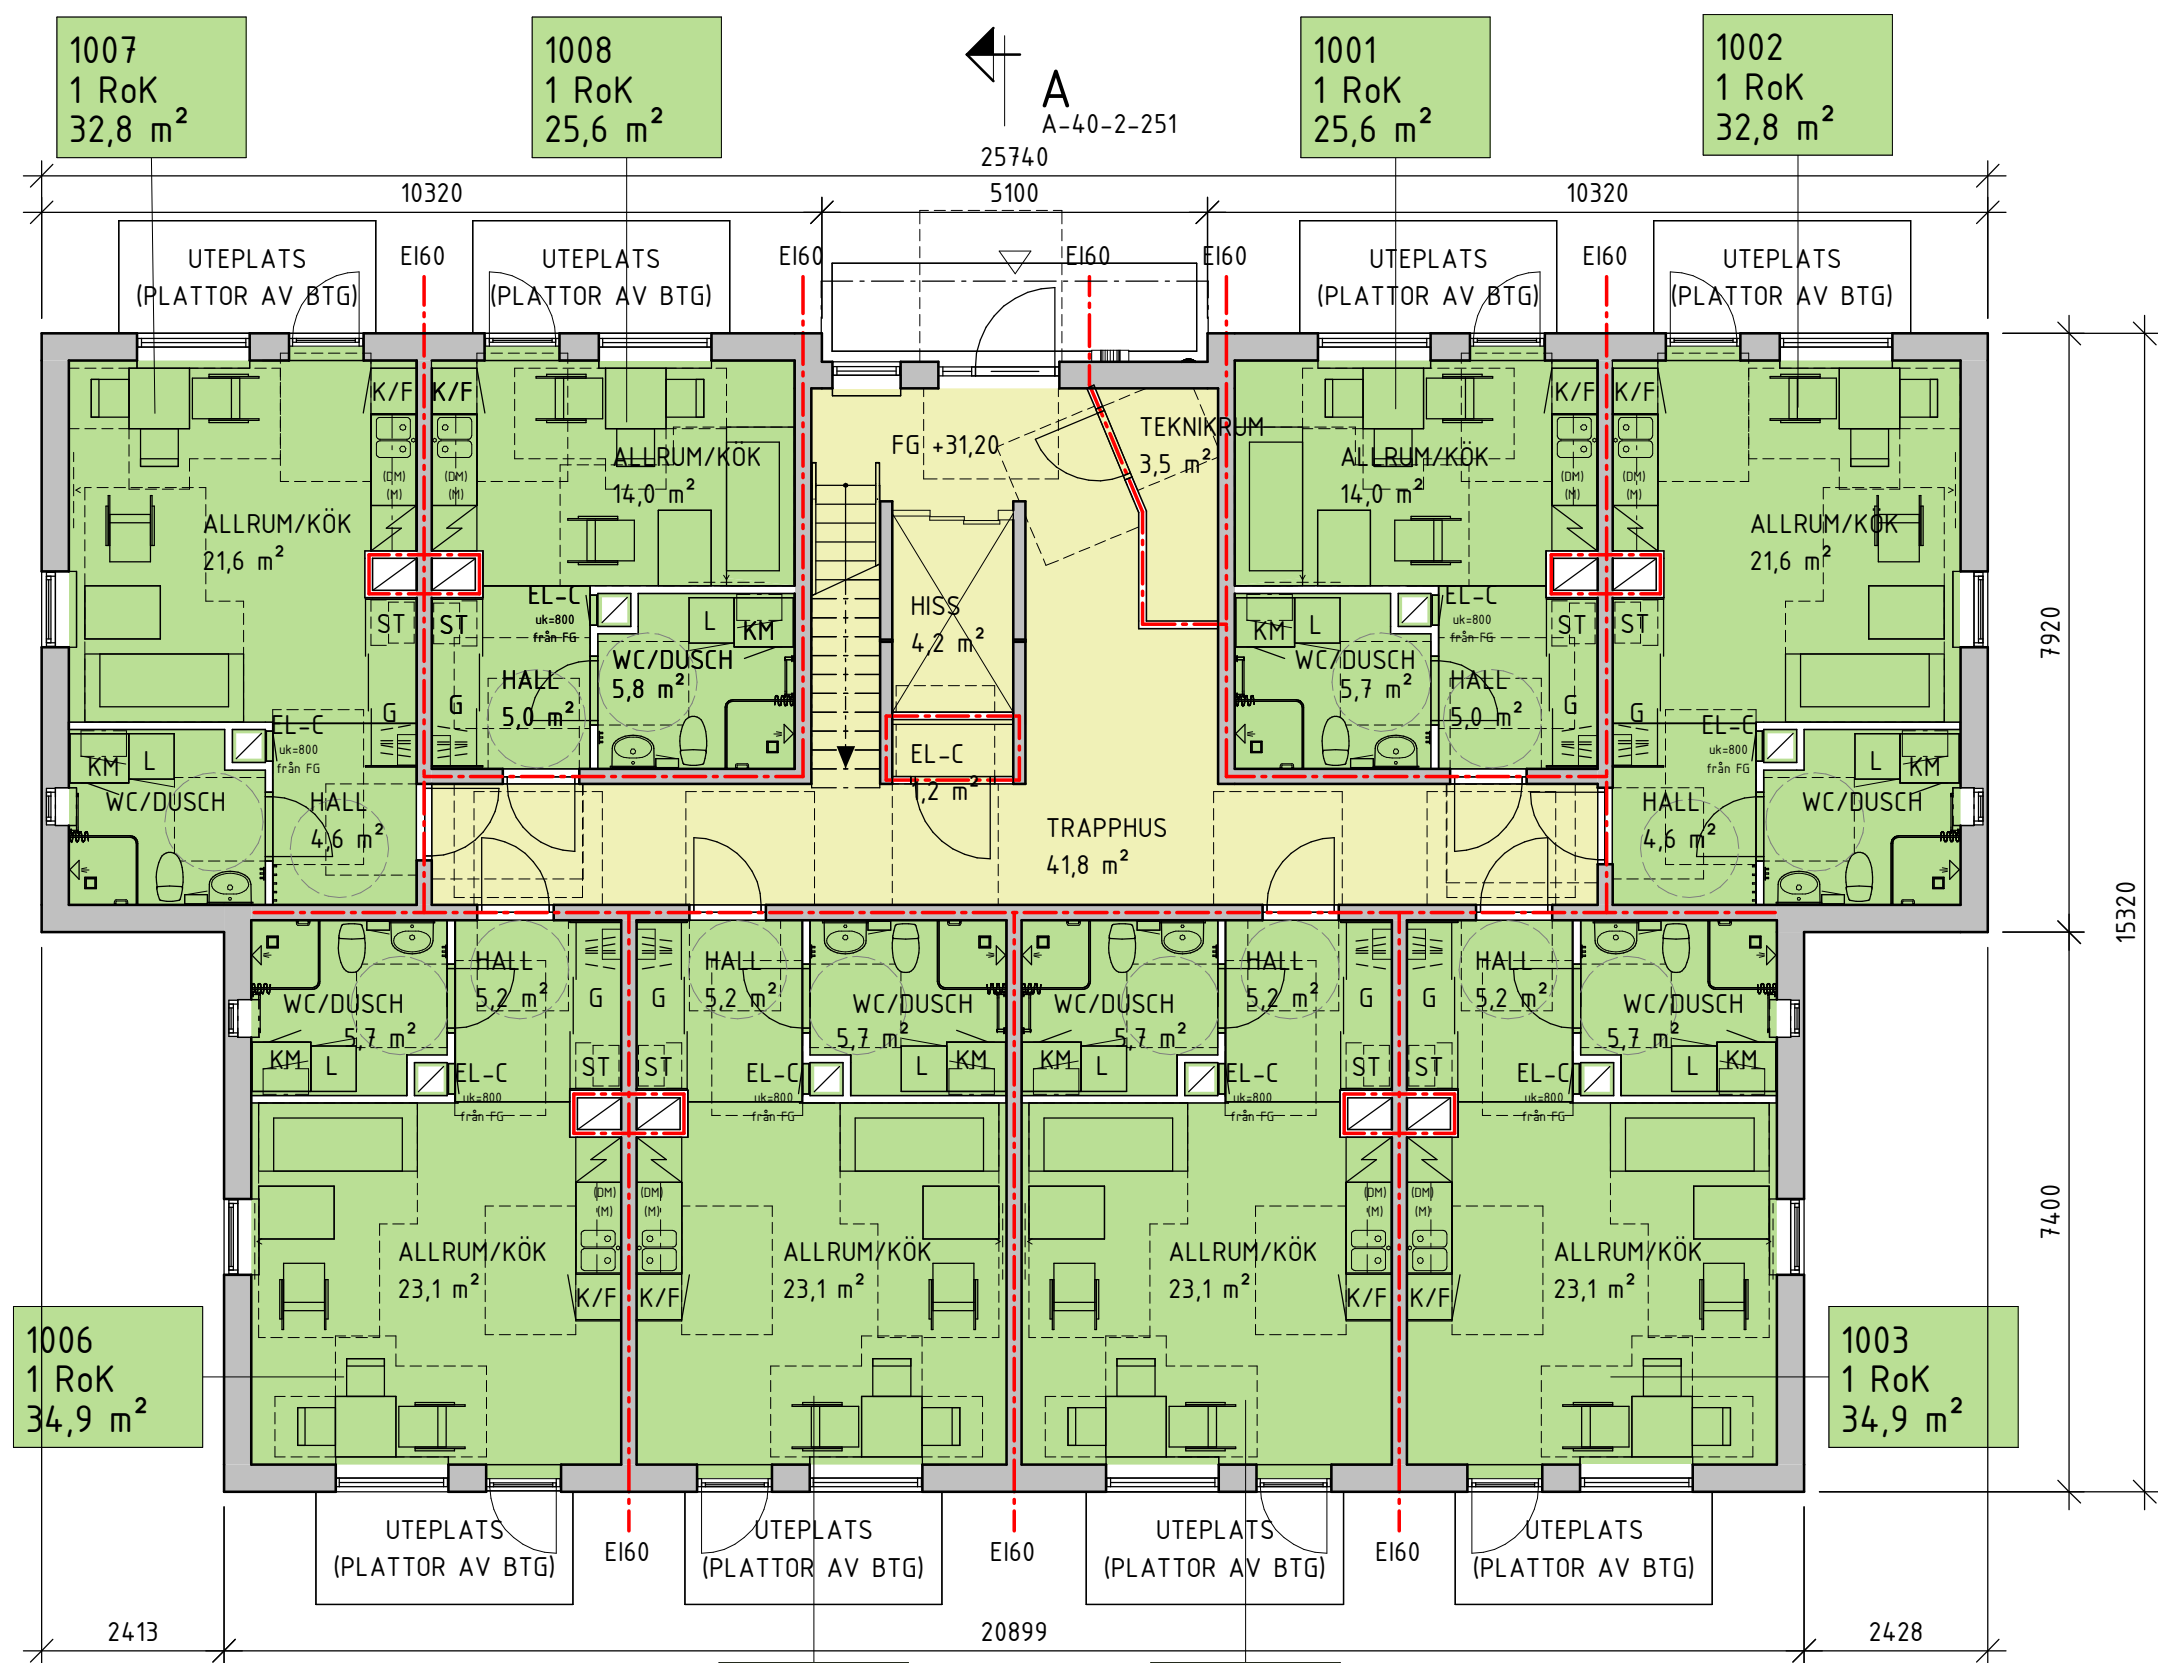


PLAN 10

A-40-2-251

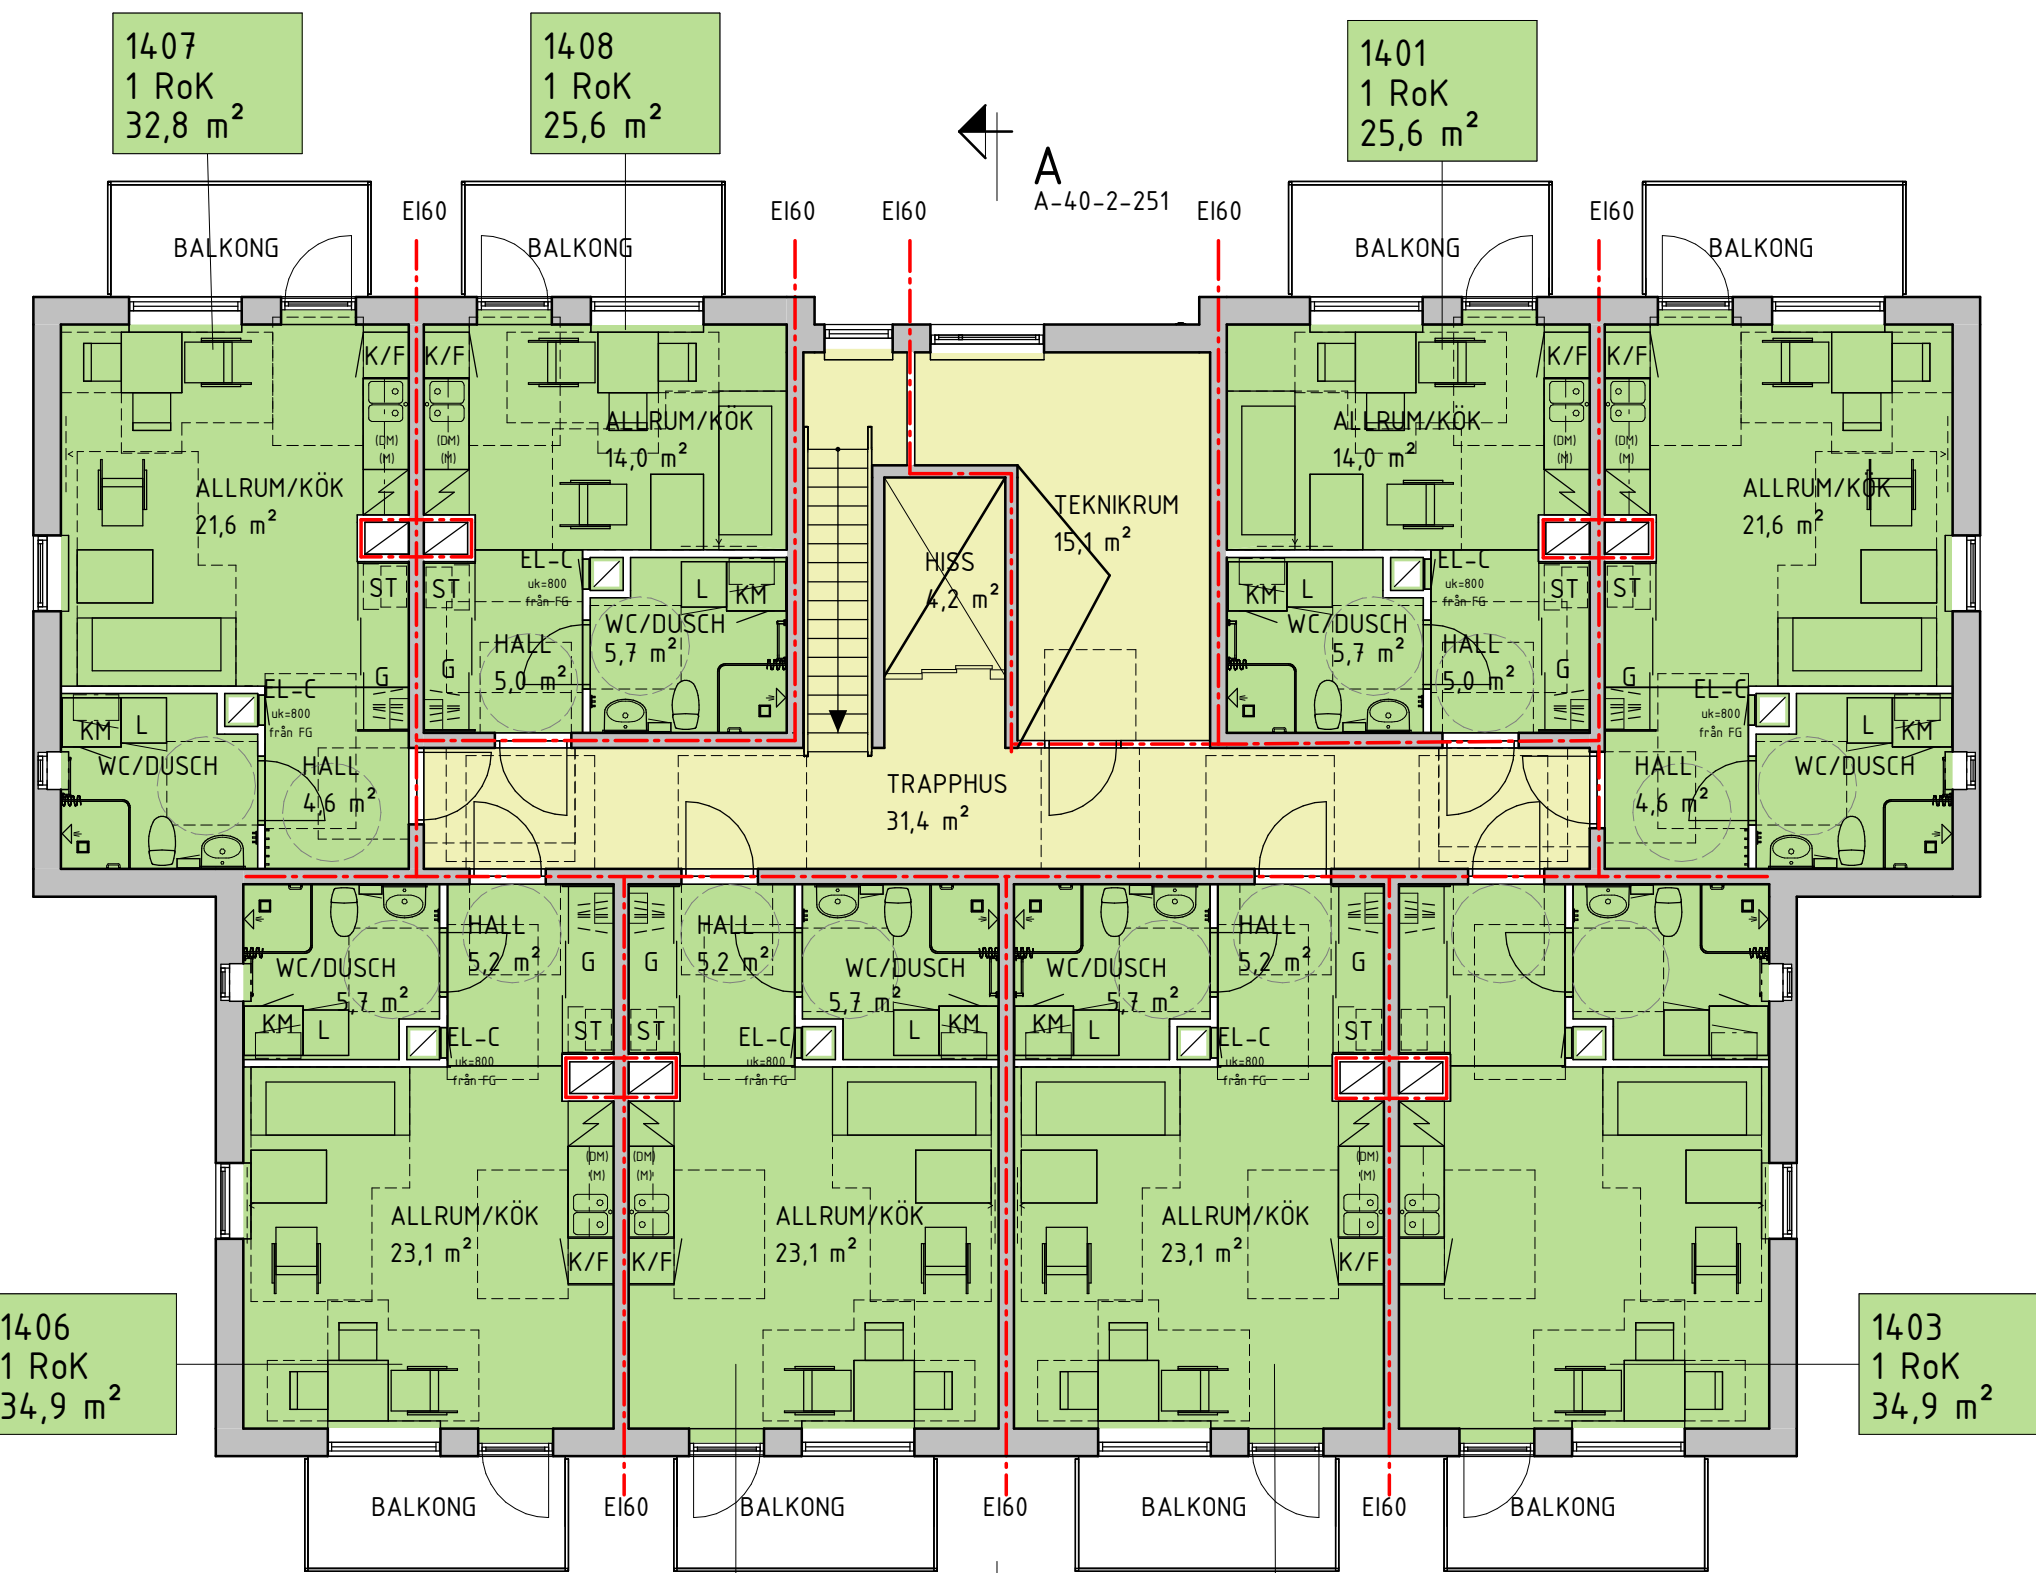

PLAN 14

A-40-2-251

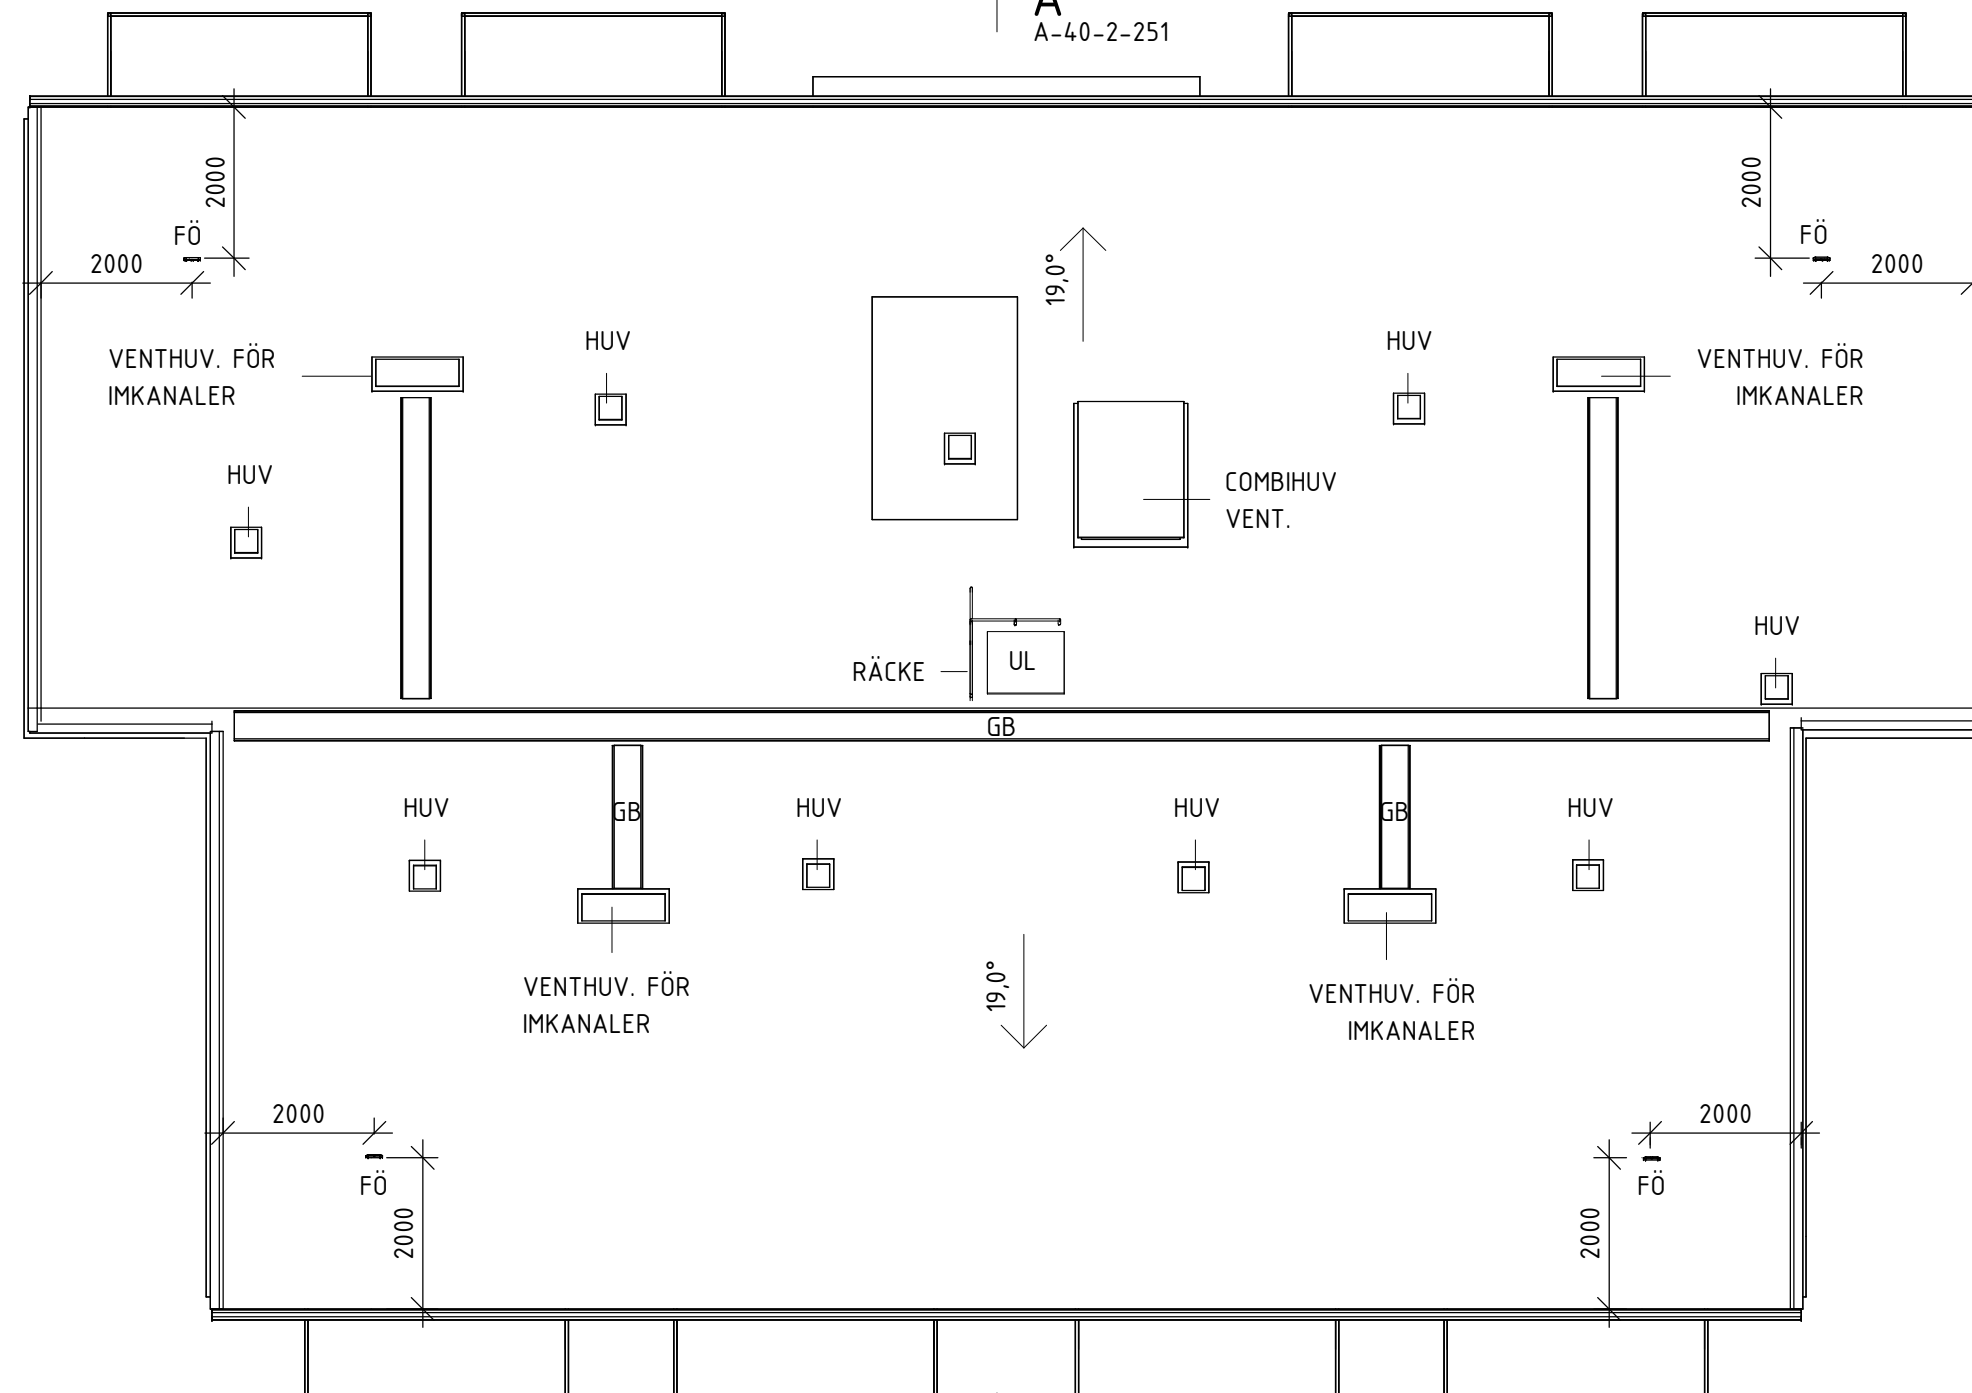

TAKPLAN

A-40-2-251

Fördelning lägenheter Hus B		
LGH-Nummer	BOA	Name

1001	25,6 m ²	1 RoK
1002	32,8 m ²	1 RoK
1003	34,9 m ²	1 RoK
1004	34,9 m ²	1 RoK
1005	34,9 m ²	1 RoK
1006	34,9 m ²	1 RoK
1007	32,8 m ²	1 RoK
1008	25,6 m ²	1 RoK

1101	25,6 m ²	1 RoK
1102	32,8 m ²	1 RoK
1103	34,9 m ²	1 RoK
1104	34,9 m ²	1 RoK
1105	34,9 m ²	1 RoK
1106	34,9 m ²	1 RoK
1107	32,8 m ²	1 RoK
1108	25,6 m ²	1 RoK

1201	25,6 m ²	1 RoK
1202	32,8 m ²	1 RoK
1203	34,9 m ²	1 RoK
1204	34,9 m ²	1 RoK
1205	34,9 m ²	1 RoK
1206	34,9 m ²	1 RoK
1207	32,8 m ²	1 RoK
1208	25,6 m ²	1 RoK

1301	25,6 m ²	1 RoK
1302	32,8 m ²	1 RoK
1303	34,9 m ²	1 RoK
1304	34,9 m ²	1 RoK
1305	34,9 m ²	1 RoK
1306	34,9 m ²	1 RoK
1307	32,8 m ²	1 RoK
1308	25,6 m ²	1 RoK

1401	25,6 m ²	1 RoK
1402	32,8 m ²	1 RoK
1403	34,9 m ²	1 RoK
1404	34,9 m ²	1 RoK
1405	34,9 m ²	1 RoK
1406	34,9 m ²	1 RoK
1407	32,8 m ²	1 RoK
1408	25,6 m ²	1 RoK

Antal lägenheter: 40
1281,4 m²

ALLMÄNNA ANVISNINGAR:

MÅTT ANGES I MILLIMETER (mm).
PLUSHÖJDER ANGES I METER (m).

FÖRKLARINGAR:

- Ei60 BRANDCELLSGRÄNS
- ABK ARMBÅGSKONTAKT
- EL-C ELCENTRAL ENL E
- (DM) FÖRBERETT FÖR DISKMASKIN
- (M) FÖRBERETT FÖR MICRO
- K/F KYL/FRYS
- G Garderob
- L LINNESKÅP
- ST STÅDSKÅP
- SKJUTDÖRRSGARDEROB
- HATTHYLLA
- TV
- PB POSTBOX, ANTAL ANPASSAS
- TRM TORKMATTA
- GS GLIDSKYDD
- GB GÅNGBRYGGA
- FÖ FÄSTÖGLA
- STR STUPRÖR
- UL UPPSTIGNINGSLUCKA
- UTRYNNINGSSKYLT
- KM KOMBIMASKIN

- 1 RoK
- 2 RoK

Plan	BOA	Plan	BTA
10	256,3 m ²	10	356,9 m ²
11	256,3 m ²	11	356,9 m ²
12	256,3 m ²	12	356,9 m ²
13	256,3 m ²	13	356,9 m ²
14	256,3 m ²	14	356,9 m ²
1281,4 m ²		1784,7 m ²	

BYA INKL. BALKONGER OCH SKÄRMTAK 402,7 m².
OPA (YTA UNDER BALKONGER/SKÄRMTAK) 45,8 m².

A	PM01-A	2022-03-14	SG
BET	ÄNDRINGEN AVSEER	DATUM	SIGN
BYGGLOVSHANDLING			
JSB VI BYGGER FÖR FLER			
X	A MINJAR AB	0739-10 01 05	
	K MINJAR AB	0739-10 01 14	
	VS COMFORT-KEDJAN AB	019-777 02 00	
	V VENTEX ENTREPRENAD AB	0456-135 95	
	E ETG EL-TELEGRUPPEN AB	0454-30 64 97	
	M MARK-KONSUKT	XXXXXXXXXX	
	G GEO-KONSULT	XXXXXXXXXX	
UPPDRAGS NR	9801030	REDAKONSTR. AV	SG
DATUM	2021-12-22	ANSVARIG	SARAH GHAZIEH
SKEVIK 1:190, VÄRMDÖ STUDENTBOENDE HUS B - 5 VÅN. PLANER, PLAN 10-14 samt TAKPLAN			
SKALA A1	SKALA A3	NUMMER	BET
1:100	1:200	A-40-1-251	A