

ALLMÄNNA ANVISNINGAR:

MÅTT ANGES I MILLIMETER (mm).
PLUSHÖJDER ANGES I METER (m).

FÖRKLARINGAR:

E160 BRANDCELLSGRÄNS

ABK ARMBÄGSKONTAKT


STR STUPRÖR

INGÅENDE MATERIAL OCH KULÖRER LITTRERAS MED
LÖPNUMMER ENLIGT TABELL.


- 1 GRÅ BETONGSOCKEL
- 2 SEDUMTAK
- 3 TRÄ, STÄNDE FALSAD SPÅRPANEL MED
FASADE KANTER MÅLAS KULÖR RÖD NCS
S 4040-Y60R, TEGELRÖD
- 4 HÄNGRÄNNOR + STUPRÖR AV PLÅT -
KULÖR GRÅ
- 5 ALUMINIUMKLÄDDA
TRÄFÖNSTER/FÖNSTERDÖRRAR,
FABRIKSLACKARAD KULÖR:
UTV. - RAL 7004
INV. - NCS S 0502-Y
- 6 PLÅTAVTÄCKNING, GRÅ
- 7 DÖRR STÅL, FABRIKSLACKARAD, KULÖR
RAL 7004

PLÅT
ALL PLÅT UTOM TRÖSKELPLÅT SKA VARA AV
ALUMINIUMPLÅT.


FÖNSTERBLECK, FÖNSTEROMFATTNINGAR SAMT
DÖRROMFATTNINGAR SKA UTFÖRAS I SAMMA
KULÖR SOM TILLHÖRANDE ENHET.

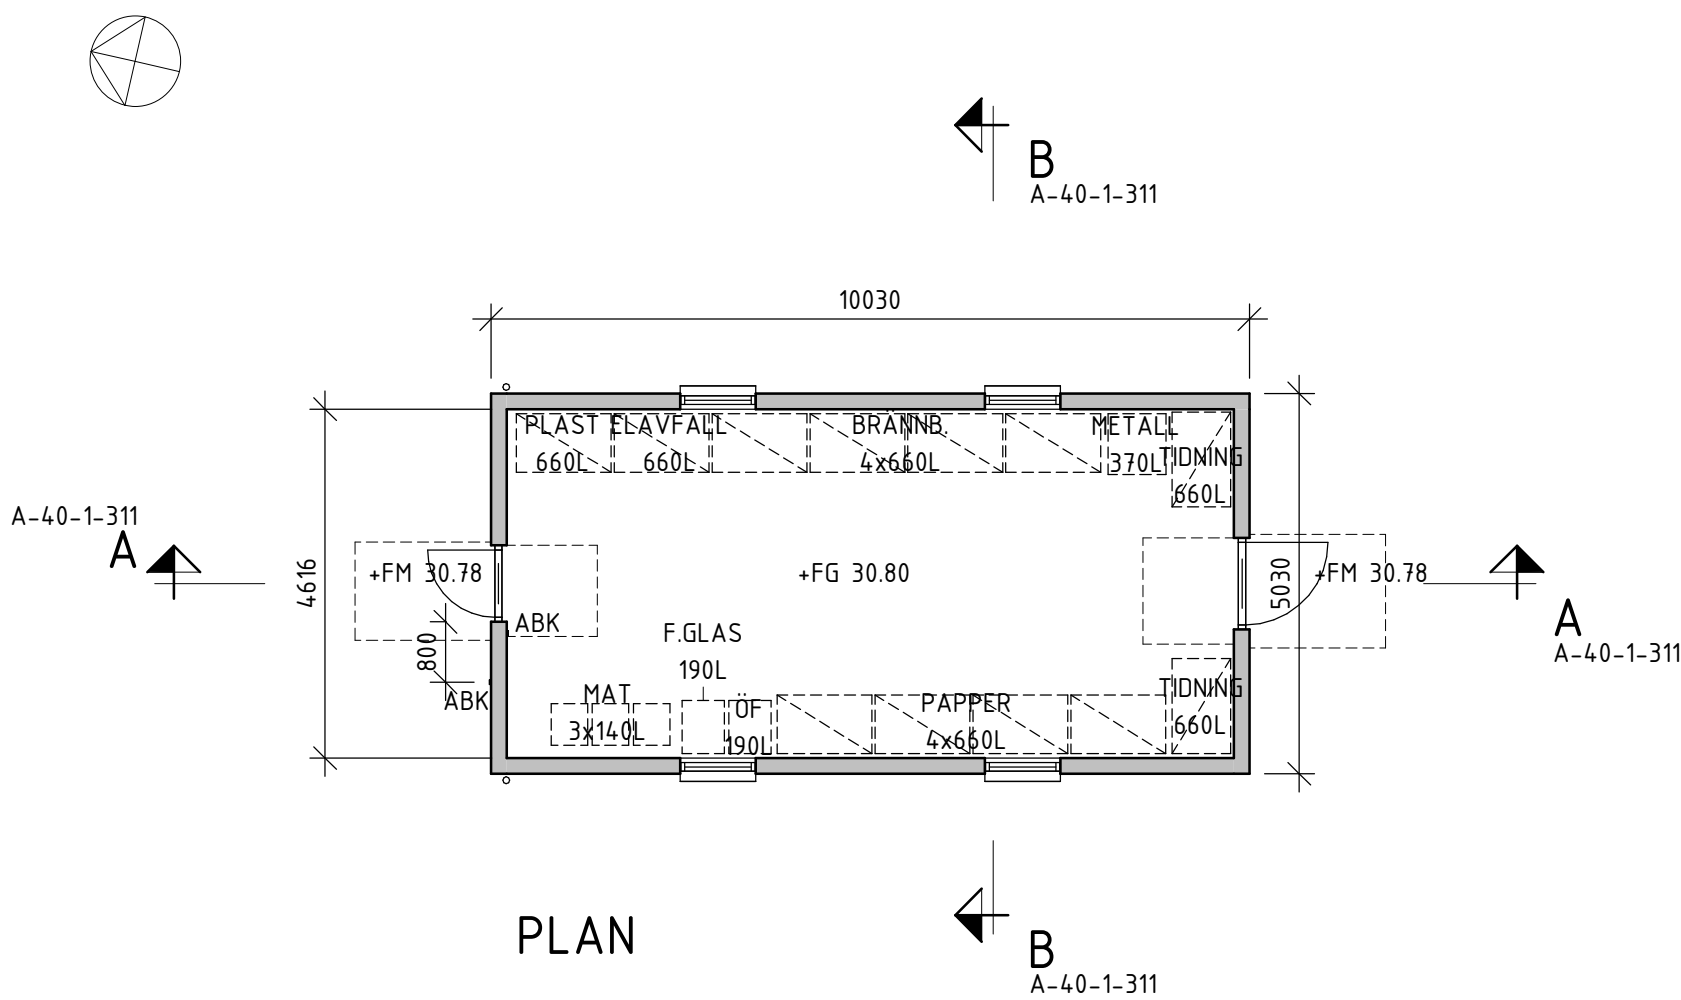


PLAN

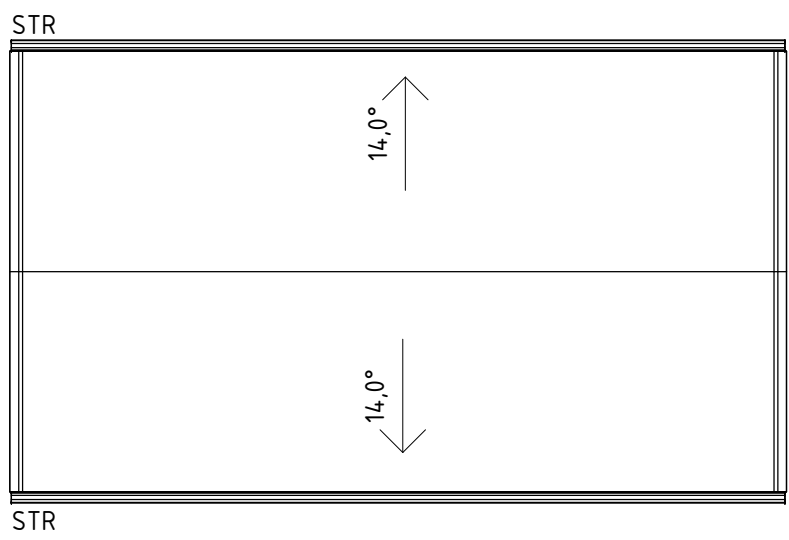


TAKPLAN

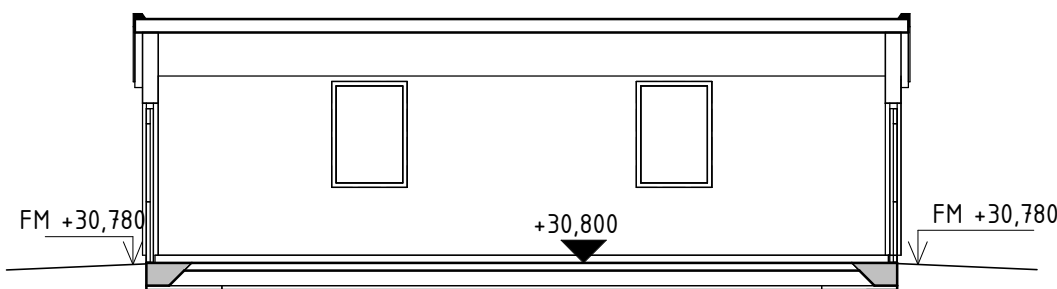


PRINCIPSEKTION A-A

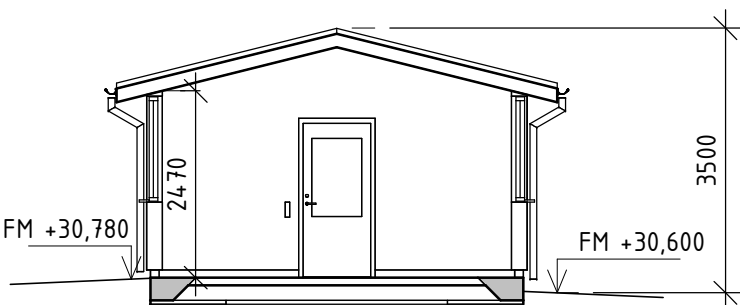


PRINCIPSEKTION B-B

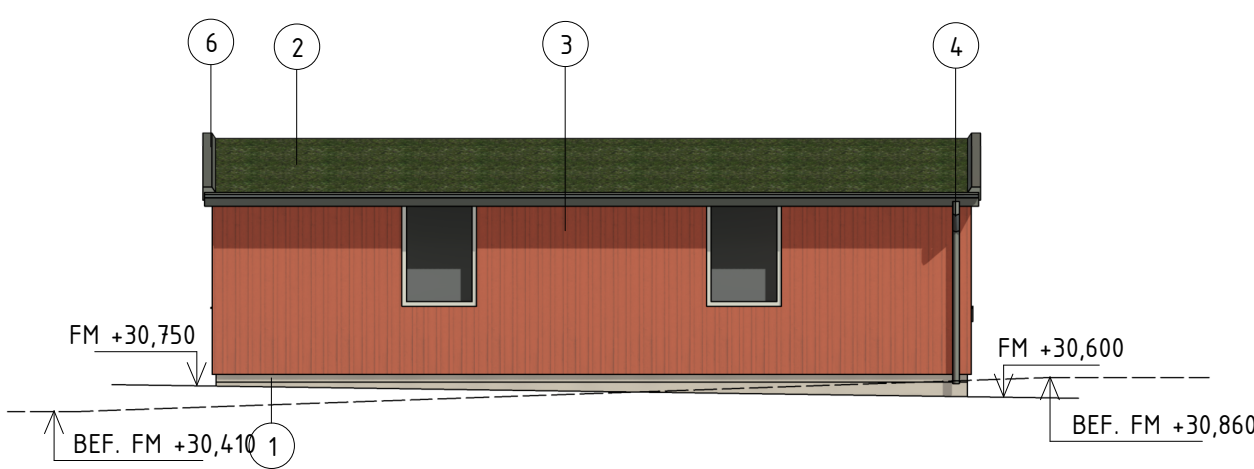


FASAD MOT ÖSTER

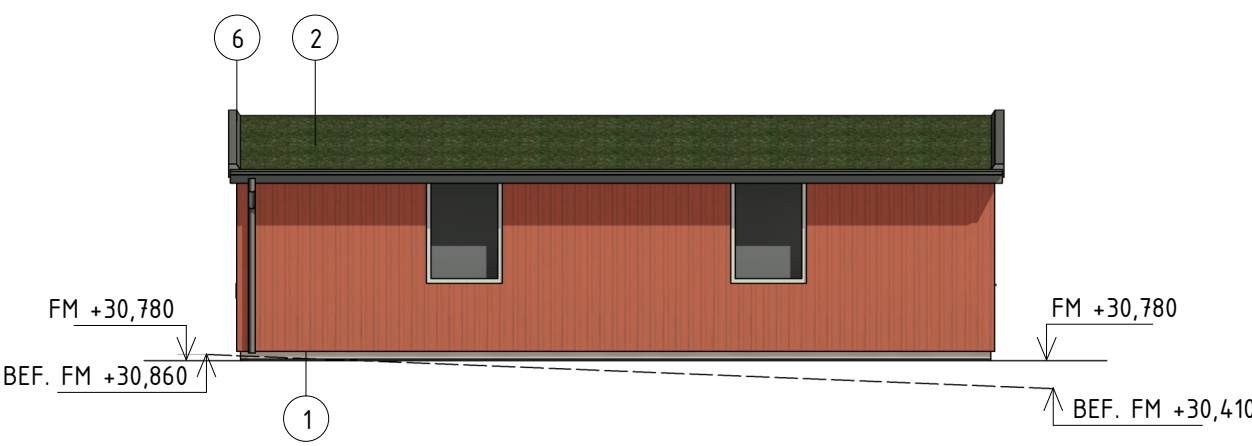

FASAD MOT VÄSTER

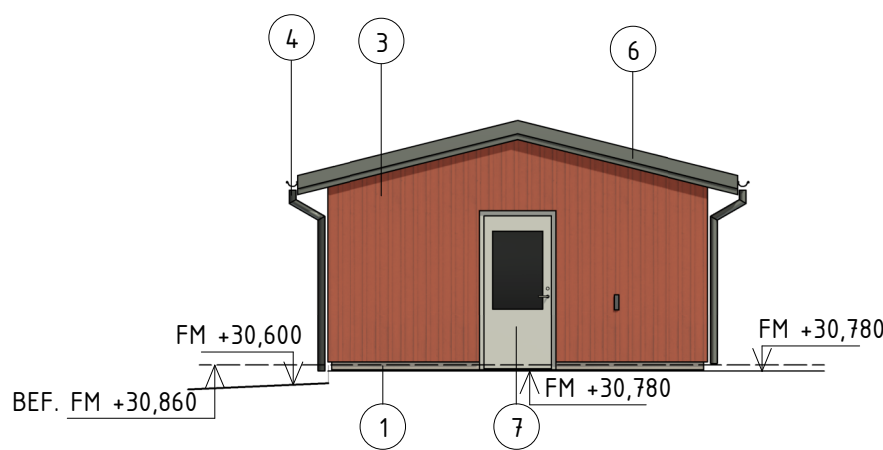


FASAD MOT NORR

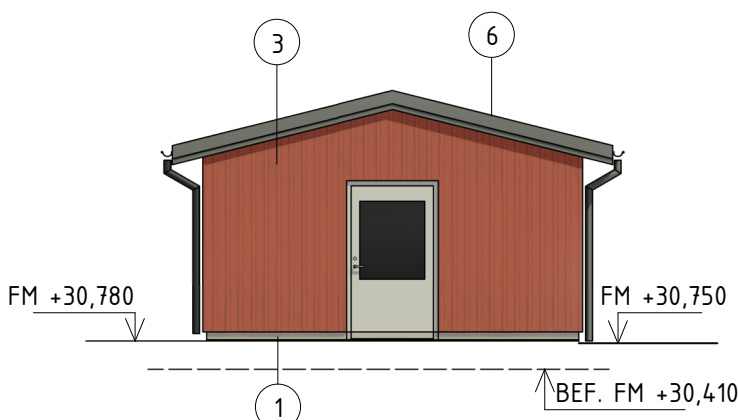

FASAD MOT SÖDER

A	PM01-A	2022-03-14	SG
BET	ÄNDRINGEN AVSER	DATUM	SIGN
BYGGLOVSHANDLING			
X	A MINJAR AB	0739-10 01 05	
	K MINJAR AB	0739-10 01 14	
	VS COMFORT-KEDJAN AB	019-777 02 00	
	V VENTEX ENTREPRENAD AB	0456-135 95	
	E ETG EL-TELEGRUPPEN AB	0454-30 64 97	
	M MARK-KONSUKT	XXXXXXXXXX	
	G GEO-KONSULT	XXXXXXXXXX	
UPPDRAGS NR	RITAD/KONSTR. AV	HANDLÄGGARE	
9801030	SG	SG	
DATUM	ANSVARIG		
2021-12-22	SARAH GHAZIEH		
SKEVIK 1:190, VÄRMDÖ KOMPLEMENTBYGGNAD HUS C - 1 PLANER			
SKALA A1	SKALA A3	NUMMER	BET
1:100	1:200	A-40-1-311	A

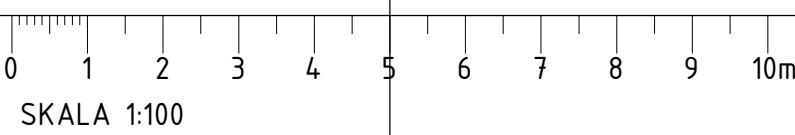

SKALA 1:100