


ALLMÄNNA ANVISNINGAR:


MÅTT ANGES I MILLIMETER (mm).
PLUSHÖJDER ANGES I METER (m).

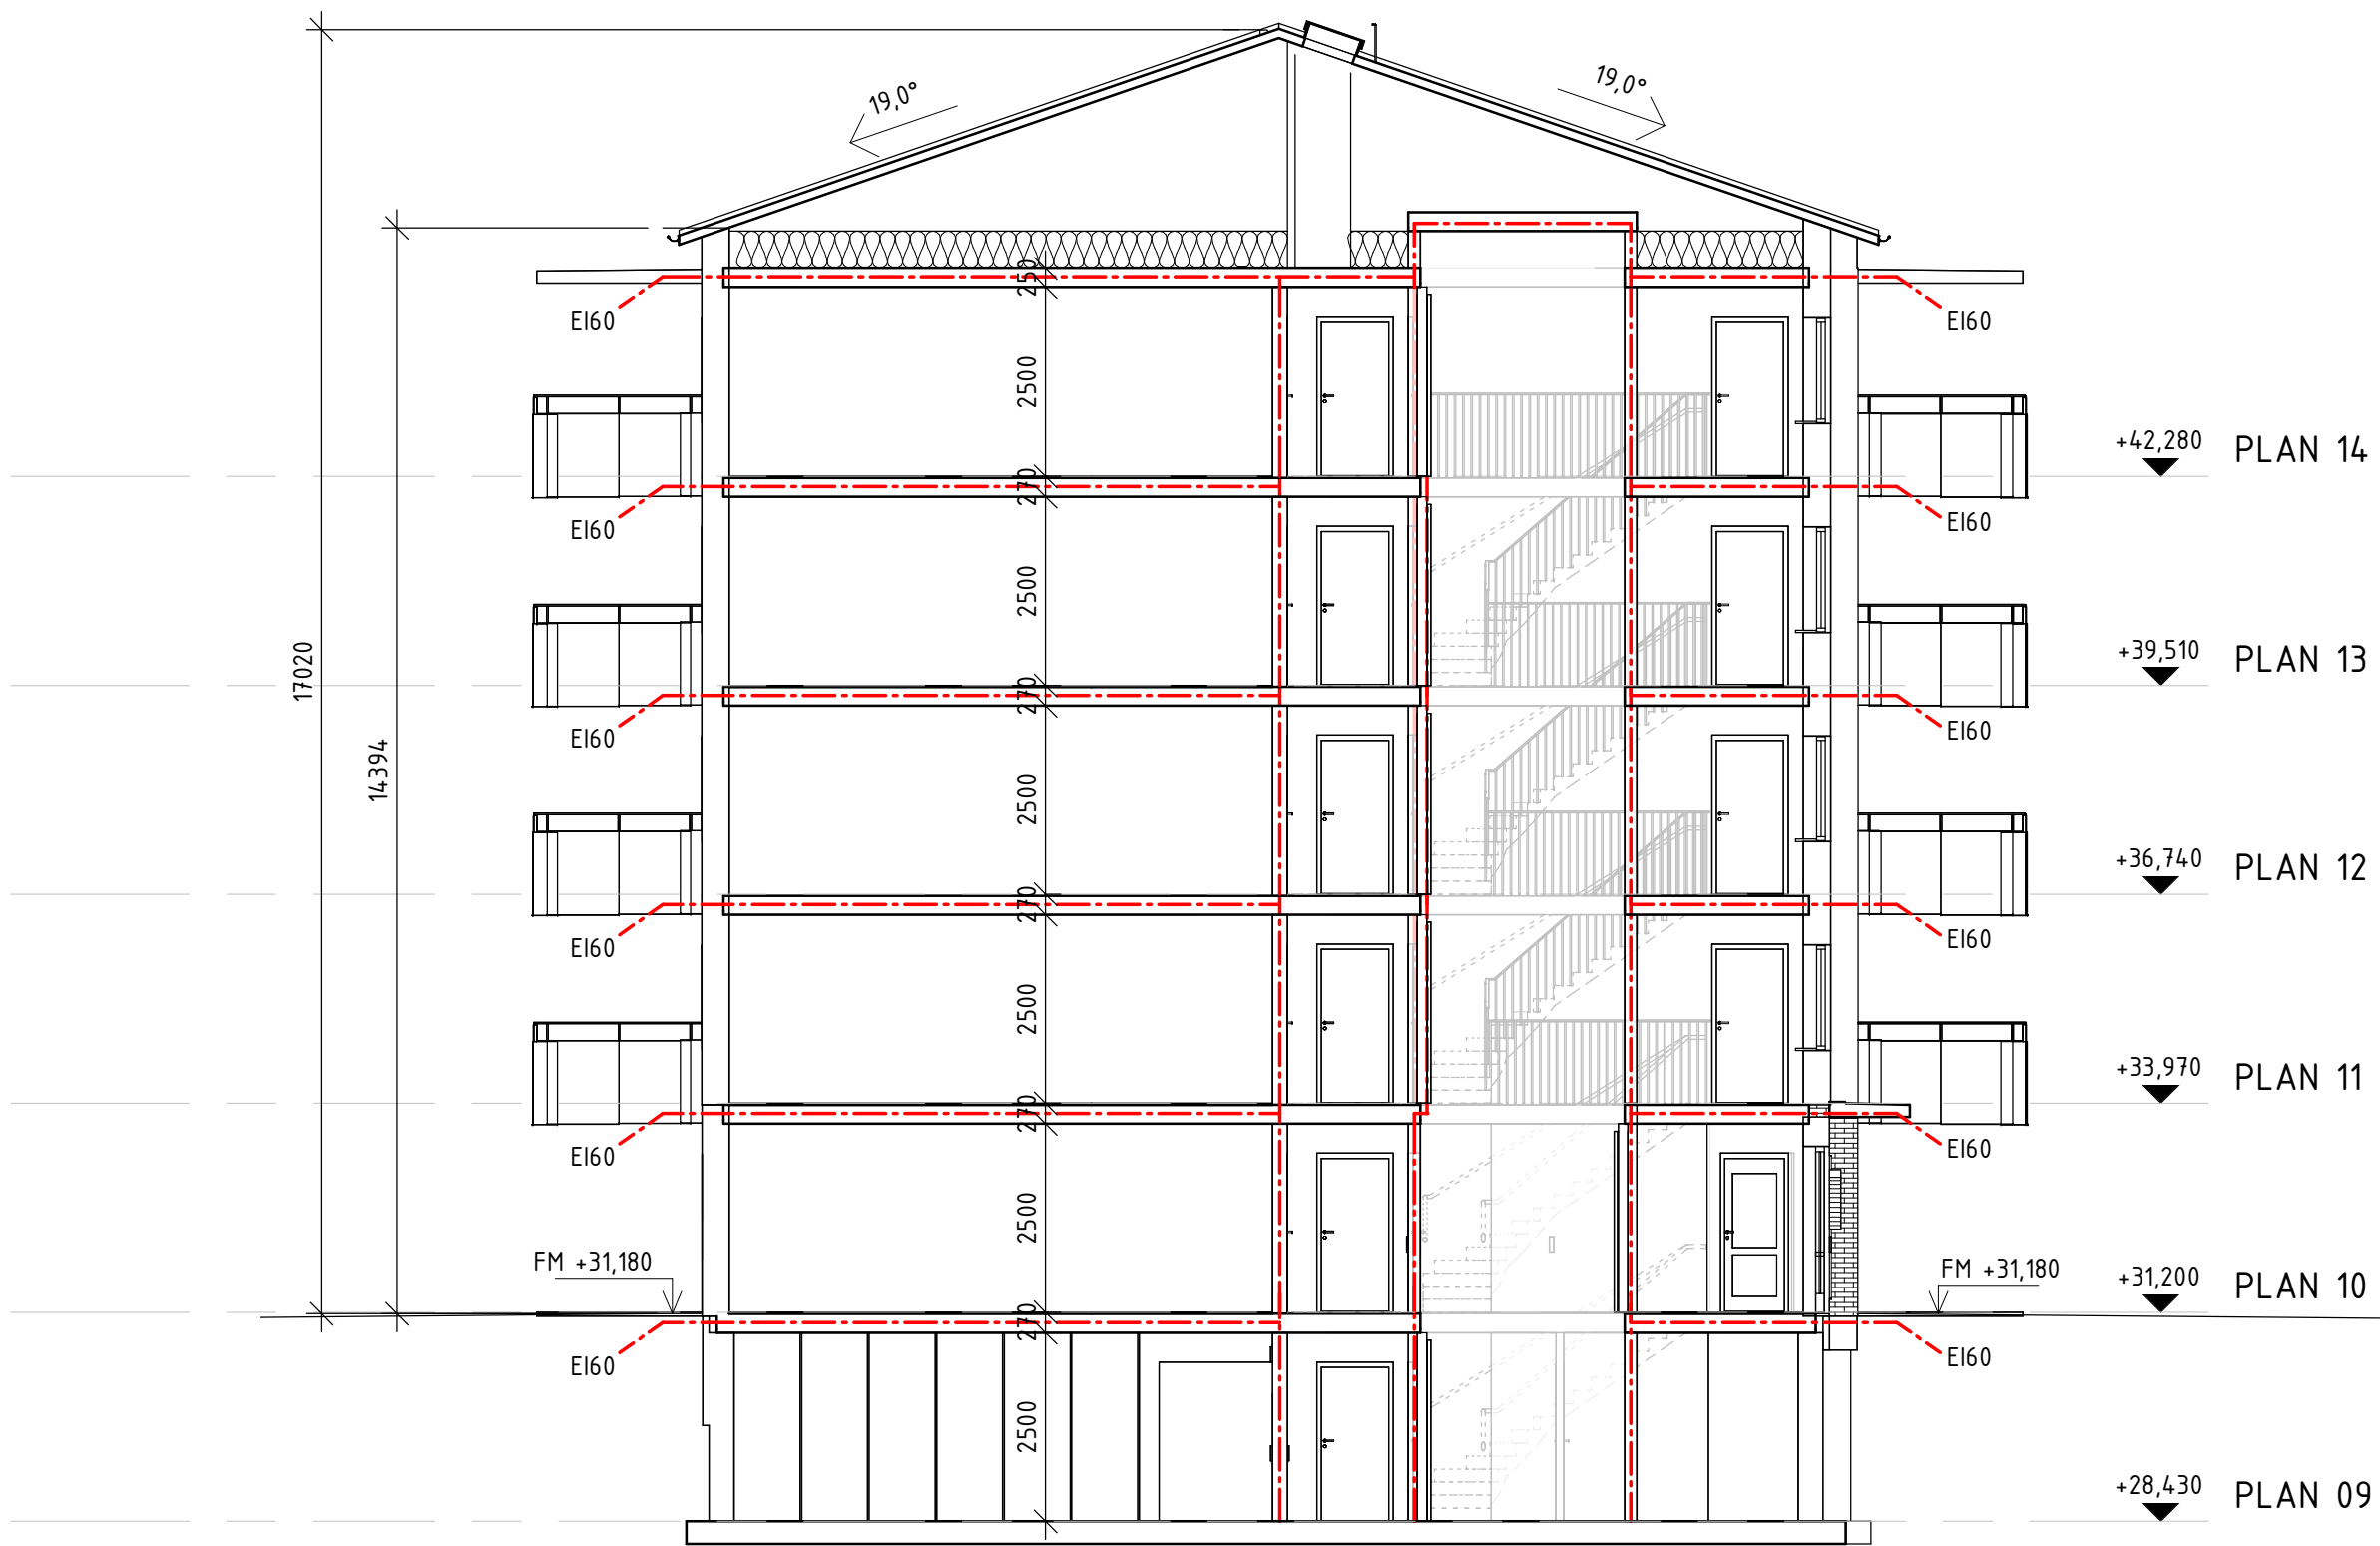

SEKTION A-A



SEKTION B-B

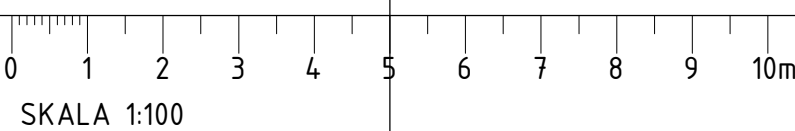

ÄNDRINGEN AVSER

DATUM

SIGN

BYGGLOVSHANDLING

JSB

VI BYGGER
FÖR FLER



minjar

X	A MINJAR AB	0739-10 00 98	
K	MINJAR AB	0739-10 01 14	
VS	COMFORT-KEDJAN AB	019-777 02 00	
V	VENTEX ENTREPRENAD AB	0456-135 95	
E	ETG EL-TELEGRUPPEN AB	0454-30 64 97	
M	XXXXXXXX		
G	GEO-KONSULT	XXXXXXXXXX	
UPPDRAGS NR	RITAD/KONSTR. AV	HANDLÄGGARE	
9801030	OF	SG	
DATUM	ANSVARIG		
2021-12-22	SARAH GHAZIEH		
SKEVIK 1:190, VÄRMDÖ			
BOMINI/BAS- 6-SPÄNNARE			
HUS A			
SEKTIONER			
SKALA A1	SKALA A3	NUMMER	BET
1:100	1:200	A-40-2-151	