
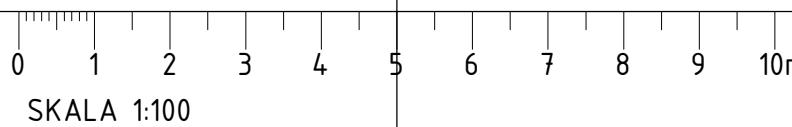


ALLMÄNNA ANVISNINGAR:

MÅTT ANGES I MILLIMETER (mm).
PLUSHÖJDER ANGES I METER (m).

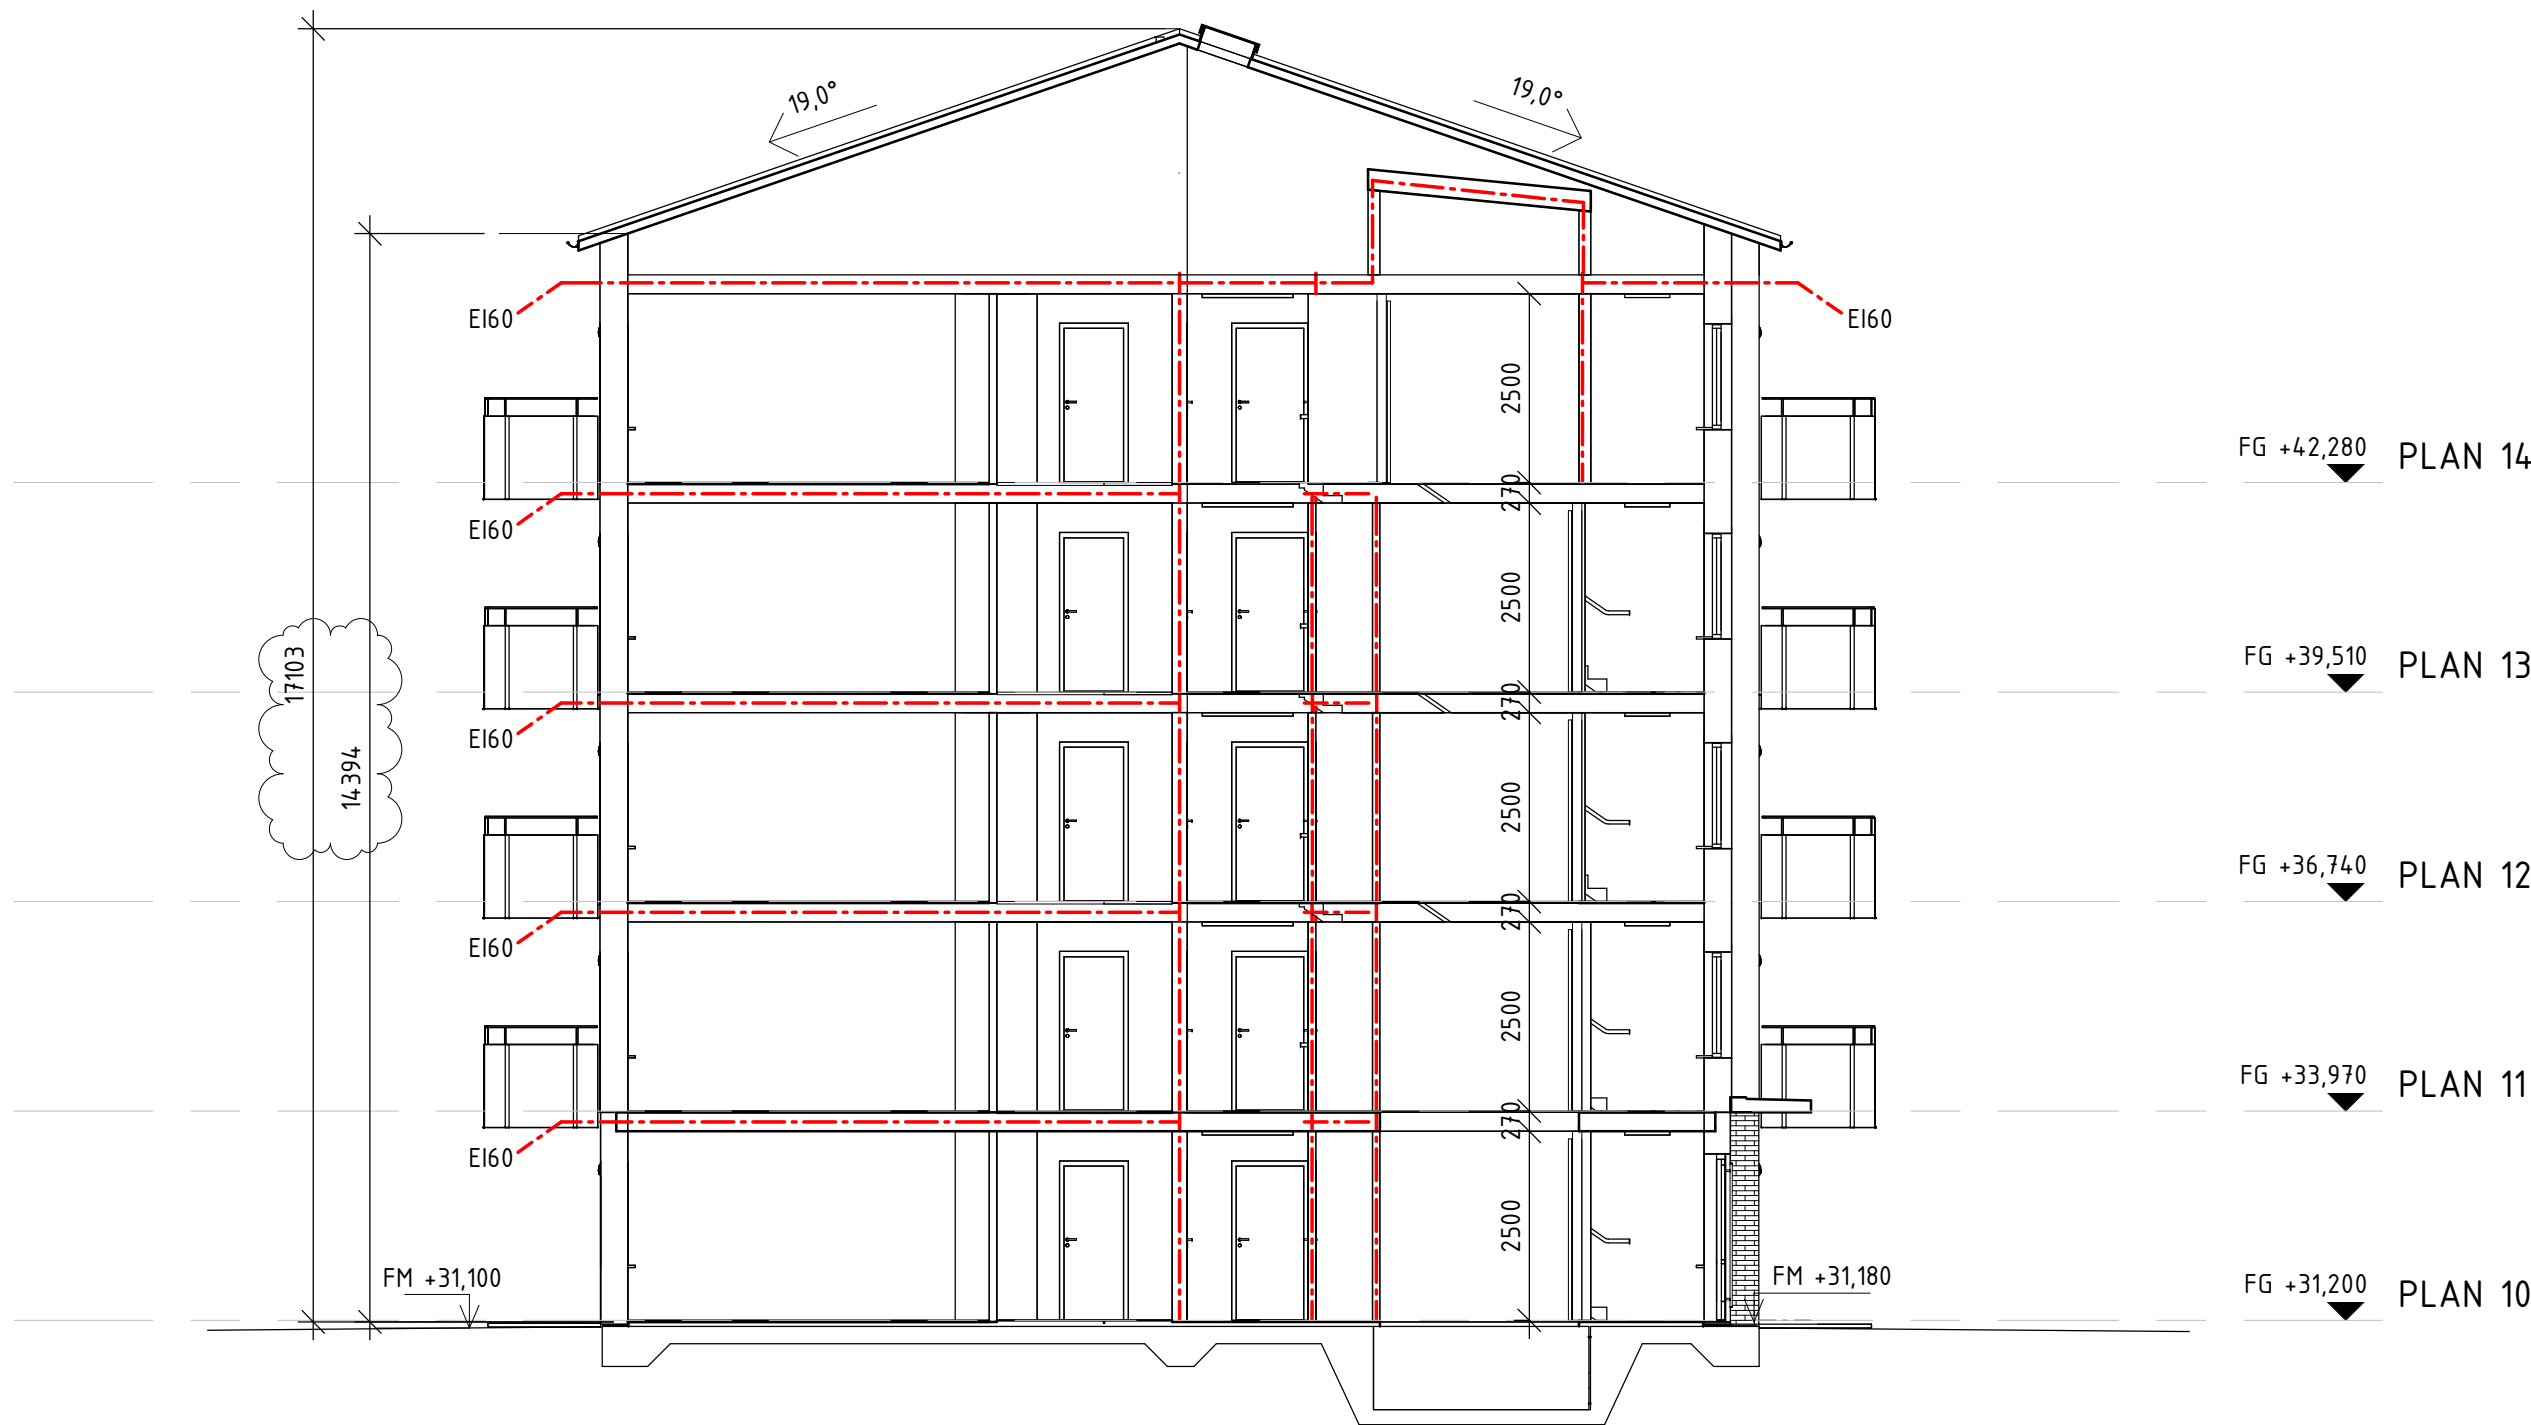

PM01-A		2022-03-14	SG		
BET	ÄNDRINGEN AVSER	DATUM	SG		
BYGGLOVSHANDLING					
JSB VI BYGGER FÖR FLER					
MINJAR minjar					
☒	A	MINJAR AB	0739-10 01 05		
☐	K	MINJAR AB	0739-10 01 14		
☐	VS	COMFORT-KEDJAN AB	019-777 02 00		
☐	V	VENTEX ENTREPRENAD AB	0456-135 95		
☐	E	ETG EL-TELEGRUPPEN AB	0454-30 64 97		
☐	M	MARK-KONSUKT	XXXXXXXXXX		
☐	G	GEO-KONSULT	XXXXXXXXXX		
UPPRORAG NR	RIITADIKONSTR. AV	HANDLÄGGARE			
9801030	SG	SG			
DATUM	ANSVARIG				
2021-12-22	SARAH GHAZIEH				
SKEVIK 1:190, VÄRMDÖ					
STUDENTBOENDE					
HUS B - 5 VÅN.					
SEKTION					
SKALA A1	SKALA A3	NUMMER	BET		
1:100	1:200	A-40-2-251	A		