

ALLMÄNNA ANVISNINGAR:

KOORDINATSYSTEM SWREF
HÖJDSYSTEM RH2000

DENNA RITNING LÄSES IHOP MED PLANRITNINGAR.
MÅTT ANGES I MILLIMETER (mm).
PLUSHÖJDER ANGES I METER (m).

FÖRKLARINGAR:


INGÅENDE MATERIAL OCH KULÖRER LITTRERAS MED
LÖPNUMMER ENLIGT TABELL.

FÖNSTERBLECK, FÖNSTEROMFATTNINGAR SAMT
DÖRRUMFATTNINGAR SKA UTFÖRAS I SAMMA KULÖR SOM
TILLHÖRANDE ENHET.

- 1 SOCKEL: BETONGSOCKEL
- 2 BRICKSTEN, MELDORFER, SKIFTANDE FÄRG
LJUSGRÅ, FOG STANDARD CEMENTGRÅ
- 2a PUTSAD FOGFRI FASAD, KULÖR TEGELRÖD,
NCS S 4040-Y60R
- 3 FÖNSTER: ALUMINIUMKLÄTT TRÄ/ALUMINIUM,
FABRIKSLACKERAD KULÖR:
UTV. - SIGNALGRÅ RAL 7004
INV. - VIT NCS S 0502-Y
- 4 ENTRÉPARTIER, GLASADE: ALUMINIUM,
FABRIKSLACKERAD KULÖR: SIGNALGRÅ RAL
7004, TÄCKPLÅTAR LIKA PARTI
- 5 FLÄKTHUVAR, AVLÜFTSDON: GALVANISERAD
STÅL, OBEHANDLAD
- 6 TAKSÄKERHET: STÅL, VARMFÖRZINKAT
- 7 TAKBELÄGGNING: TAKPAPP, SVART
- 8 TAKAVVÄTTNING: HÄNGRÄNNOR + STUPRÖR
AV PLÅT - ZINKGRÅ RAL 9007
- 9 PLÅTAVTÄCKNING: ZINKGRÅ RAL 9007
- 10 VENT.GALLER: LACKERAD, GRÅ
- 11 RÄCKE: ALUMINIUM,
KULÖR RAL 7024
- 11a BALKONGRÄCKE: LAMINAT,
KULÖR NCS S 2005-Y20R
- 12 TAKLUCKA: PLÅT, ZINKGRÅ RAL 9007
- 13 VERTIKAL TRÄPANEL VID ENTRÉNISCH,
TÄCKMÅLAD, KULÖR HAVREGUL NCS S
3020-Y20R



FASAD MOT SYDVÄST

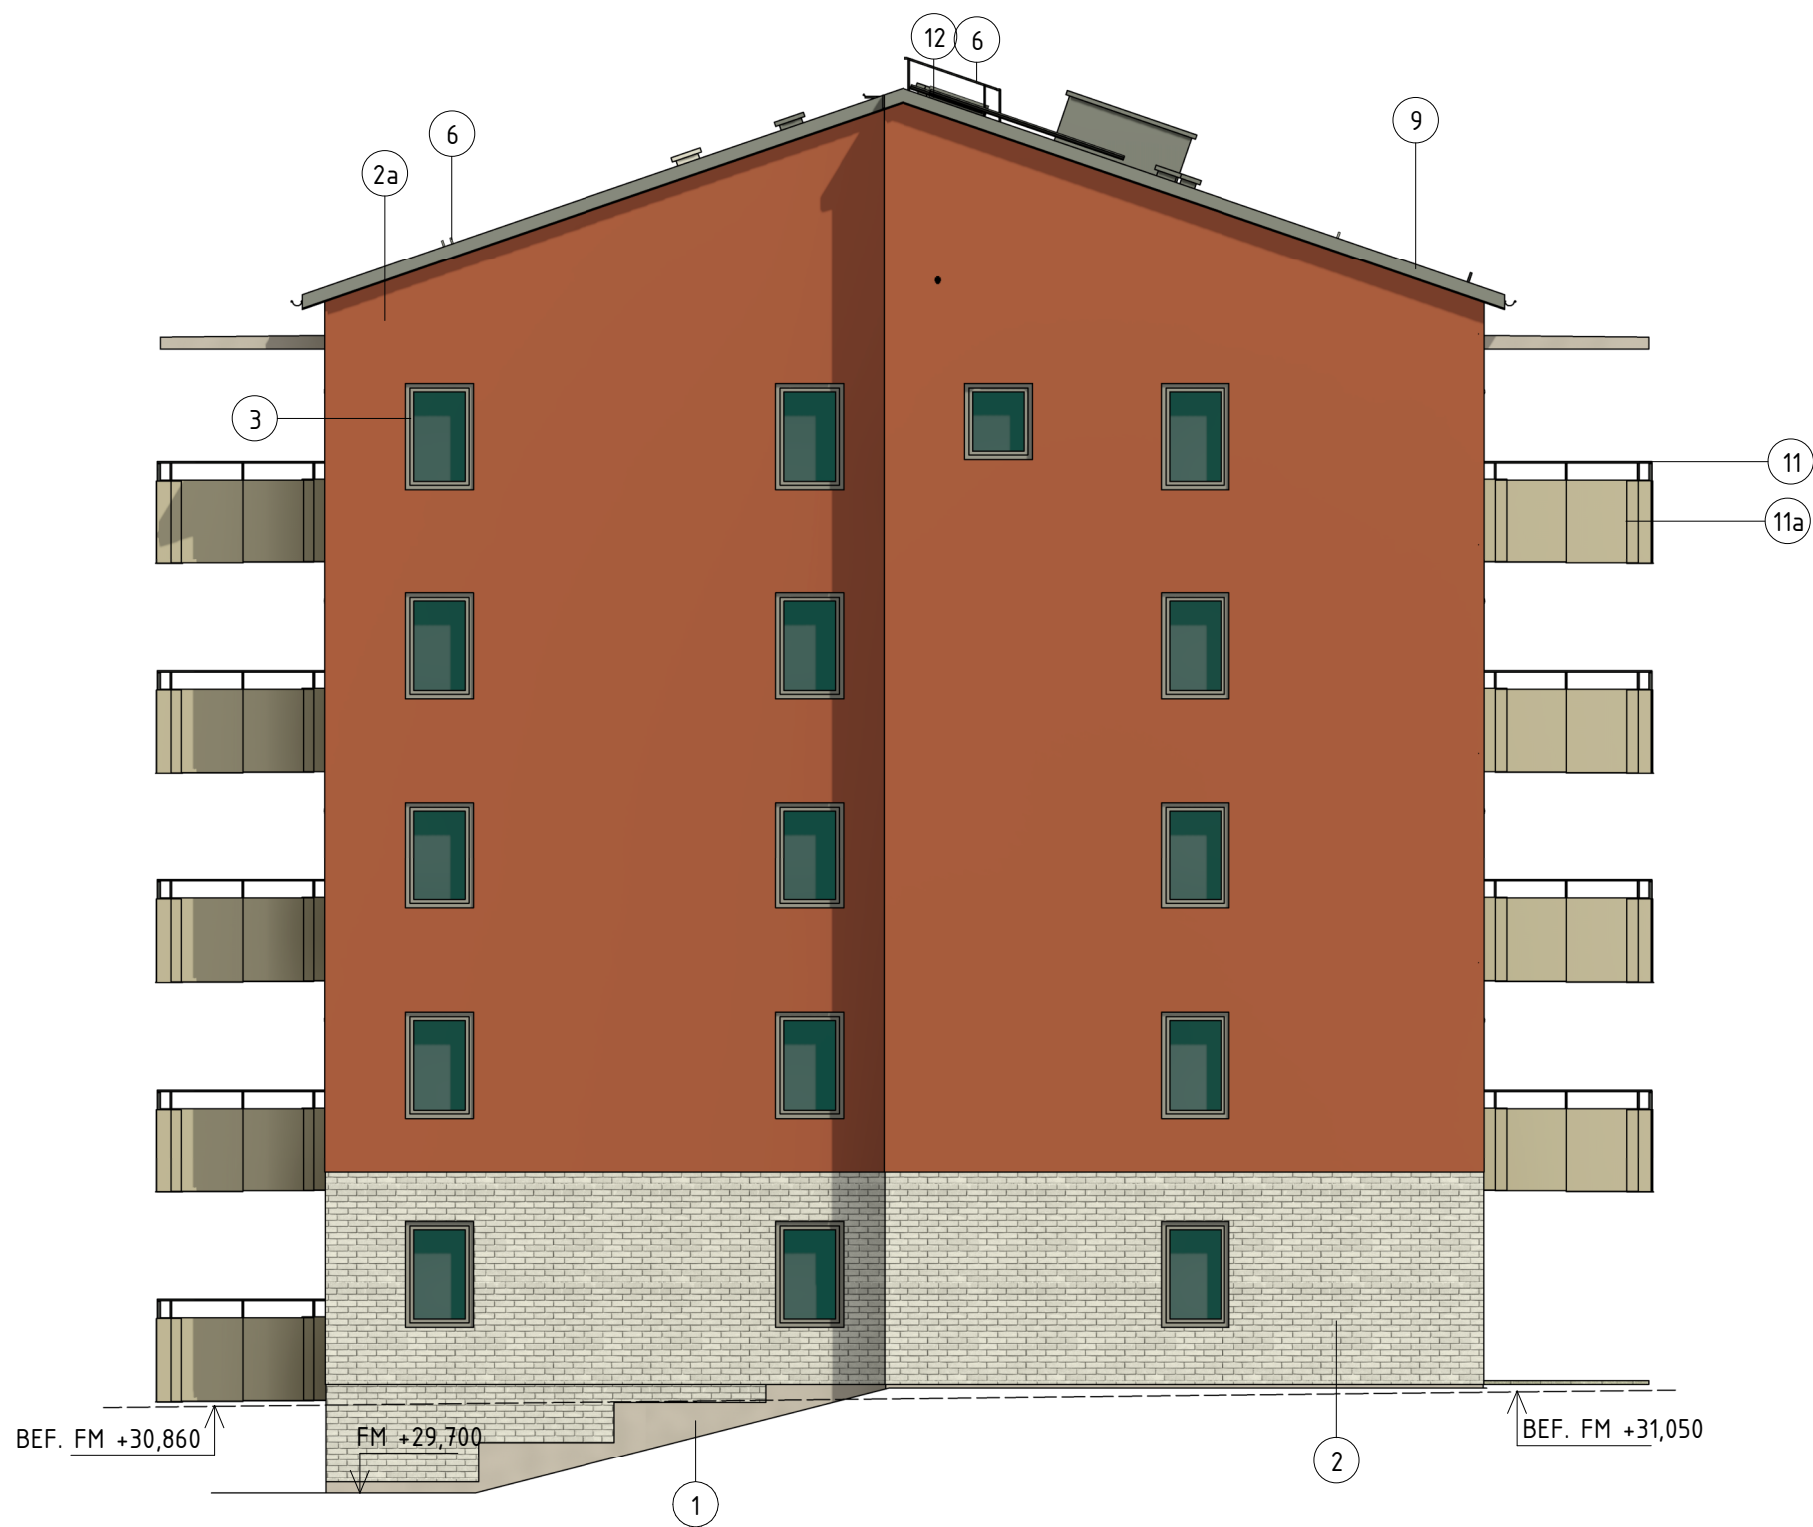

FASAD MOT SYDÖST



FASAD MOT NORDÖST



FASAD MOT NORDVÄST

BET	ÄNDRINGEN AVSER	DATUM	SIGN
BYGGLOVSHANDLING			
JSB VI BYGGER FÖR FLER			
			
☒	A MINJAR AB	0739-10 00 98	
☐	K MINJAR AB	0739-10 01 14	
☐	VS COMFORT-KEDJAN AB	019-777 02 00	
☐	V VENTEX ENTREPRENAD AB	0456-135 95	
☐	E ETG EL-TELEGRUPPEN AB	0454-30 64 97	
☐	M XXXXXXX		
☐	G GEO-KONSULT	XXXXXXXXXX	
UPPDRAGS NR 9801030	RITAD/KONSTR. AV OF	HANDLÄGGARE SG	
DATUM 2021-12-22	ANSVARIG SARAH GHAZIEH		
SKEVIK 1:190, VÄRMDÖ BOMINI/BAS- 6-SPÄNNARE HUS A FASADER			
SKALA A1 1:100	SKALA A3 1:200	NUMMER A-40-3-151	BET

0 1 2 3 4 5 6 7 8 9 10m
SKALA 1:100